


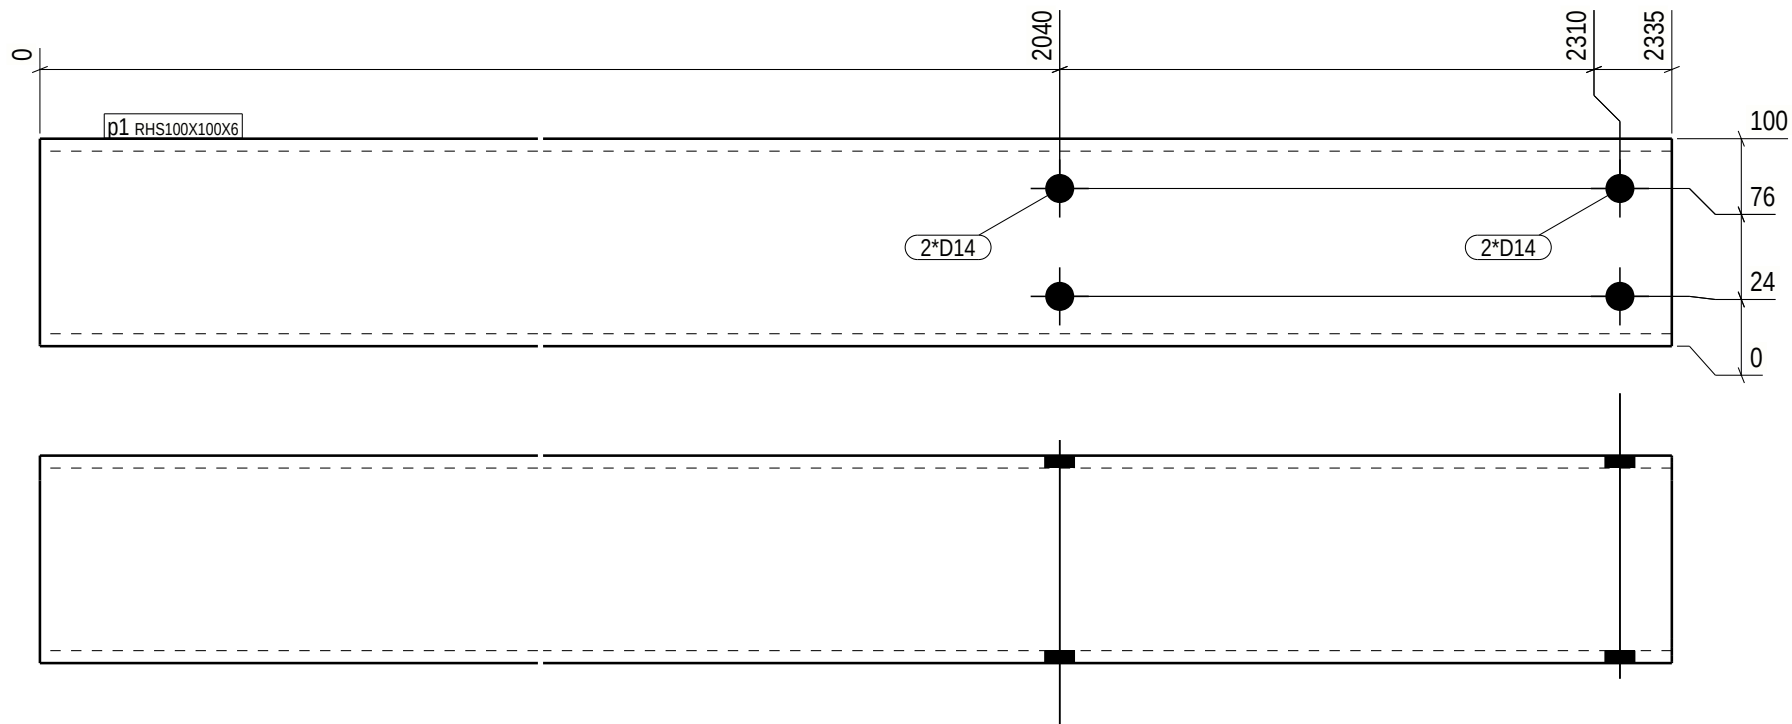

GENERAL NOTES:

For your safety, check weight before handling:
0-5kg Light 5-15kg Normal 15+kg Heavy

MATERIAL LIST FOR PART - p1

8 PARTS REQUIRED

POS. No.	PROFILE	No.	GRADE	L (mm)	AREA (m ²)	WEIGHT (kg)
p1	RHS100X100X6	1	S355J2H	2335	0.9	39.5 !!
TOTAL WEIGHT FOR				8	PARTS	316.0

Part list	Qty.
OP	8

Execution class: EXC 2

No utilization on drawings = over 50%

V-SEAM
Utilization under 50%
EXC 2=> Acc. to process control
EXC 3=> 20% UT
Utilization over 50%
EXC 2=> 10% UT
EXC 3=> 20% UT

* o 3 0 4 8 0 - 1 *



DS Skalkonstruktion

* W p 1 *

PROJECT	Akkasæter Lager- og vedlikeholdshall		PHASE	1 / Phase 1
MEMBER	Portomfatning	QUANTITY:	8	PROJECT No 30480-1
REVISION		ISSUED:	03.11.2025	DRAWING No. p.1
		DRAFTER:	ZLL	
		BIM control:	SST	