


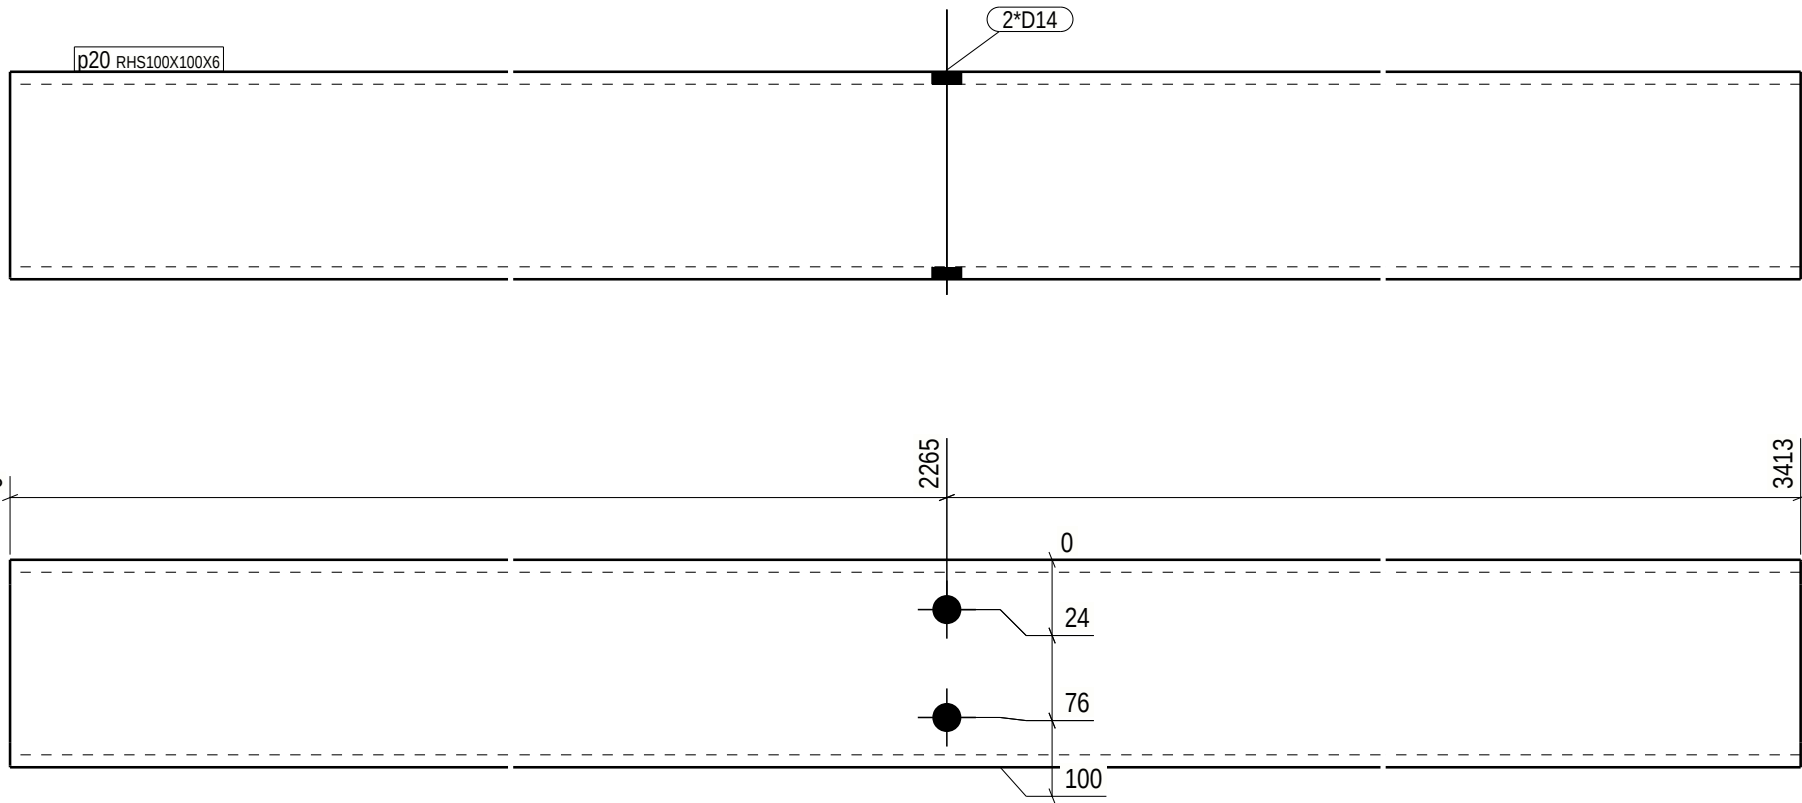

GENERAL NOTES:

For your safety, check weight before handling:
0-5kg Light 5-15kg Normal 15+kg Heavy

MATERIAL LIST FOR PART - p20

1 PARTS REQUIRED

POS. No.	PROFILE	No.	GRADE	L (mm)	AREA (m ²)	WEIGHT (kg)
p20	RHS100X100X6	1	S355J2H	3413	1.3	57.7 !!

TOTAL WEIGHT FOR 1 PARTS 57.7

Part list	Qty.
OP	1

Execution class: EXC 2

No utilization on drawings = over 50%

V-SEAM
Utilization under 50%
EXC 2=> Acc. to process control
EXC 3=> 20% UT
Utilization over 50%
EXC 2=> 10% UT
EXC 3=> 20% UT

* o 3 0 4 8 0 - 1 *



DS Skanska Construction

* W p 2 0 *

PROJECT	Akkasæter Lager- og vedlikeholdshall	PHASE	1 / Phase 1
MEMBER	Portomfatning	QUANTITY:	1
REVISION	ISSUED: 03.11.2025	DRAFTER:	ZLL
		BIM control:	SST
		PROJECT No	30480-1
		DRAWING No.	p.20