


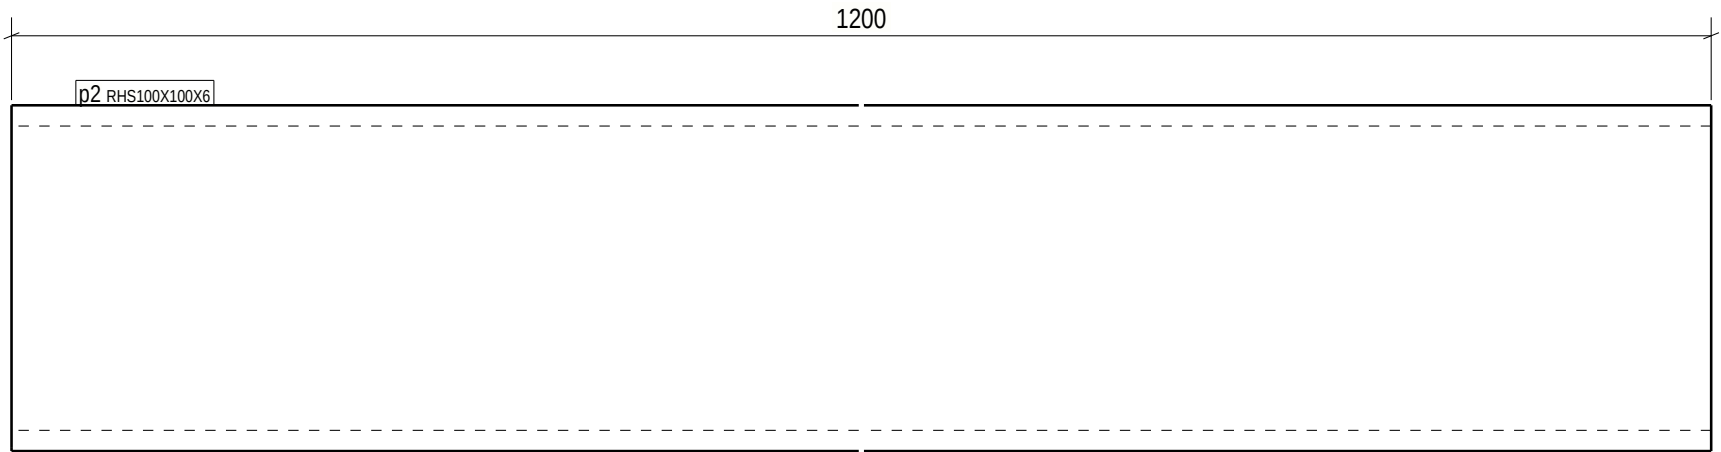

GENERAL NOTES:		For your safety, check weight before handling: 0-5kg Light 5-15kg Normal 15+kg Heavy				
MATERIAL LIST FOR PART - p2				24 PARTS REQUIRED		
POS. No.	PROFILE	No.	GRADE	L (mm)	AREA (m ²)	WEIGHT (kg)
p2	RHS100X100X6	1	S355J2H	1200	0.5	20.3 !!
TOTAL WEIGHT FOR				24	PARTS	487.1

Execution class: EXC 2		* o 3 0 4 8 0 - 1 *  DS <i>Skalkonstruktion</i> * W p 2 *			
No utilization on drawings = over 50%		PROJECT	Akkasæter Lager- og vedlikeholdshall		PHASE 1 / Phase 1
V-SEAM Utilization under 50% EXC 2=> Acc. to process control EXC 3=> 20% UT Utilization over 50% EXC 2=> 10% UT EXC 3=> 20% UT		MEMBER	Portomfatning		QUANTITY: 24
		REVISION		ISSUED: 03.11.2025	DRAFTER: ZLL BIM control: SST
				PROJECT No 30480-1	
				DRAWING No. p.2	