


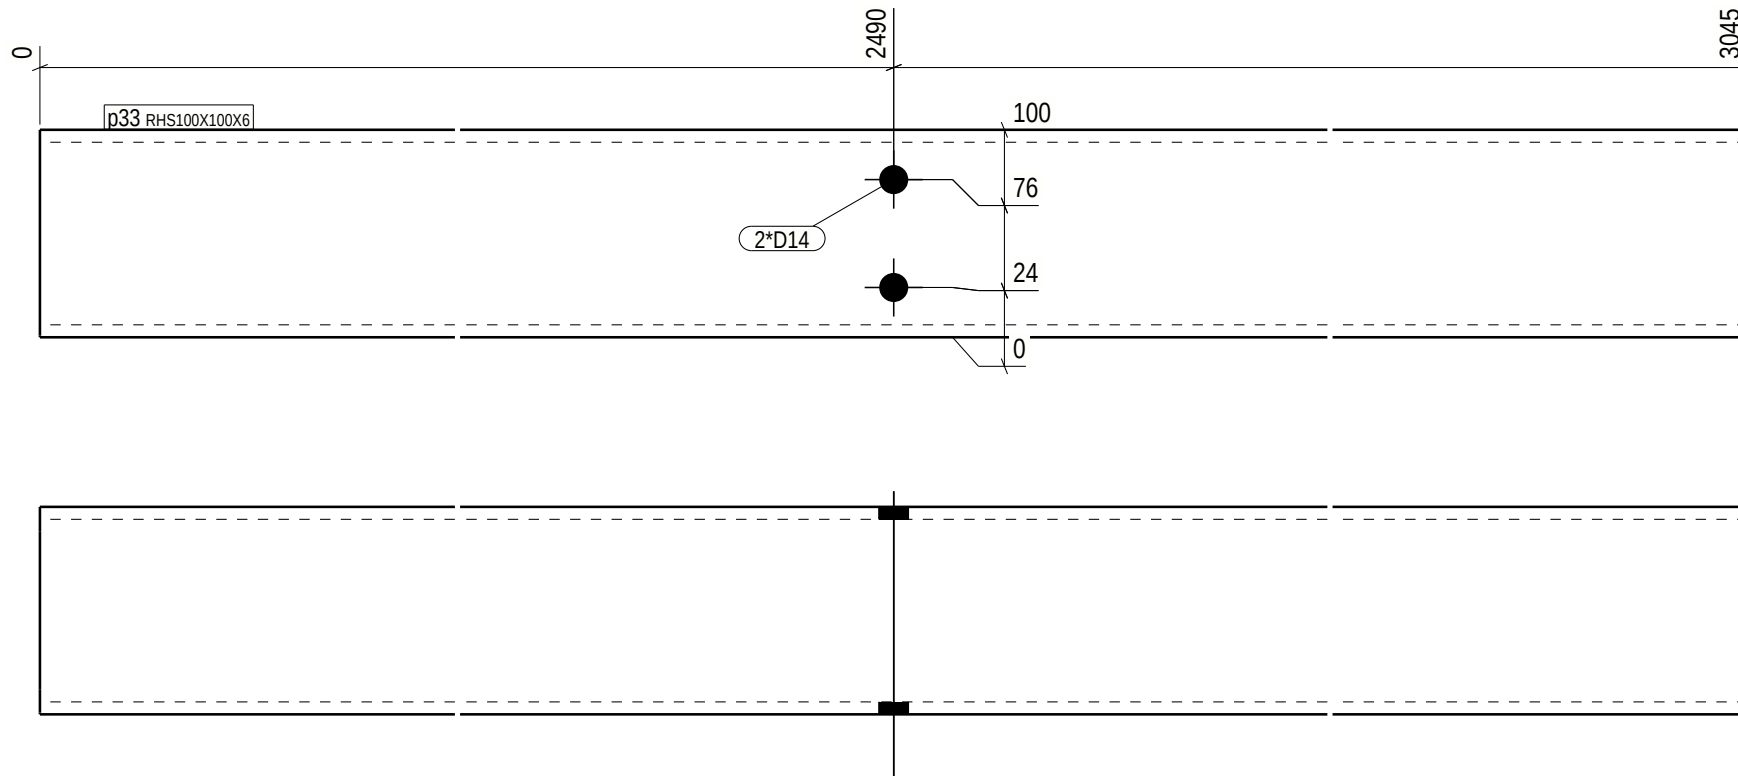

GENERAL NOTES:		For your safety, check weight before handling:				
		0-5kg Light 5-15kg Normal 15+kg Heavy				
MATERIAL LIST FOR PART - p33		1 PARTS REQUIRED				
POS. No.	PROFILE	No.	GRADE	L (mm)	AREA (m ²)	WEIGHT (kg)
p33	RHS100X100X6	1	S355J2H	3045	1.2	51.5 !!
TOTAL WEIGHT FOR		1	PARTS	51.5		

Execution class: EXC 2	
No utilization on drawings = over 50%	
V-SEAM Utilization under 50% EXC 2=> Acc. to process control EXC 3=> 20% UT Utilization over 50% EXC 2=> 10% UT EXC 3=> 20% UT	
Part list	Qty.
OP	1

* o 3 0 4 8 0 - 1 *		 DS <i>Skalkonstruktion</i>		* W p 3 3 *	
PROJECT	Akkasæter Lager- og vedlikeholdshall		PHASE	1 / Phase 1	
MEMBER	Portomfatning		QUANTITY:	1	PROJECT No 30480-1
REVISION	ISSUED: 03.11.2025		DRAFTER: BIM control:	ZLL SST	DRAWING No. p.33