


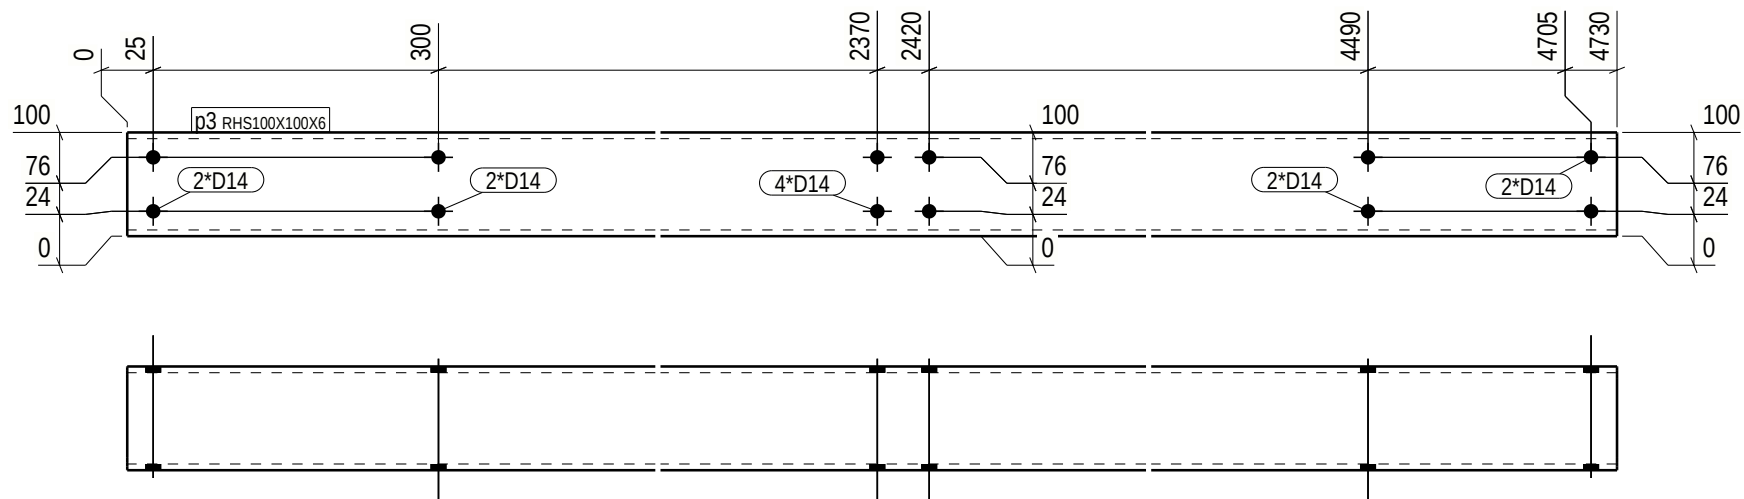

## GENERAL NOTES:

For your safety, check weight before handling:  
0-5kg Light 5-15kg Normal 15+kg Heavy

## MATERIAL LIST FOR PART - p3

4 PARTS REQUIRED

| POS. No. | PROFILE      | No. | GRADE   | L (mm) | AREA (m <sup>2</sup> ) | WEIGHT (kg) |
|----------|--------------|-----|---------|--------|------------------------|-------------|
| p3       | RHS100X100X6 | 1   | S355J2H | 4730   | 1.8                    | 80.0 !!     |

TOTAL WEIGHT FOR 4 PARTS 320.0

| Part list | Qty. |
|-----------|------|
| OP        | 4    |

## Execution class: EXC 2

No utilization on drawings = over 50%

V-SEAM  
Utilization under 50%  
EXC 2=> Acc. to process control  
EXC 3=> 20% UT  
Utilization over 50%  
EXC 2=> 10% UT  
EXC 3=> 20% UT

\* o 3 0 4 8 0 - 1 \*



DS Svalkonstruktion \* W p 3 \*

|          |                                      |                    |                       |             |                    |
|----------|--------------------------------------|--------------------|-----------------------|-------------|--------------------|
| PROJECT  | Akkasæter Lager- og vedlikeholdshall |                    | PHASE                 | 1 / Phase 1 |                    |
| MEMBER   | Portomfatning                        |                    | QUANTITY:             | 4           | PROJECT No 30480-1 |
| REVISION |                                      | ISSUED: 03.11.2025 | DRAFTER: BIM control: | ZLL SST     | DRAWING No. p.3    |