


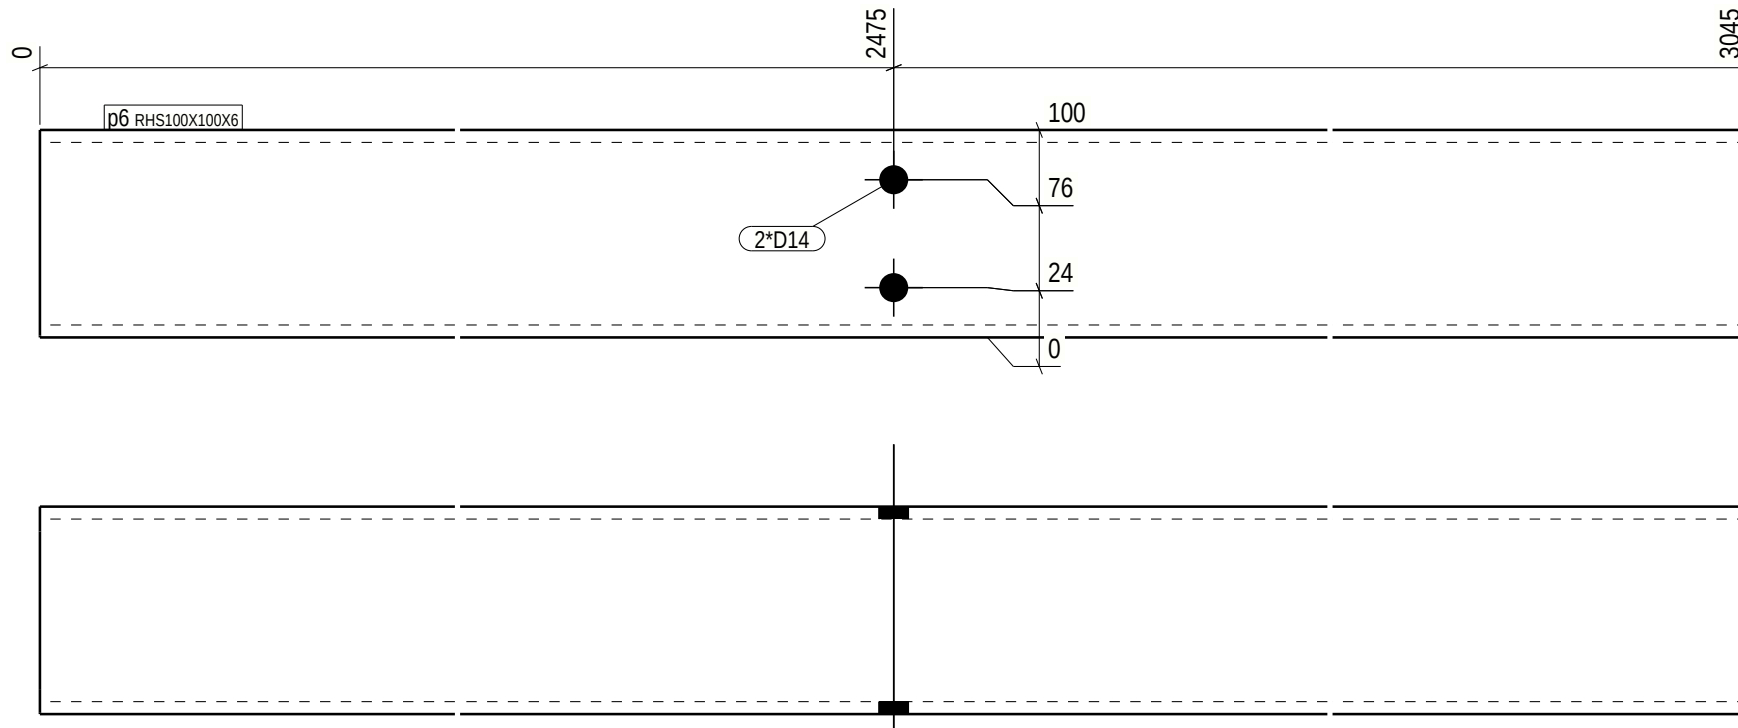

GENERAL NOTES:		For your safety, check weight before handling: 0-5kg Light 5-15kg Normal 15+kg Heavy				
MATERIAL LIST FOR PART - p6		1 PARTS REQUIRED				
POS. No.	PROFILE	No.	GRADE	L (mm)	AREA (m ²)	WEIGHT (kg)
p6	RHS100X100X6	1	S355J2H	3045	1.2	51.5 !!
TOTAL WEIGHT FOR		1	PARTS			51.5

Part list	Qty.
OP	1

Execution class: EXC 2		* o 3 0 4 8 0 - 1 *  DS <i>Skalkonstruktion</i> * W p 6 *			
No utilization on drawings = over 50%					
V-SEAM Utilization under 50% EXC 2=> Acc. to process control EXC 3=> 20% UT Utilization over 50% EXC 2=> 10% UT EXC 3=> 20% UT		PROJECT	Akkasæter Lager- og vedlikeholdshall		PHASE 1 / Phase 1
		MEMBER	Portomfatning		QUANTITY: 1 PROJECT No 30480-1
		REVISION	ISSUED: 03.11.2025		DRAFTER: ZLL BIM control: SST DRAWING No. p.6