


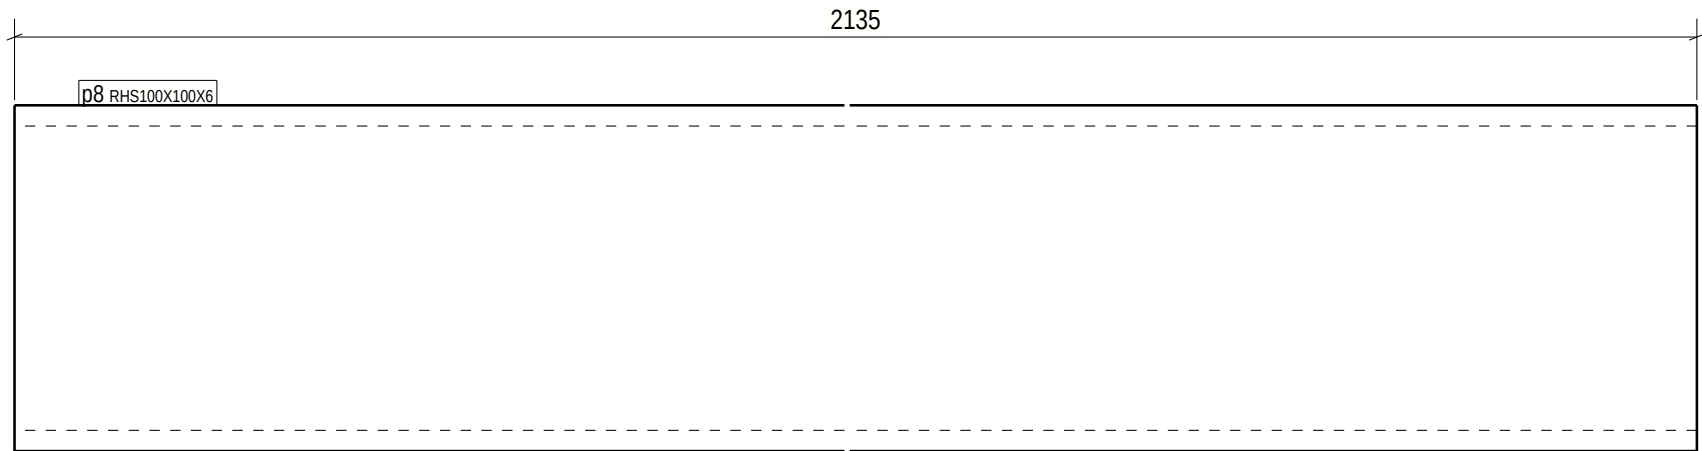

GENERAL NOTES:		For your safety, check weight before handling: 0-5kg Light 5-15kg Normal 15+kg Heavy				
MATERIAL LIST FOR PART - p8				1 PARTS REQUIRED		
POS. No.	PROFILE	No.	GRADE	L (mm)	AREA (m ²)	WEIGHT (kg)
p8	RHS100X100X6	1	S355J2H	2135	0.8	36.1 !!
TOTAL WEIGHT FOR				1	PARTS	36.1

Execution class: EXC 2	
No utilization on drawings = over 50%	
Part list	V-SEAM
	Utilization under 50%
	EXC 2=> Acc. to process control
	EXC 3=> 20% UT
Qty.	Utilization over 50%
	EXC 2=> 10% UT
	EXC 3=> 20% UT
OP	1

* o 3 0 4 8 0 - 1 *  DS <i>Skalkonstruktion</i> * W p 8 *			
PROJECT	Akkasæter Lager- og vedlikeholdshall		PHASE 1 / Phase 1
MEMBER	Portomfatning	QUANTITY: 1	PROJECT No 30480-1
REVISION	ISSUED: 03.11.2025	DRAFTER: ZLL BIM control: SST	DRAWING No. p.8