


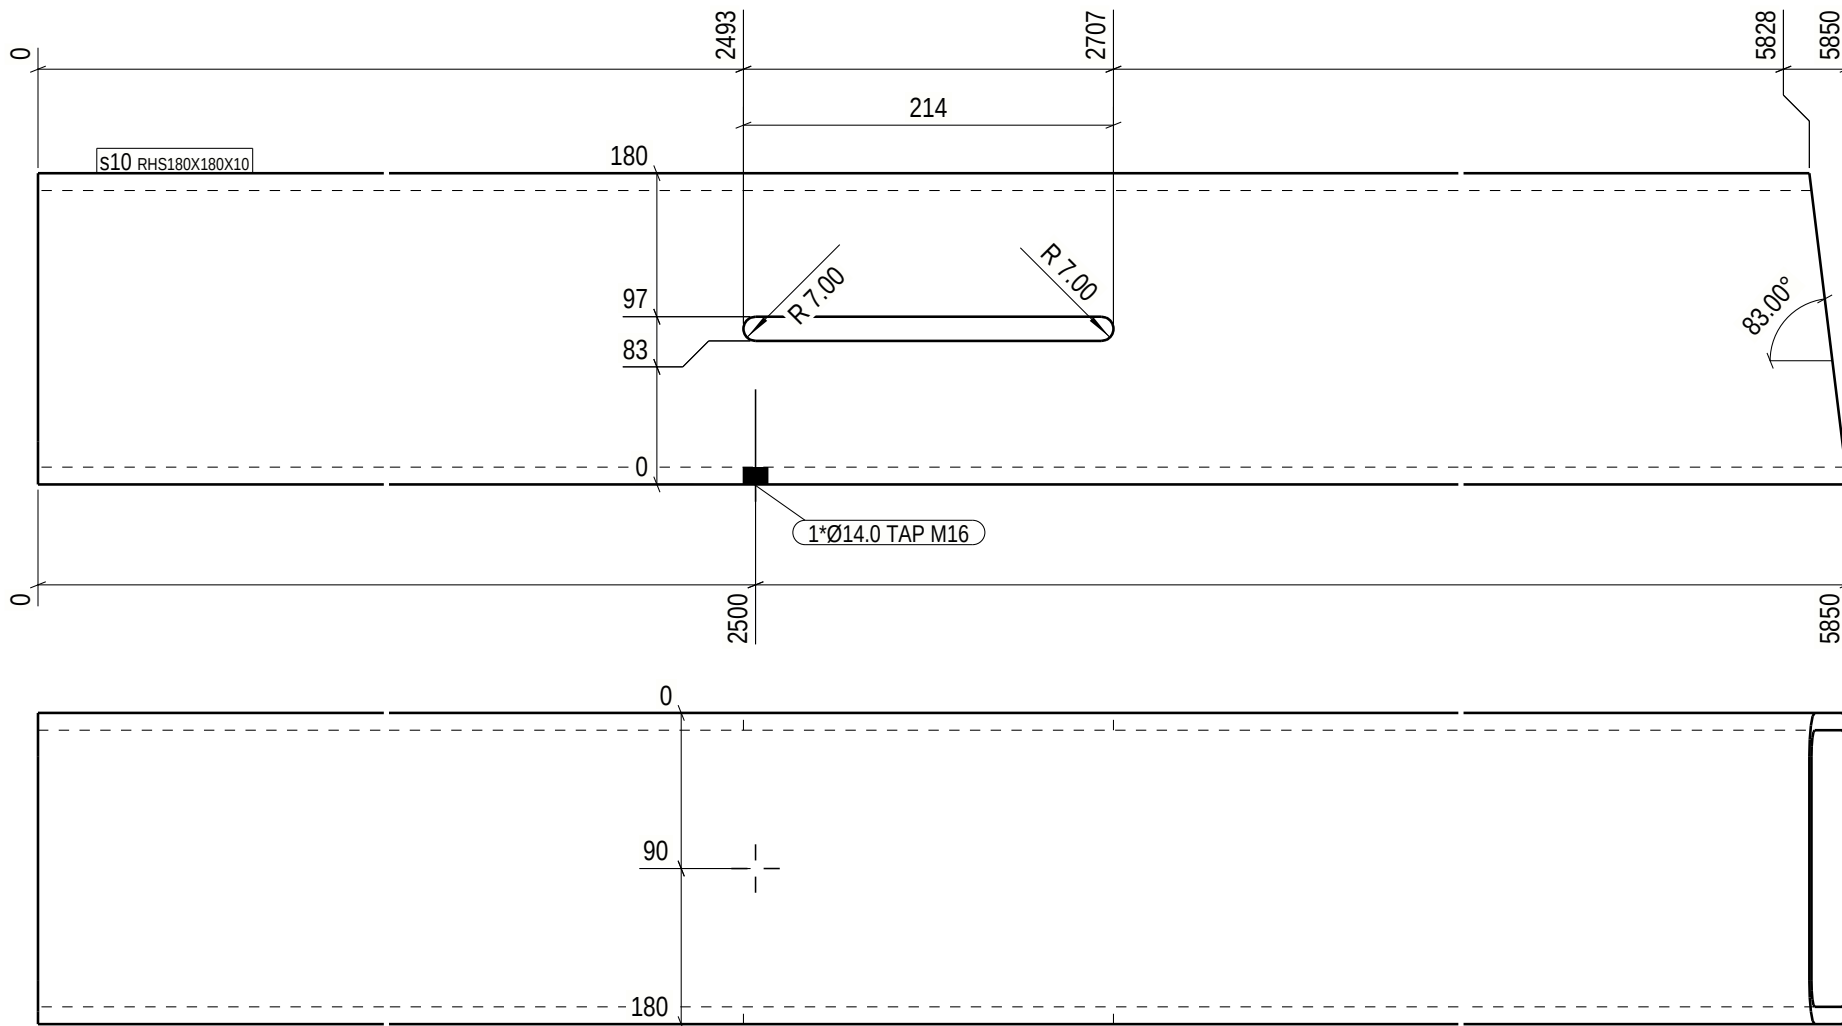

GENERAL NOTES: For your safety, check weight before handling:
0-5kg Light 5-15kg Normal 15+kg Heavy

MATERIAL LIST FOR PART - S10						1 PARTS REQUIRED
POS. No.	PROFILE	No.	GRADE	L (mm)	AREA (m ²)	WEIGHT (kg)
s10	RHS180X180X10	1	S355J2H	5850	4.0	294.0 !!
TOTAL WEIGHT FOR						1 PARTS 294.0

Execution class: EXC 2

No utilization on drawings = over 50%

V-SEAM
Utilization under 50%
EXC 2=> Acc. to process control
EXC 3=> 20% UT
Utilization over 50%
EXC 2=> 10% UT
EXC 3=> 20% UT

Part list	Qty.
GS	1

* o 3 0 4 8 0 - 1 *  DS <i>Skalkonstruktion</i> * W s 1 0 *			
PROJECT	Akkasæter Lager- og vedlikeholdshall		PHASE 1 / Phase 1
MEMBER	Søyle	QUANTITY: 1	PROJECT No 30480-1
REVISION	ISSUED: 03.11.2025	DRAFTER: ZLL BIM control: SST	DRAWING No. s.10