


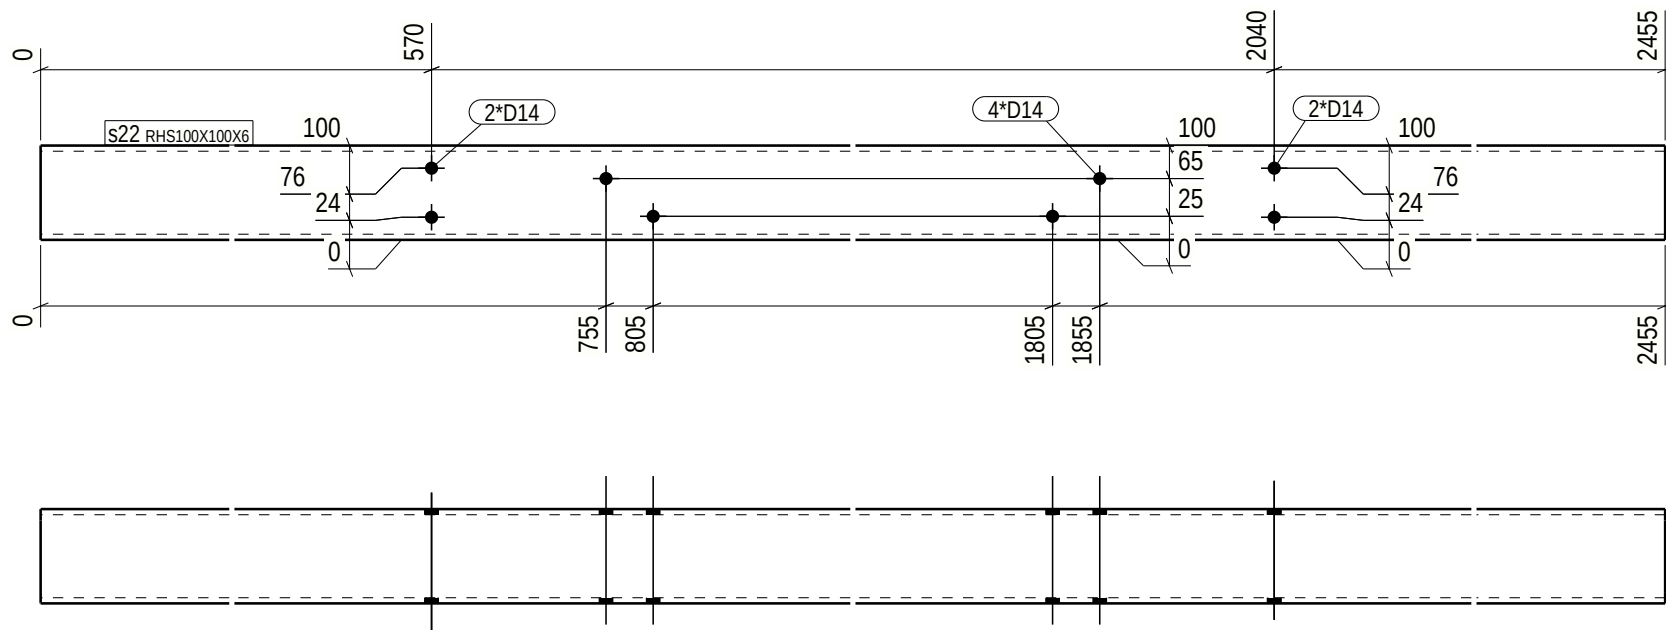

GENERAL NOTES: For your safety, check weight before handling: 0-5kg Light 5-15kg Normal 15+kg Heavy						
MATERIAL LIST FOR PART - S22				2 PARTS REQUIRED		
POS. No.	PROFILE	No.	GRADE	L (mm)	AREA (m ²)	WEIGHT (kg)
s22	RHS100X100X6	1	S355J2H	2455	0.9	41.5 !!
TOTAL WEIGHT FOR				2	PARTS	83.0

Part list	Qty.
GS	2

Execution class: EXC 2	
No utilization on drawings = over 50%	
V-SEAM Utilization under 50% EXC 2=> Acc. to process control EXC 3=> 20% UT Utilization over 50% EXC 2=> 10% UT EXC 3=> 20% UT	

* o 3 0 4 8 0 - 1 *  DS <i>Skalkonstruktion</i> * W s 2 2 *			
PROJECT	Akkasæter Lager- og vedlikeholdshall		PHASE 1 / Phase 1
MEMBER	Søyle	QUANTITY: 2	PROJECT No 30480-1
REVISION		ISSUED: 03.11.2025	DRAFTER: ZLL BIM control: SST DRAWING No. s.22