


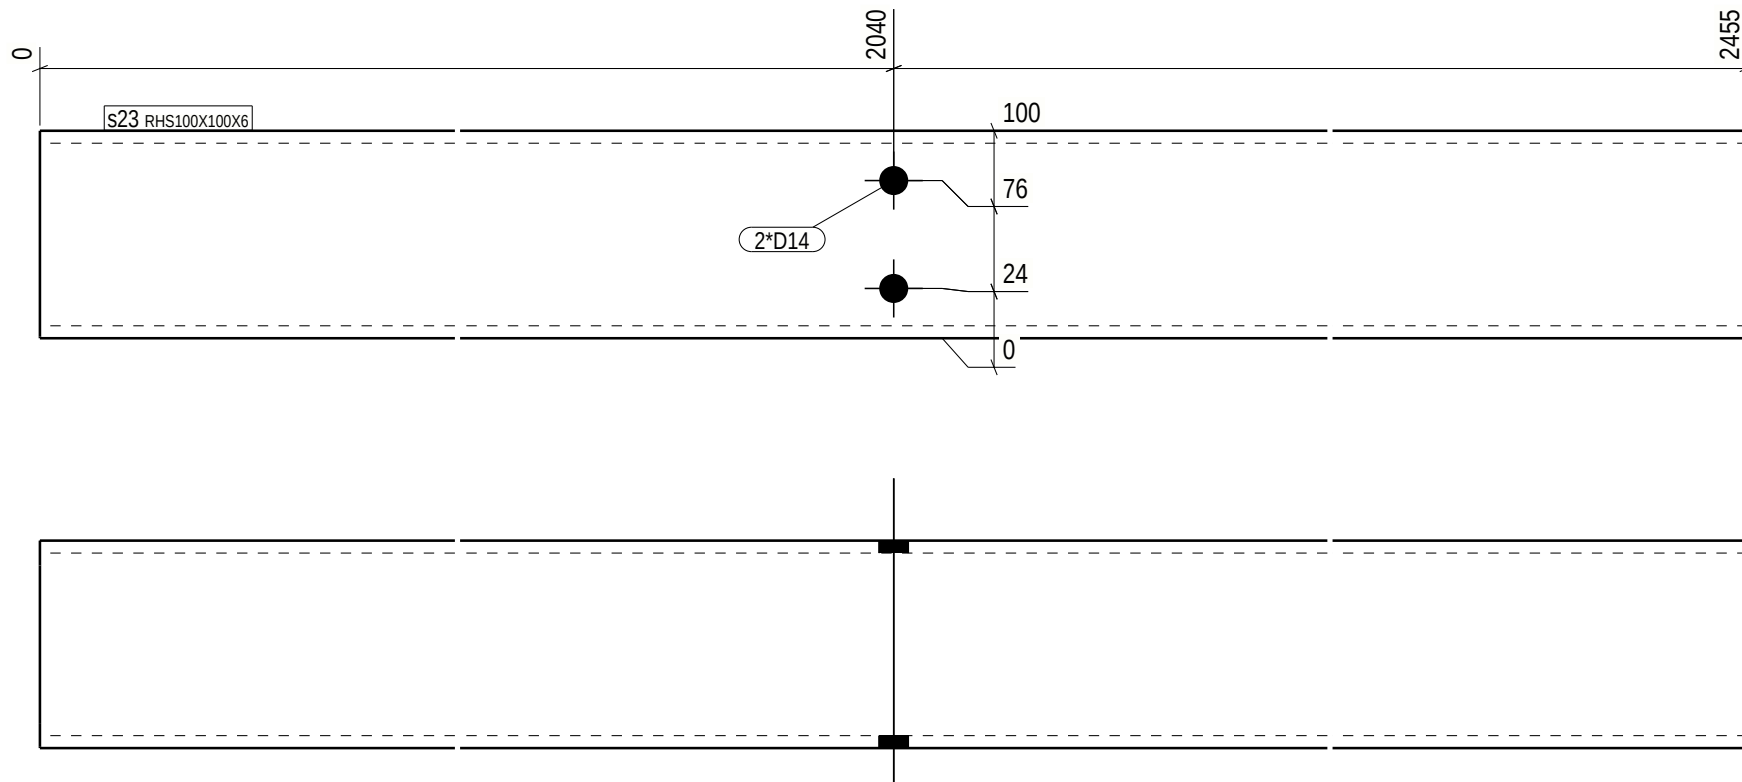

GENERAL NOTES: For your safety, check weight before handling:
0-5kg Light 5-15kg Normal 15+kg Heavy

MATERIAL LIST FOR PART - **S23** 2 PARTS REQUIRED

POS. No.	PROFILE	No.	GRADE	L (mm)	AREA (m ²)	WEIGHT (kg)
s23	RHS100X100X6	1	S355J2H	2455	0.9	41.5 !!
TOTAL WEIGHT FOR		2	PARTS			83.0

Part list	Qty.
GS	2

Execution class: EXC 2

No utilization on drawings = over 50%

V-SEAM
Utilization under 50%
EXC 2=> Acc. to process control
EXC 3=> 20% UT
Utilization over 50%
EXC 2=> 10% UT
EXC 3=> 20% UT

* o 3 0 4 8 0 - 1 *



DS Skalkonstruktion

* W s 2 3 *

PROJECT	Akkasæter Lager- og vedlikeholdshall		PHASE	1 / Phase 1
MEMBER	Søyle	QUANTITY:	2	PROJECT No 30480-1
REVISION		ISSUED:	03.11.2025	DRAWING No. s.23
		DRAFTER:	ZLL	
		BIM control:	SST	