


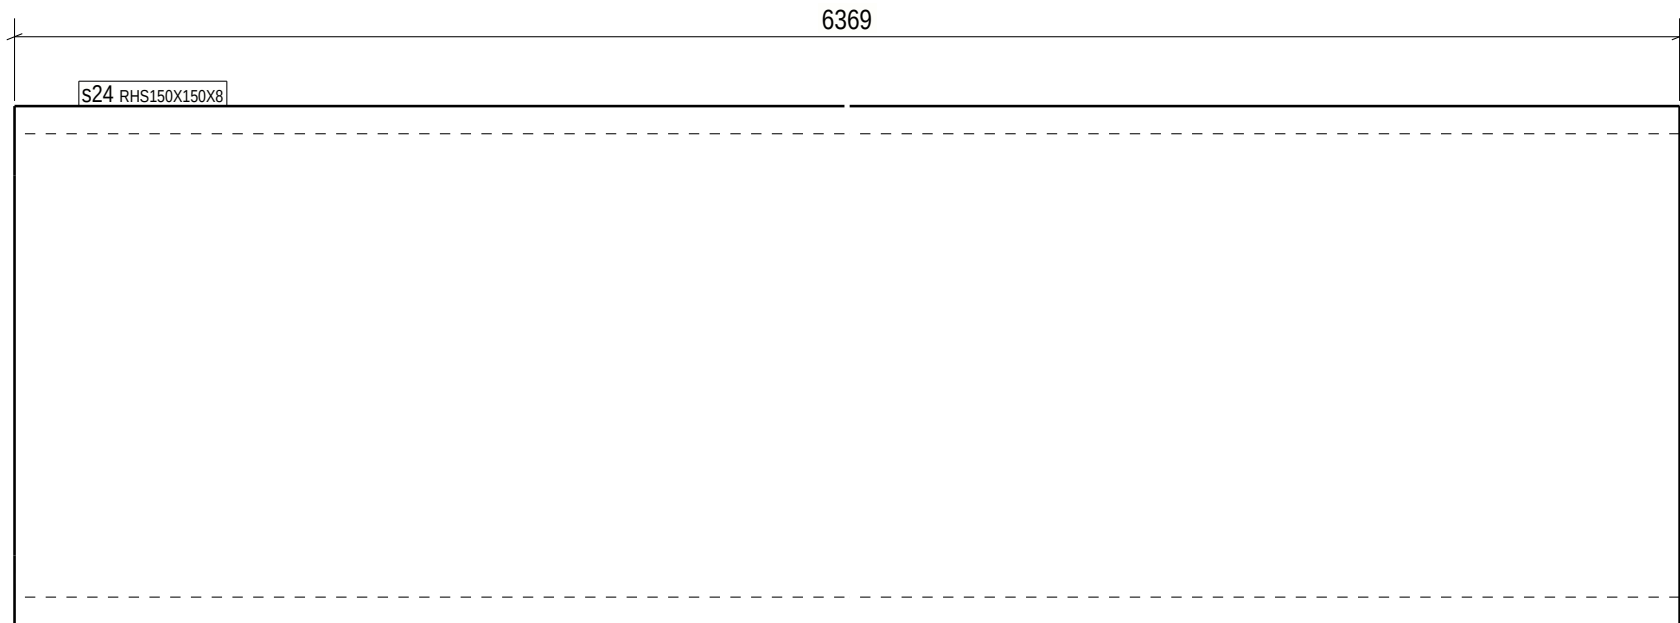

|                              |              |                                                                                               |         |                  |                        |             |
|------------------------------|--------------|-----------------------------------------------------------------------------------------------|---------|------------------|------------------------|-------------|
| GENERAL NOTES:               |              | For your safety, check weight before handling:<br>0-5kg Light    5-15kg Normal    15+kg Heavy |         |                  |                        |             |
| MATERIAL LIST FOR PART - S24 |              |                                                                                               |         | 1 PARTS REQUIRED |                        |             |
| POS. No.                     | PROFILE      | No.                                                                                           | GRADE   | L (mm)           | AREA (m <sup>2</sup> ) | WEIGHT (kg) |
| s24                          | RHS150X150X8 | 1                                                                                             | S355J2H | 6369             | 3.6                    | 215.2 !!    |
| TOTAL WEIGHT FOR             |              |                                                                                               |         | 1                | PARTS                  | 215.2       |

|                                                                                      |      |   |                                      |                                  |                                |
|--------------------------------------------------------------------------------------|------|---|--------------------------------------|----------------------------------|--------------------------------|
| Execution class: EXC 2                                                               |      | * o 3 0 4 8 0 - 1 *  <b>DS</b> <i>Stalkonstruktion</i> * W s 2 4 * |                                      |                                  |                                |
| No utilization on drawings = over 50%                                                |      | PROJECT   | Akkasæter Lager- og vedlikeholdshall |                                  | PHASE 1 / Phase 1              |
| V-SEAM<br>Utilization under 50%<br>EXC 2=> Acc. to process control<br>EXC 3=> 20% UT |      | MEMBER   | Søje                                 |                                  | QUANTITY: 1 PROJECT No 30480-1 |
| Utilization over 50%<br>EXC 2=> 10% UT<br>EXC 3=> 20% UT                             |      | REVISION   | ISSUED: 03.11.2025                   | DRAFTER: ZLL<br>BIM control: SST | DRAWING No. s.24               |
| Part list                                                                            | Qty. |   |                                      |                                  |                                |
| GS                                                                                   | 1    |   |                                      |                                  |                                |