


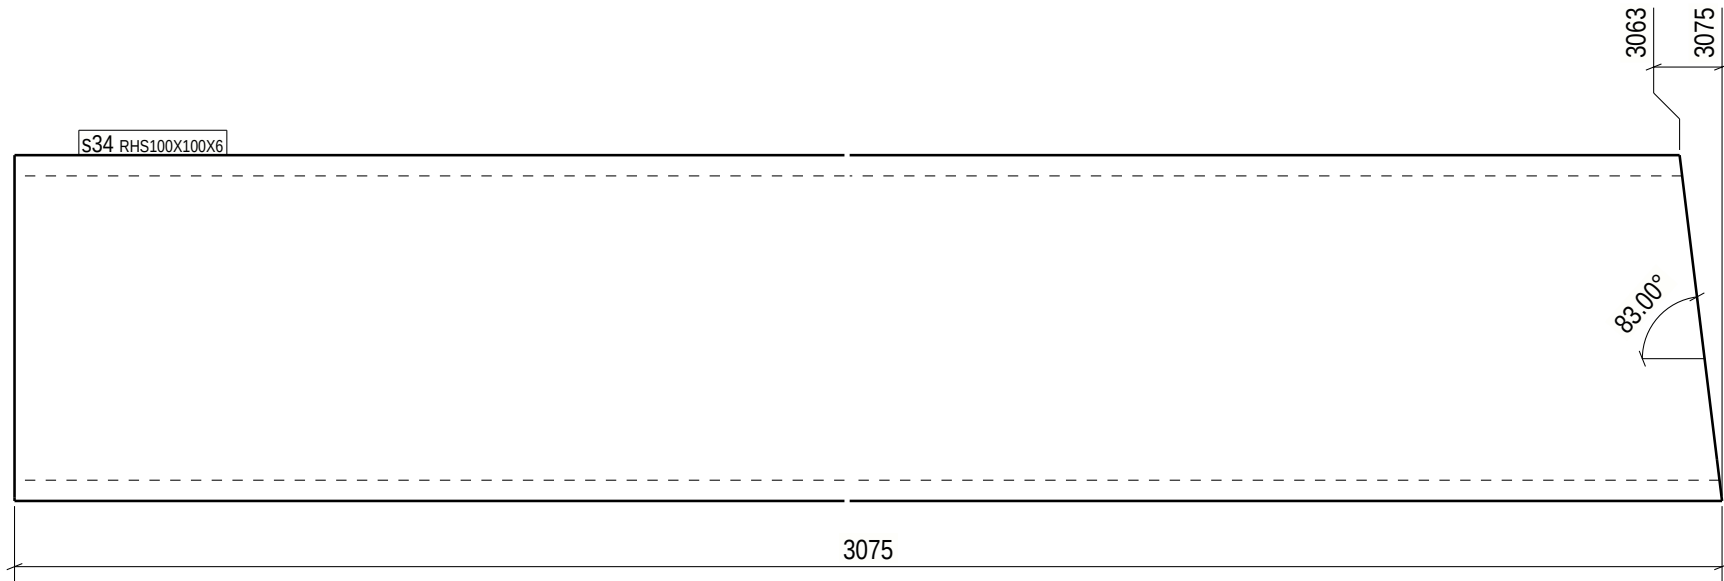

GENERAL NOTES:						
For your safety, check weight before handling:						
0-5kg Light 5-15kg Normal 15+kg Heavy						
MATERIAL LIST FOR PART - S34				1 PARTS REQUIRED		
POS. No.	PROFILE	No.	GRADE	L (mm)	AREA (m ²)	WEIGHT (kg)
s34	RHS100X100X6	1	S355J2H	3075	1.2	51.9 !!
TOTAL WEIGHT FOR				1	PARTS	51.9

Part list	Qty.
GS	1

Execution class: EXC 2		* o 3 0 4 8 0 - 1 *  DS <i>Skalkonstruktion</i> * W s 3 4 *			
No utilization on drawings = over 50%					
V-SEAM Utilization under 50% EXC 2=> Acc. to process control EXC 3=> 20% UT Utilization over 50% EXC 2=> 10% UT EXC 3=> 20% UT		PROJECT	Akkasæter Lager- og vedlikeholdshall		PHASE 1 / Phase 1
		MEMBER	Søyle		QUANTITY: 1 PROJECT No 30480-1
		REVISION	ISSUED: 03.11.2025		DRAFTER: ZLL BIM control: SST DRAWING No. s.34