


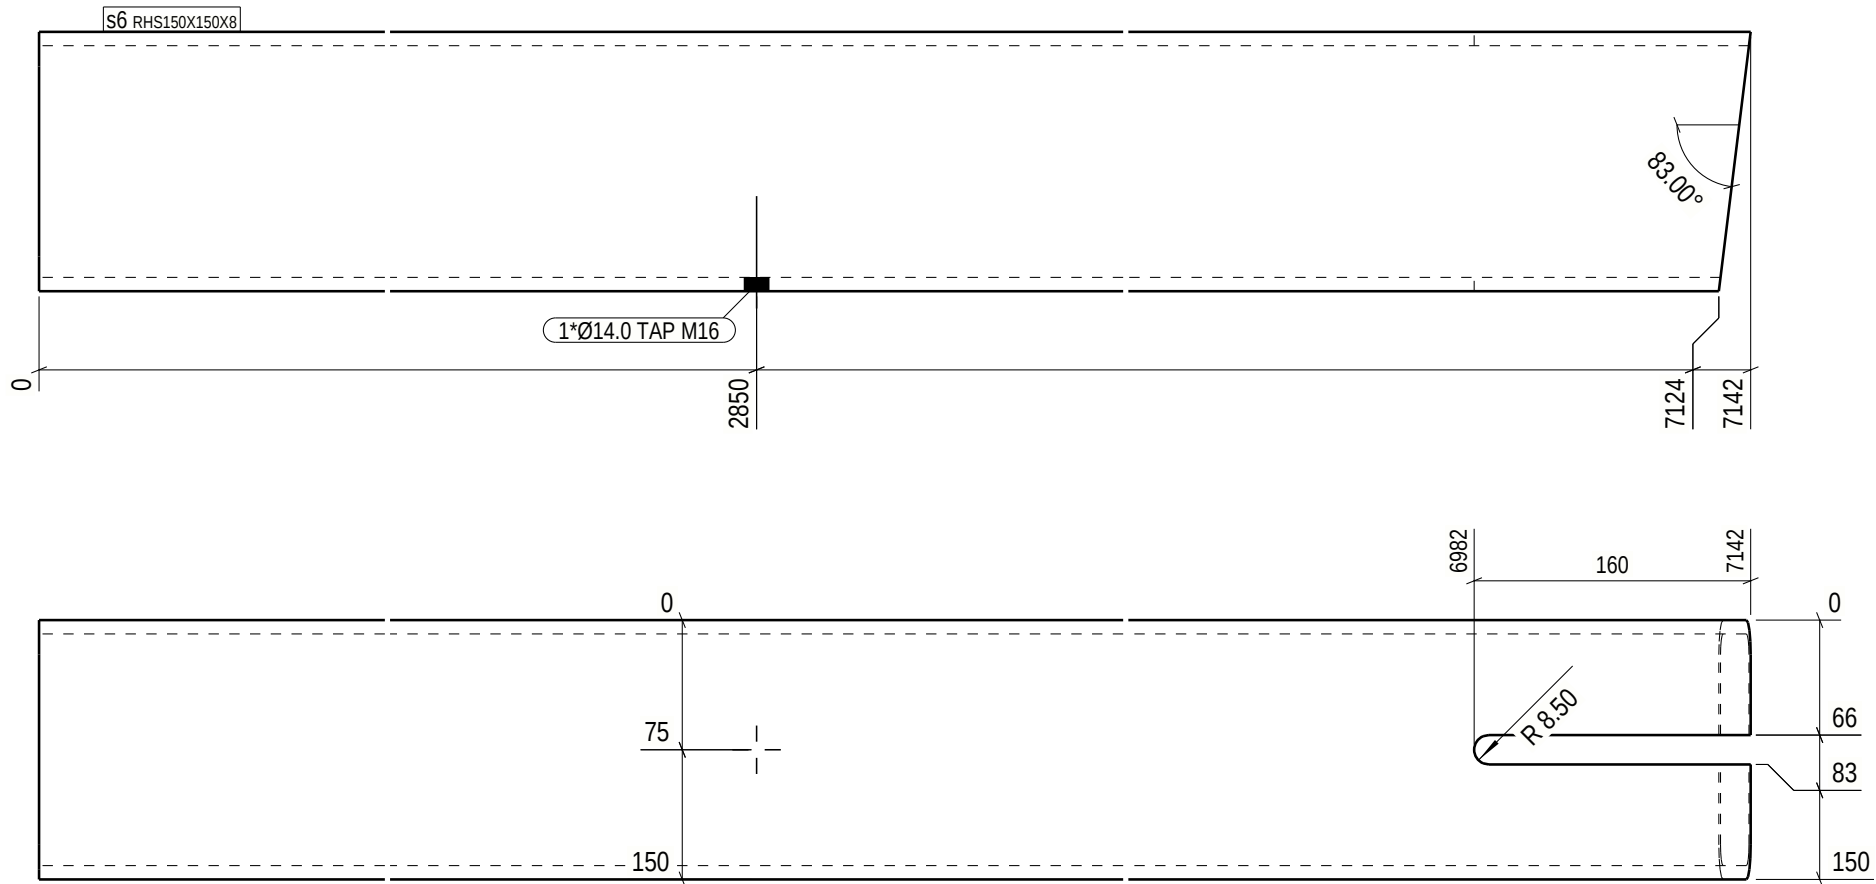

## GENERAL NOTES:

For your safety, check weight before handling:  
0-5kg Light 5-15kg Normal 15+kg Heavy

## MATERIAL LIST FOR PART - S6

1 PARTS REQUIRED

| POS. No. | PROFILE      | No. | GRADE   | L (mm) | AREA (m <sup>2</sup> ) | WEIGHT (kg) |
|----------|--------------|-----|---------|--------|------------------------|-------------|
| s6       | RHS150X150X8 | 1   | S355J2H | 7142   | 4.1                    | 240.7 !!    |

TOTAL WEIGHT FOR 1 PARTS 240.7

| Part list | Qty. |
|-----------|------|
| GS        | 1    |

## Execution class: EXC 2

No utilization on drawings = over 50%

V-SEAM  
Utilization under 50%  
EXC 2=> Acc. to process control  
EXC 3=> 20% UT  
Utilization over 50%  
EXC 2=> 10% UT  
EXC 3=> 20% UT

\* o 3 0 4 8 0 - 1 \*



DS Sivilkonstruksjon

\* W s 6 \*

|          |                                      |                    |              |                  |                    |
|----------|--------------------------------------|--------------------|--------------|------------------|--------------------|
| PROJECT  | Akkasæter Lager- og vedlikeholdshall |                    | PHASE        | 1 / Phase 1      |                    |
| MEMBER   | Søyle                                |                    | QUANTITY:    | 1                | PROJECT No 30480-1 |
| REVISION |                                      | ISSUED: 03.11.2025 | DRAFTER: ZLL | BIM control: SST | DRAWING No. S.6    |