


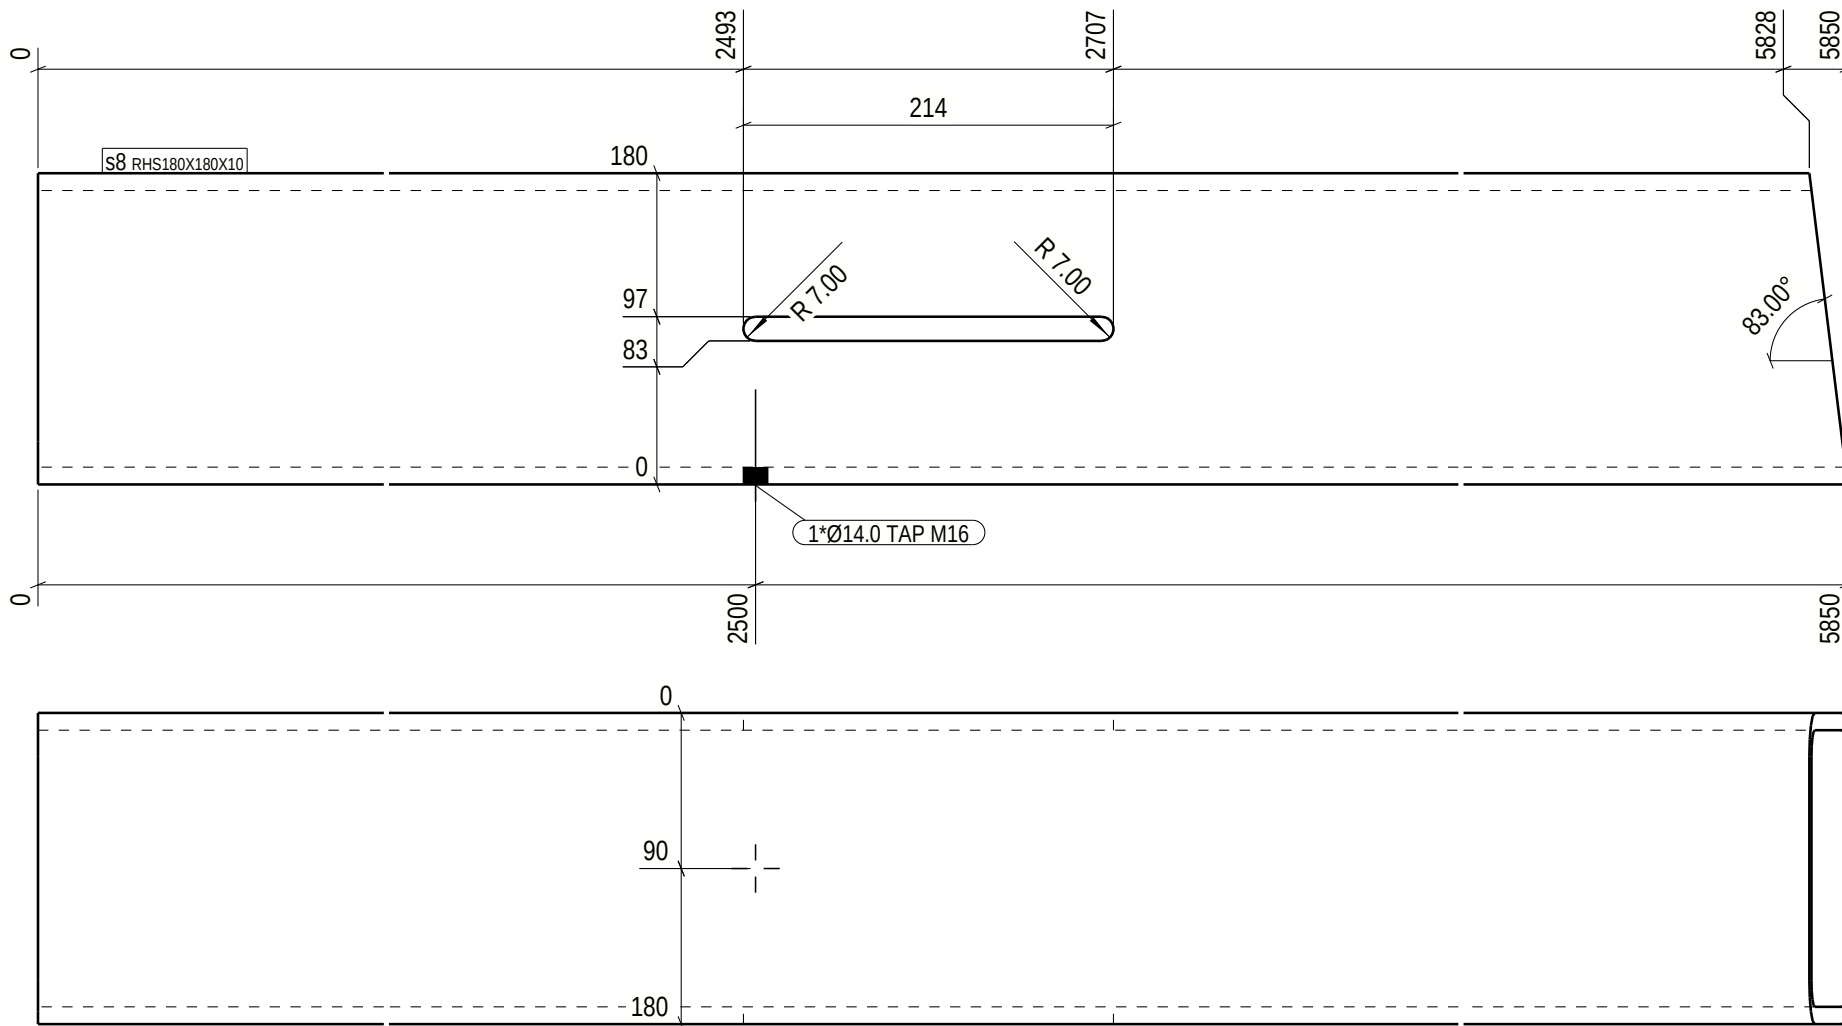

GENERAL NOTES:

For your safety, check weight before handling:
0-5kg Light 5-15kg Normal 15+kg Heavy

MATERIAL LIST FOR PART - S8

1 PARTS REQUIRED

POS. No.	PROFILE	No.	GRADE	L (mm)	AREA (m ²)	WEIGHT (kg)
s8	RHS180X180X10	1	S355J2H	5850	4.0	294.0 !!

TOTAL WEIGHT FOR 1 PARTS 294.0

Execution class: EXC 2

No utilization on drawings = over 50%

V-SEAM
Utilization under 50%
EXC 2=> Acc. to process control
EXC 3=> 20% UT
Utilization over 50%
EXC 2=> 10% UT
EXC 3=> 20% UT

Part list	Qty.
GS	1

* o 3 0 4 8 0 - 1 *



DS Steelkonstruktion

* W s 8 *

PROJECT	Akkasæter Lager- og vedlikeholdshall	PHASE	1 / Phase 1
MEMBER	Søjle	QUANTITY:	1
REVISION		ISSUED:	03.11.2025
		DRAFTER:	ZLL
		BIM control:	SST
		PROJECT No	30480-1
		DRAWING No.	S.8