


|                                                |         |     |        |                  |                        |             |
|------------------------------------------------|---------|-----|--------|------------------|------------------------|-------------|
| GENERAL NOTES:                                 |         |     |        |                  |                        |             |
| For your safety, check weight before handling: |         |     |        |                  |                        |             |
| 0-5kg Light    5-15kg Normal    15+kg Heavy    |         |     |        |                  |                        |             |
| MATERIAL LIST FOR PART - x23                   |         |     |        | 4 PARTS REQUIRED |                        |             |
| POS. No.                                       | PROFILE | No. | GRADE  | L (mm)           | AREA (m <sup>2</sup> ) | WEIGHT (kg) |
| x23                                            | D30     | 1   | S355J2 | 5873             | 0.5                    | 31.1 !!     |
| TOTAL WEIGHT FOR                               |         |     |        | 4                | PARTS                  | 124.5       |

|           |      |
|-----------|------|
| Part list | Qty. |
| VX        | 4    |

|   |  |   |  |        |                                      |              |       |            |             |             |  |         |  |
|---|--|---|--|--------|--------------------------------------|--------------|-------|------------|-------------|-------------|--|---------|--|
| Execution class: EXC 2   |  | * o 3 0 4 8 0 - 1 *  <b>DS</b> <i>Skalkonstruktion</i> * W x 2 3 * |  |        |                                      |              |       |            |             |             |  |         |  |
| No utilization on drawings = over 50%   |  |   |  |        |                                      |              |       |            |             |             |  |         |  |
| V-SEAM<br>Utilization under 50%<br>EXC 2=> Acc. to process control<br>EXC 3=> 20% UT<br>Utilization over 50%<br>EXC 2=> 10% UT<br>EXC 3=> 20% UT |  | PROJECT   |  |        | Akkasæter Lager- og vedlikeholdshall |              | PHASE |            | 1 / Phase 1 |             |  |         |  |
|   |  | MEMBER   |  | Vind-X |                                      | QUANTITY:    |       | 4          |             | PROJECT No  |  | 30480-1 |  |
|   |  | REVISION   |  |        |                                      | ISSUED:      |       | 03.11.2025 |             | DRAFTER:    |  | ZLL     |  |
|   |  |   |  |        |                                      | BIM control: |       | SST        |             | DRAWING No. |  | x.23    |  |