


Tekla Structures



GENERAL NOTES:						
For your safety, check weight before handling:						
0-5kg Light 5-15kg Normal 15+kg Heavy						
MATERIAL LIST FOR PART - x33				2 PARTS REQUIRED		
POS. No.	PROFILE	No.	GRADE	L (mm)	AREA (m ²)	WEIGHT (kg)
x33	D30	1	S355J2	5864	0.5	31.1 !!
TOTAL WEIGHT FOR				2	PARTS	62.1

Execution class: EXC 2		* o 3 0 4 8 0 - 1 *  DS <i>Skalkonstruktion</i> * W x 3 3 *			
No utilization on drawings = over 50%					
V-SEAM Utilization under 50% EXC 2=> Acc. to process control EXC 3=> 20% UT Utilization over 50% EXC 2=> 10% UT EXC 3=> 20% UT		PROJECT	Akkasæter Lager- og vedlikeholdshall		PHASE 1 / Phase 1
		MEMBER	Vind-X		QUANTITY: 2 PROJECT No 30480-1
		REVISION		ISSUED: 03.11.2025	DRAFTER: ZLL BIM control: SST DRAWING No. x.33
Part list	Qty.				
VX	2				