


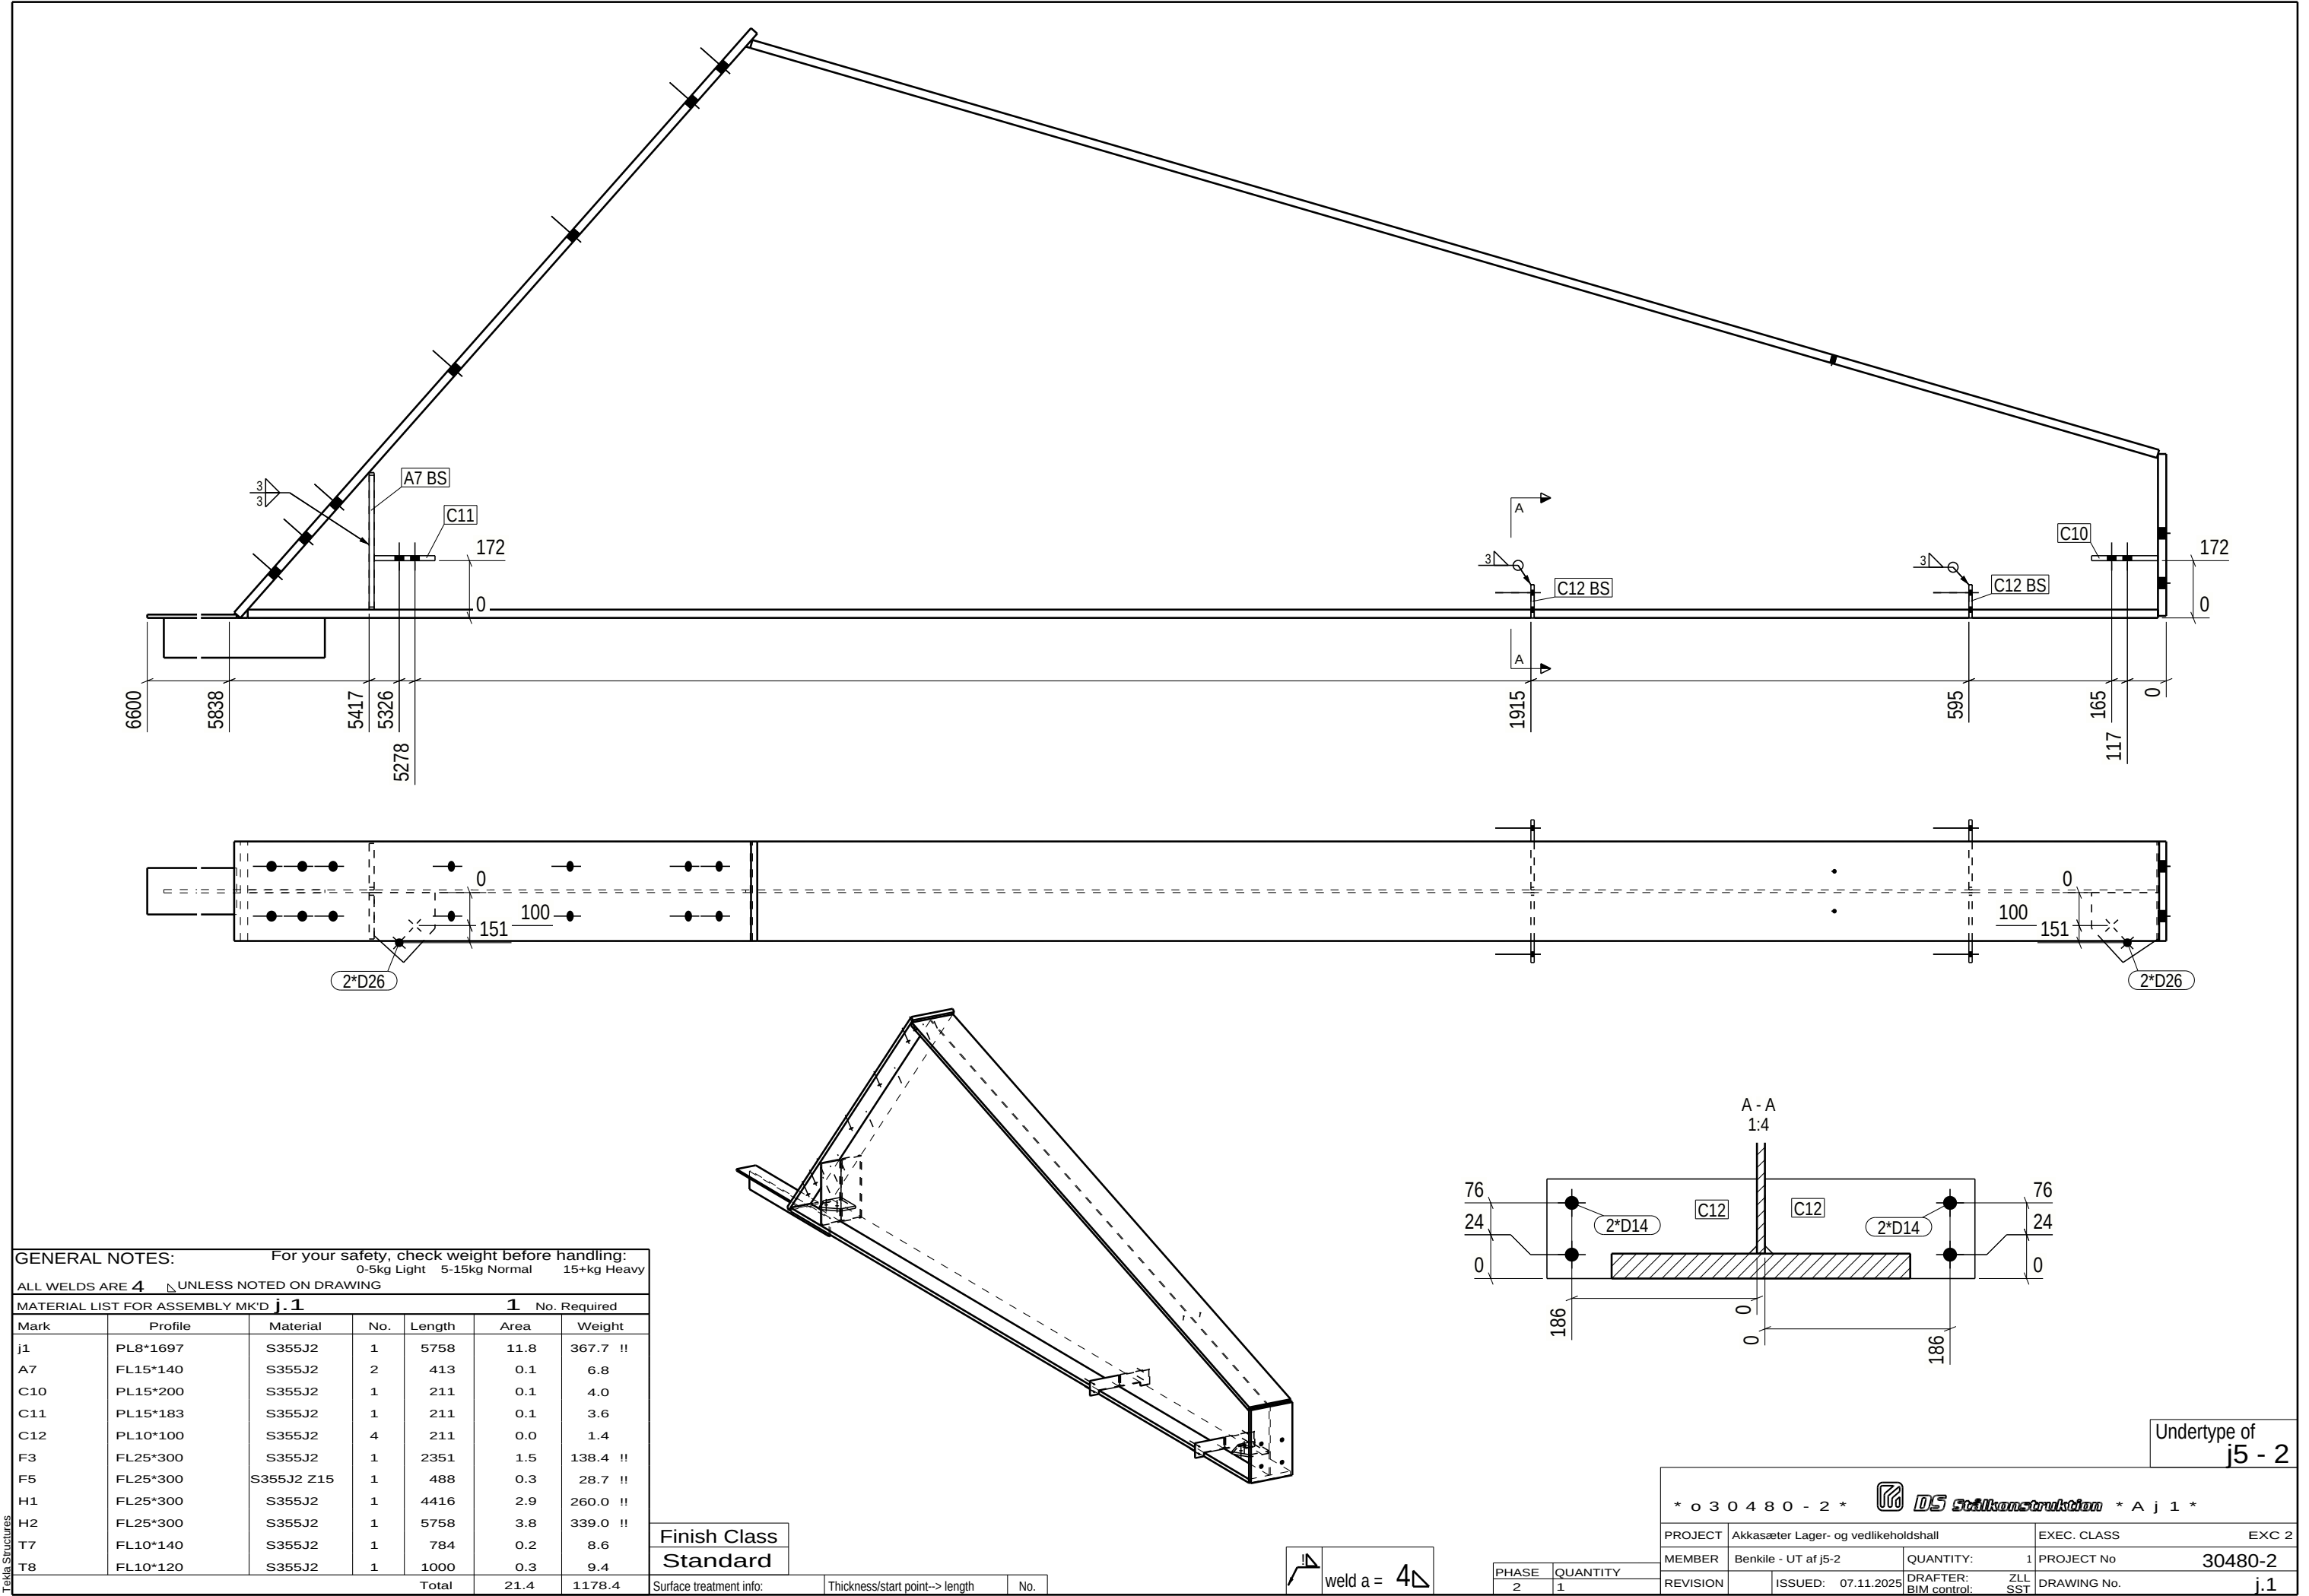

GENERAL NOTES: For your safety, check weight before handling:  
0-5kg Light 5-15kg Normal 15+kg Heavy

| MATERIAL LIST FOR ASSEMBLY MK'D j.1 |          |            |     |        |      | 1 No. Required |
|-------------------------------------|----------|------------|-----|--------|------|----------------|
| Mark                                | Profile  | Material   | No. | Length | Area | Weight         |
| j1                                  | PL8*1697 | S355J2     | 1   | 5758   | 11.8 | 367.7 !!       |
| A7                                  | FL15*140 | S355J2     | 2   | 413    | 0.1  | 6.8            |
| C10                                 | PL15*200 | S355J2     | 1   | 211    | 0.1  | 4.0            |
| C11                                 | PL15*183 | S355J2     | 1   | 211    | 0.1  | 3.6            |
| C12                                 | PL10*100 | S355J2     | 4   | 211    | 0.0  | 1.4            |
| F3                                  | FL25*300 | S355J2     | 1   | 2351   | 1.5  | 138.4 !!       |
| F5                                  | FL25*300 | S355J2 Z15 | 1   | 488    | 0.3  | 28.7 !!        |
| H1                                  | FL25*300 | S355J2     | 1   | 4416   | 2.9  | 260.0 !!       |
| H2                                  | FL25*300 | S355J2     | 1   | 5758   | 3.8  | 339.0 !!       |
| T7                                  | FL10*140 | S355J2     | 1   | 784    | 0.2  | 8.6            |
| T8                                  | FL10*120 | S355J2     | 1   | 1000   | 0.3  | 9.4            |
| Total                               |          |            |     |        | 21.4 | 1178.4         |

Finish Class  
Standard

Surface treatment info: Thickness/start point-> length No.

weld a = 4

| PHASE | QUANTITY |
|-------|----------|
| 2     | 1        |

|                                                   |                                      |              |                      |
|---------------------------------------------------|--------------------------------------|--------------|----------------------|
| * o 3 0 4 8 0 - 2 * DS Skalkonstruktion * A j 1 * |                                      |              |                      |
| PROJECT                                           | Akkasæter Lager- og vedlikeholdshall | EXEC. CLASS  | EXC 2                |
| MEMBER                                            | Benkile - UT af j5-2                 | QUANTITY:    | 1 PROJECT No 30480-2 |
| REVISION                                          | ISSUED: 07.11.2025                   | DRAFTER: ZLL | DRAWING No. j.1      |
| BIM control: SST                                  |                                      |              |                      |