
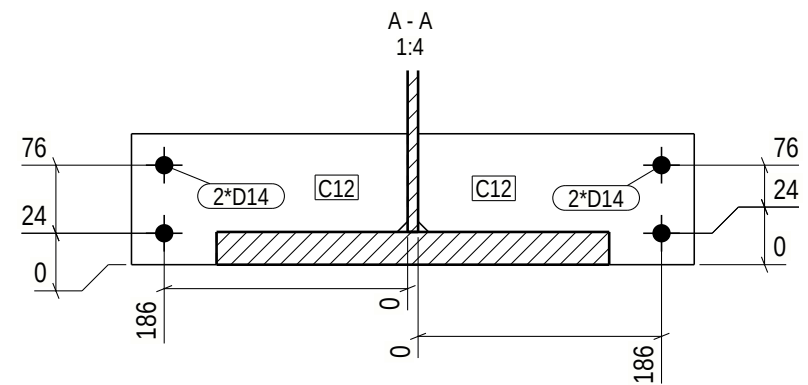
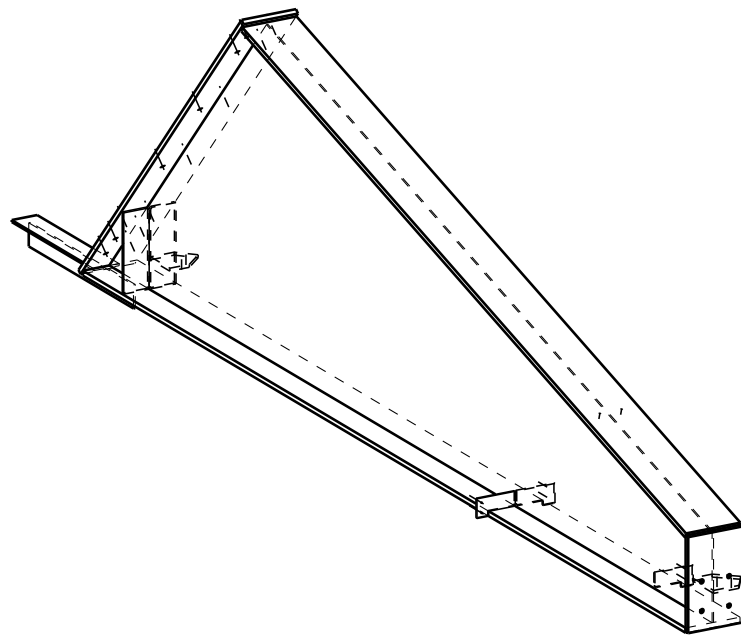


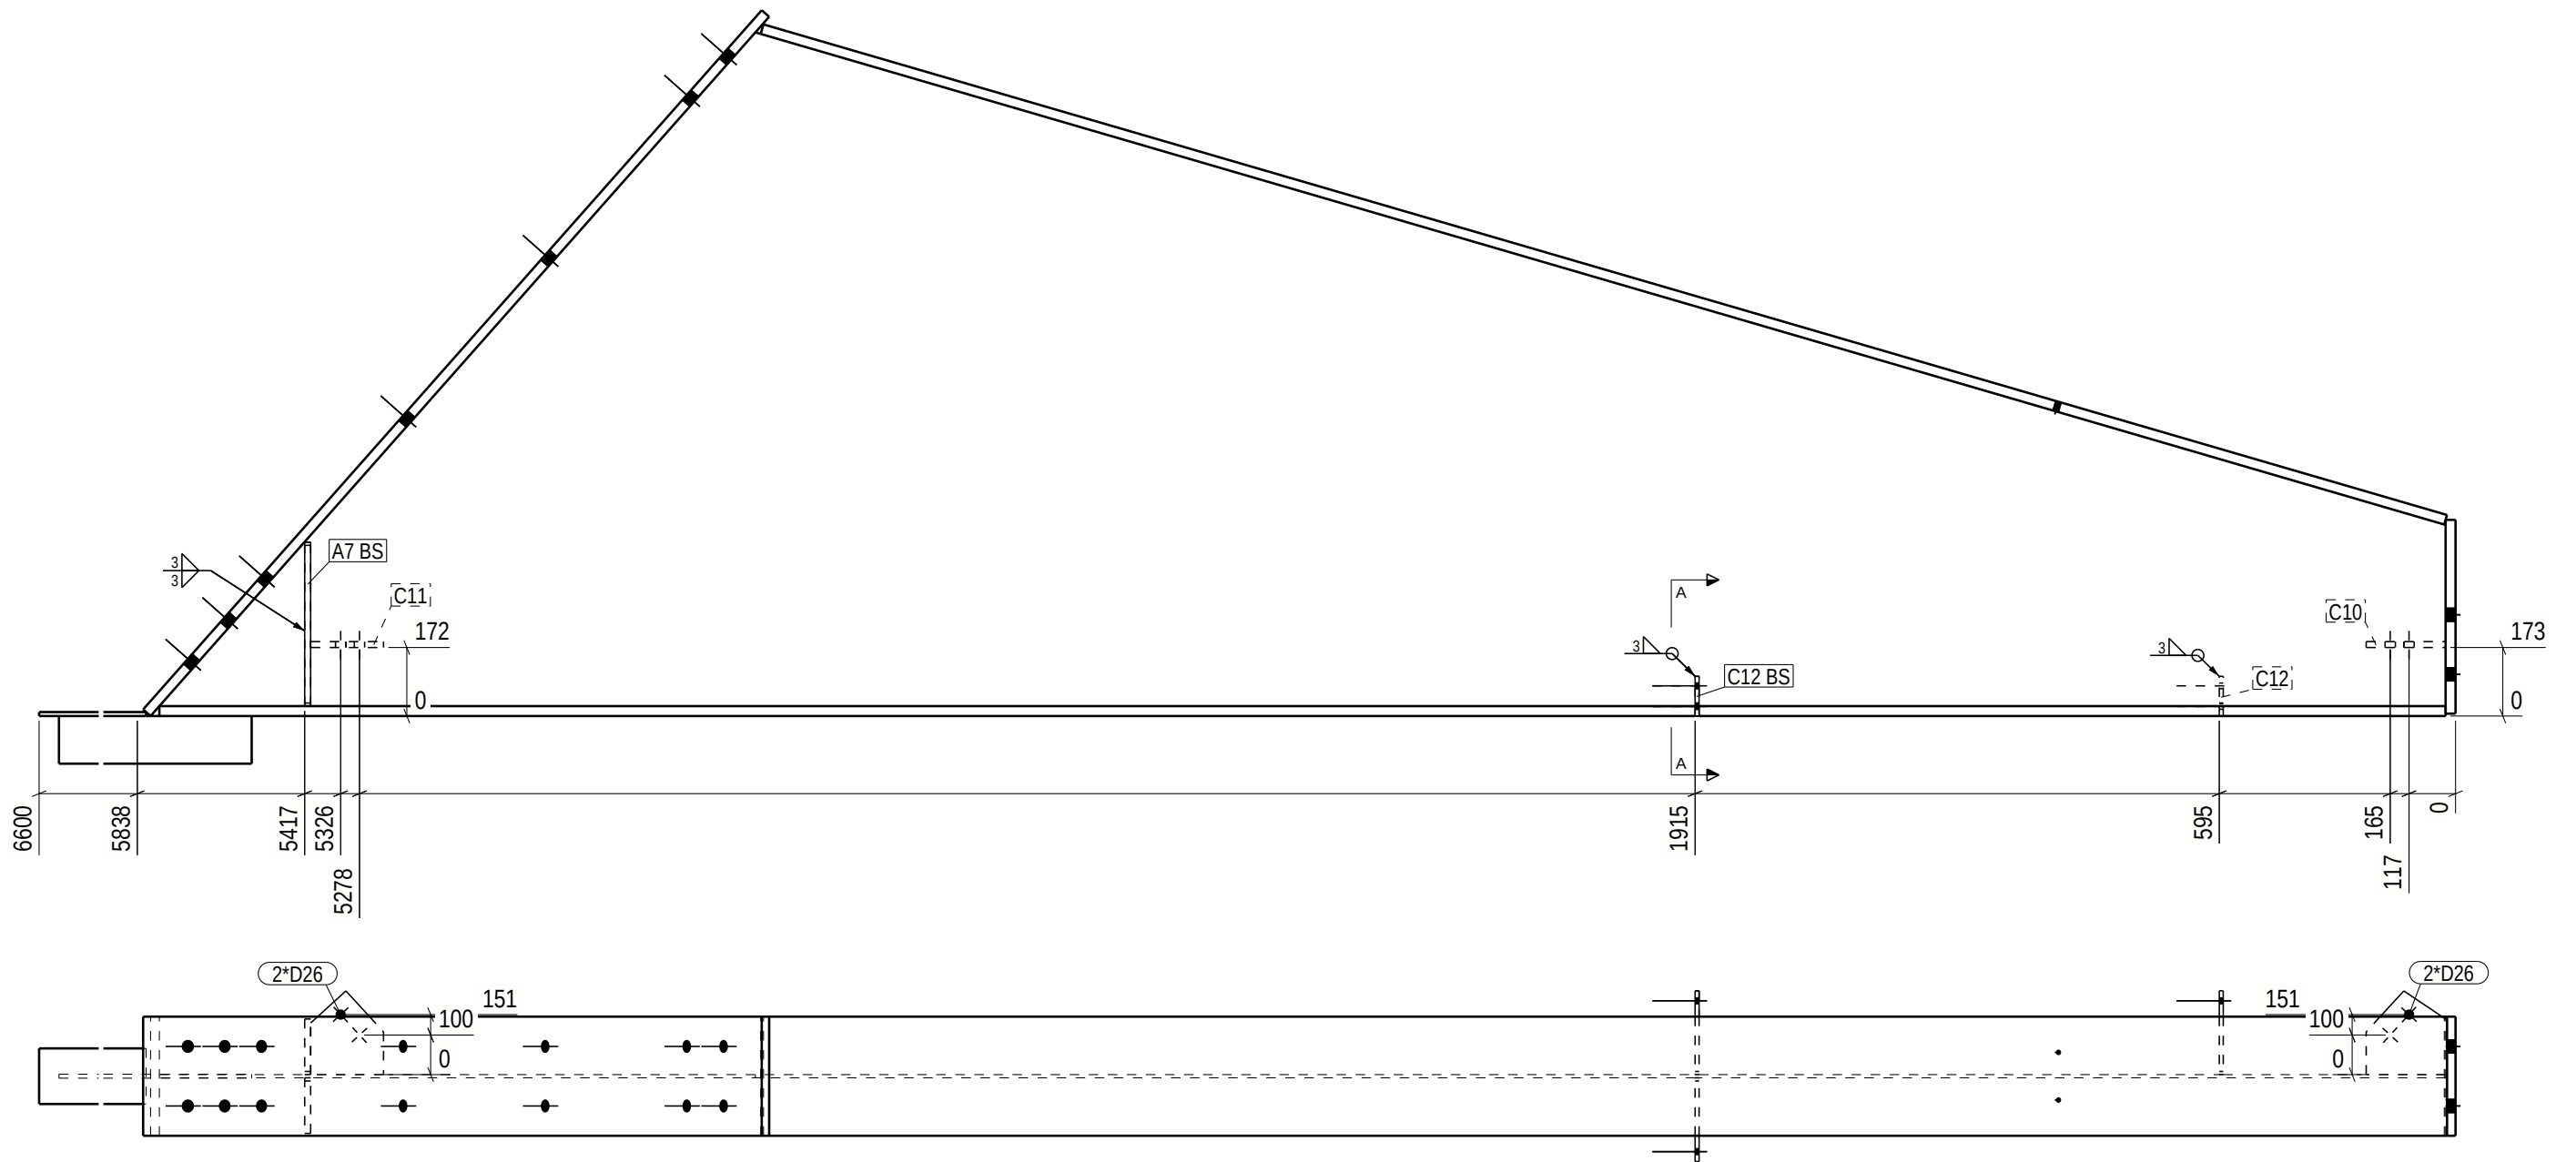

GENERAL NOTES: For your safety, check weight before handling:						
ALL WELDS ARE 4 UNLESS NOTED ON DRAWING						
MATERIAL LIST FOR ASSEMBLY MK'D j.2						
Mark	Profile	Material	No.	Length	Area	Weight
j2	PL8*1697	S355J2	1	5758	11.8	367.7 !!
A7	FL15*140	S355J2	2	413	0.1	6.8
C10	PL15*200	S355J2	1	211	0.1	4.0
C11	PL15*183	S355J2	1	211	0.1	3.6
C12	PL10*100	S355J2	3	211	0.0	1.4
F3	FL25*300	S355J2	1	2351	1.5	138.4 !!
F5	FL25*300	S355J2 Z15	1	488	0.3	28.7 !!
H1	FL25*300	S355J2	1	4416	2.9	260.0 !!
H2	FL25*300	S355J2	1	5758	3.8	339.0 !!
T7	FL10*140	S355J2	1	784	0.2	8.6
T8	FL10*120	S355J2	1	1000	0.3	9.4
Total				21.4	1177.0	

Finish Class
Standard

Surface treatment info:	Thickness/start point-> length	No.
-------------------------	--------------------------------	-----

weld a = 4

PHASE	QUANTITY
2	1

					Undertype af j5 - 2	
* o 3 0 4 8 0 - 2 *  DS Skalkonstruktion * A j 2 *						
PROJECT	Akkasæter Lager- og vedlikeholdshall				EXEC. CLASS	EXC 2
MEMBER	Benkile - UT af j5-2		QUANTITY:	1	PROJECT No	30480-2
REVISION		ISSUED: 07.11.2025	DRAFTER: BIM control:	ZLL SST	DRAWING No.	j.2

Undertype of
j5 - 2