


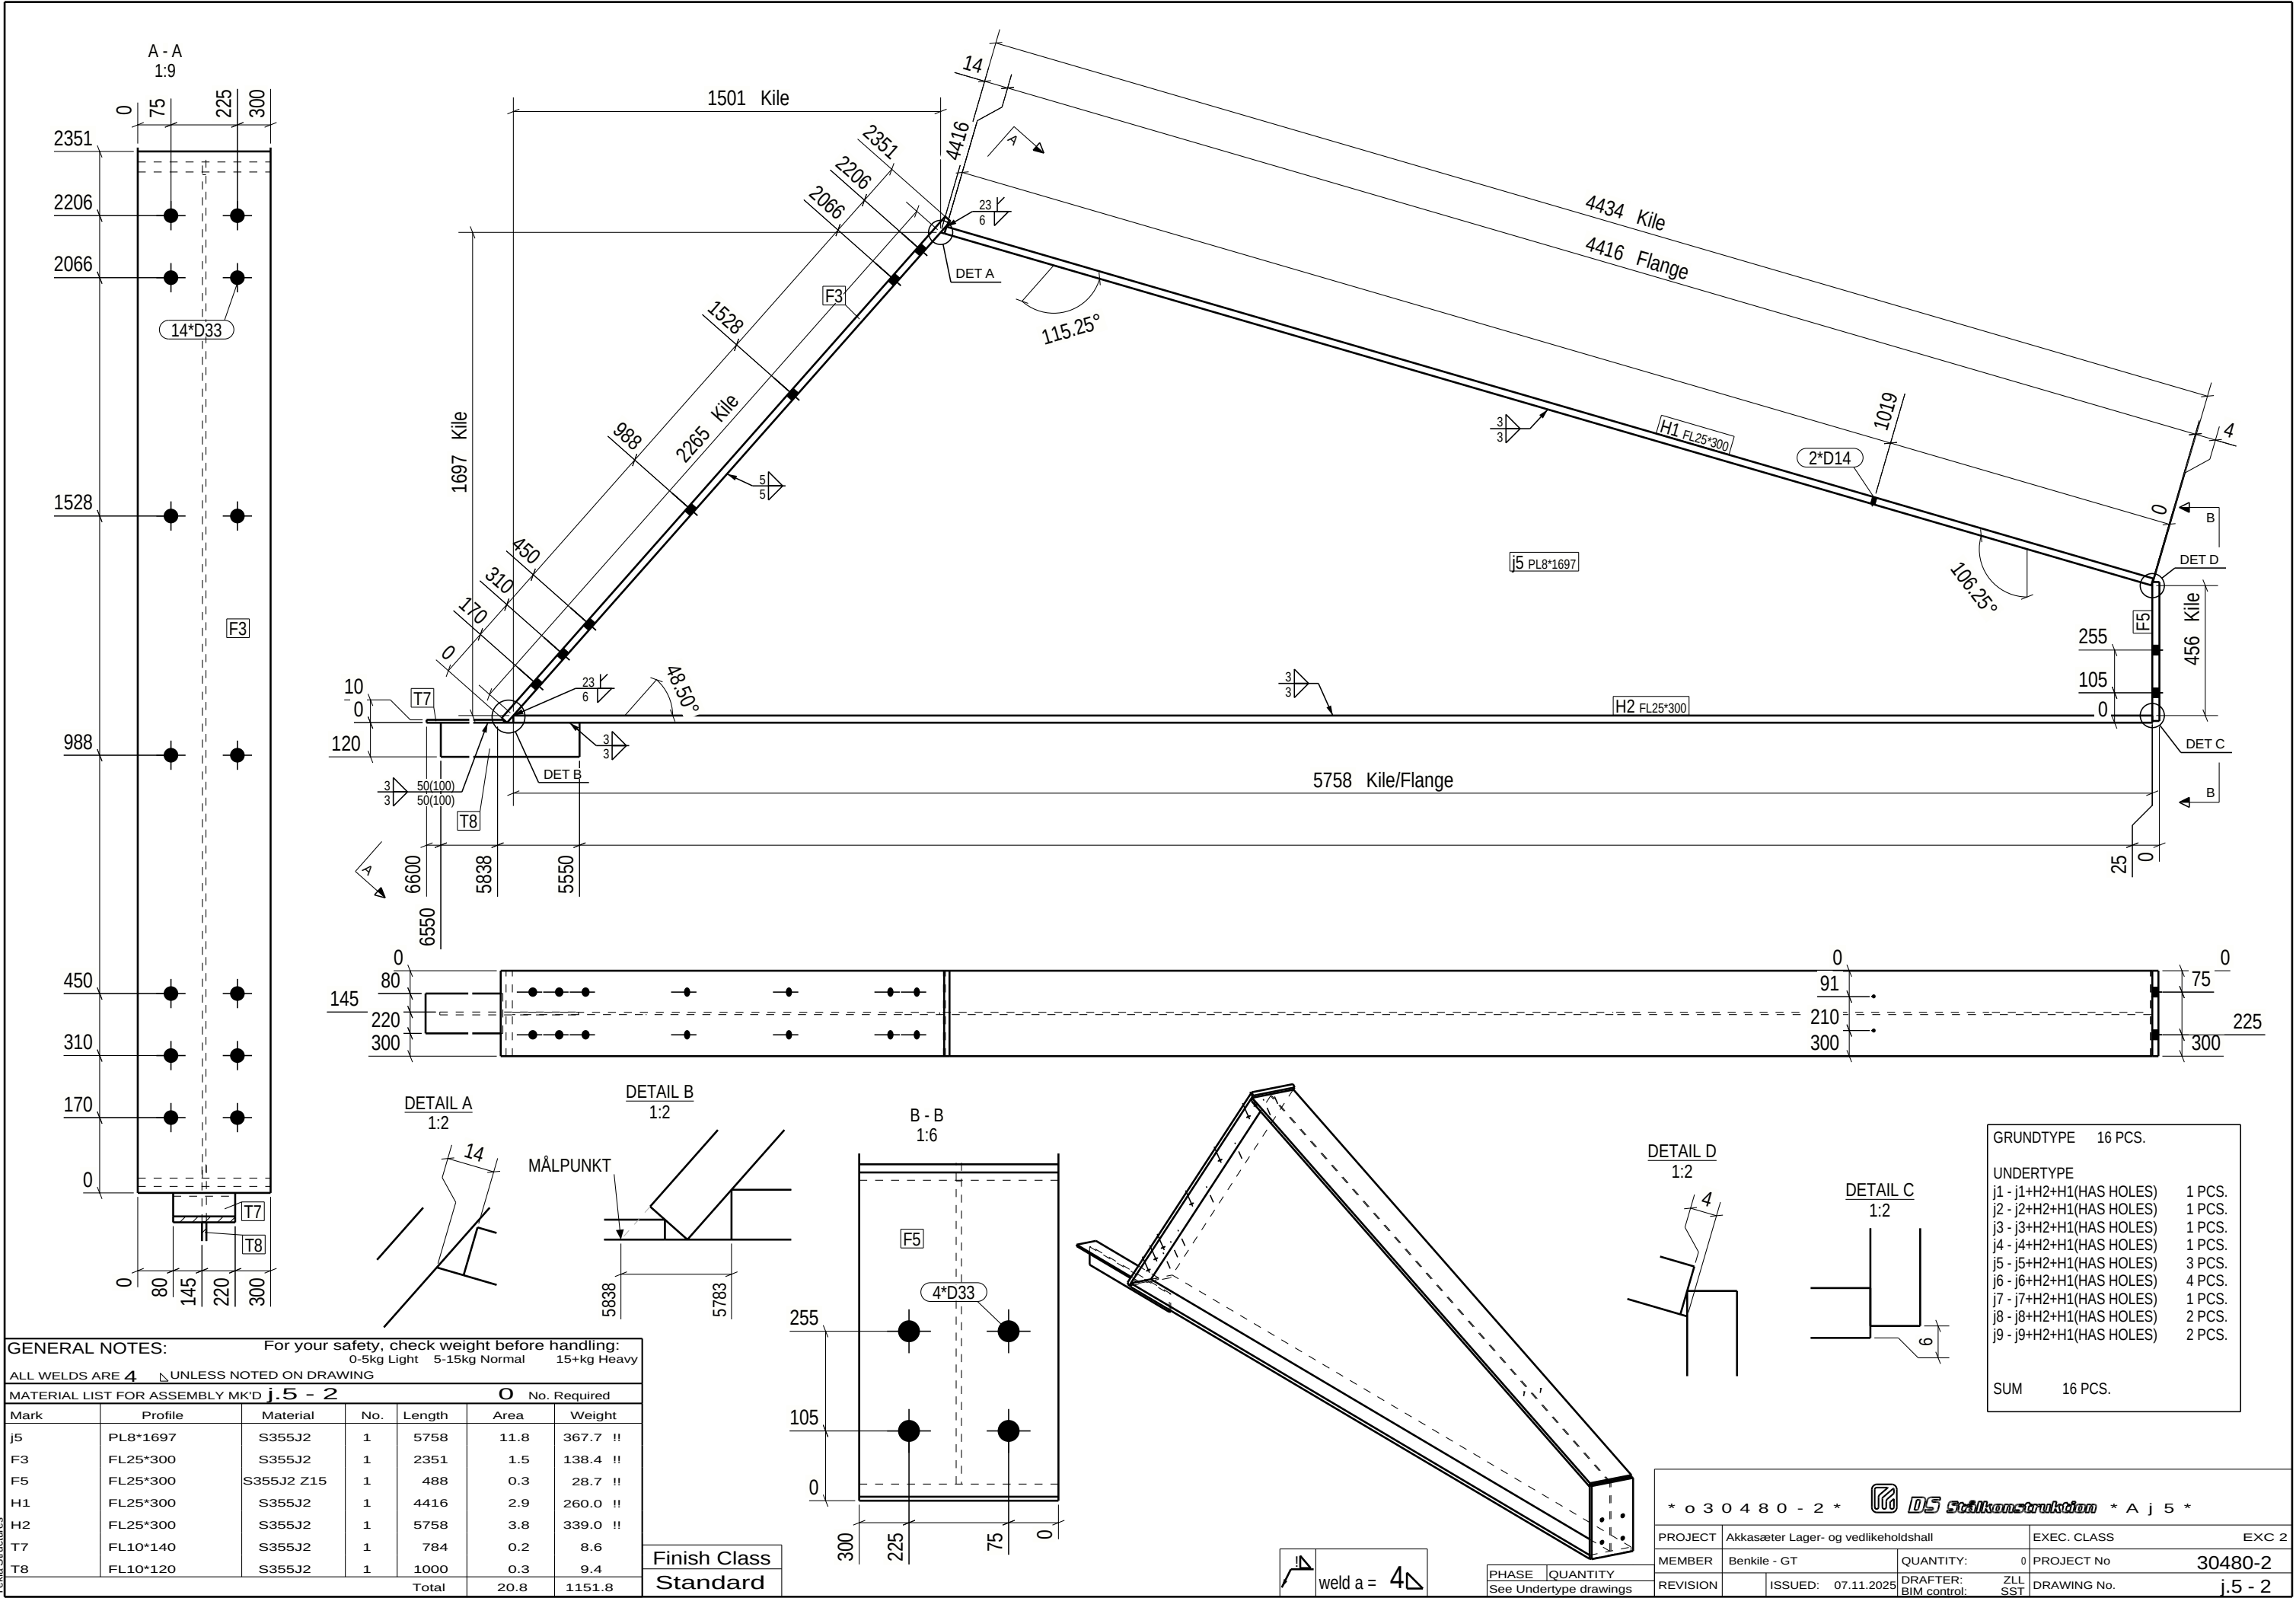

GENERAL NOTES: For your safety, check weight before handling:
0-5kg Light 5-15kg Normal 15+kg Heavy

ALL WELDS ARE 4 UNLESS NOTED ON DRAWING

MATERIAL LIST FOR ASSEMBLY MK'D j.5 - 2

Mark	Profile	Material	No.	Length	Area	Weight
j5	PL8*1697	S355J2	1	5758	11.8	367.7 !!
F3	FL25*300	S355J2	1	2351	1.5	138.4 !!
F5	FL25*300	S355J2 Z15	1	488	0.3	28.7 !!
H1	FL25*300	S355J2	1	4416	2.9	260.0 !!
H2	FL25*300	S355J2	1	5758	3.8	339.0 !!
T7	FL10*140	S355J2	1	784	0.2	8.6
T8	FL10*120	S355J2	1	1000	0.3	9.4
Total				20.8	1151.8	

Finish Class
Standard

GRUNDTYPE	16 PCS.
UNDERTYPE	
j1 - j1+H2+H1(HAS HOLES)	1 PCS.
j2 - j2+H2+H1(HAS HOLES)	1 PCS.
j3 - j3+H2+H1(HAS HOLES)	1 PCS.
j4 - j4+H2+H1(HAS HOLES)	1 PCS.
j5 - j5+H2+H1(HAS HOLES)	3 PCS.
j6 - j6+H2+H1(HAS HOLES)	4 PCS.
j7 - j7+H2+H1(HAS HOLES)	1 PCS.
j8 - j8+H2+H1(HAS HOLES)	2 PCS.
j9 - j9+H2+H1(HAS HOLES)	2 PCS.
SUM	16 PCS.

* o 3 0 4 8 0 - 2 * DS Skalkonstruktion * A j 5 *

PROJECT	Akkasæter Lager- og vedlikeholdshall	EXEC. CLASS	EXC 2
MEMBER	Benkile - GT	QUANTITY:	0
REVISION	ISSUED: 07.11.2025	DRAFTER:	ZLL SST
PROJECT No		30480-2	
DRAWING No.		j.5 - 2	

weld a = 4

PHASE QUANTITY
See Undertype drawings