
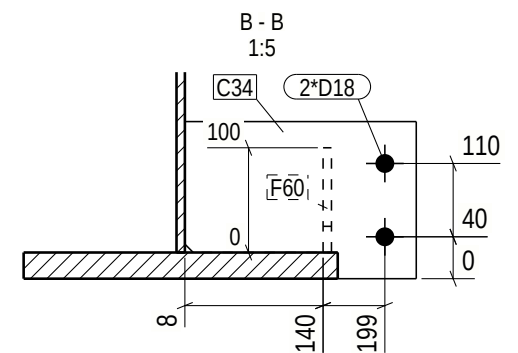
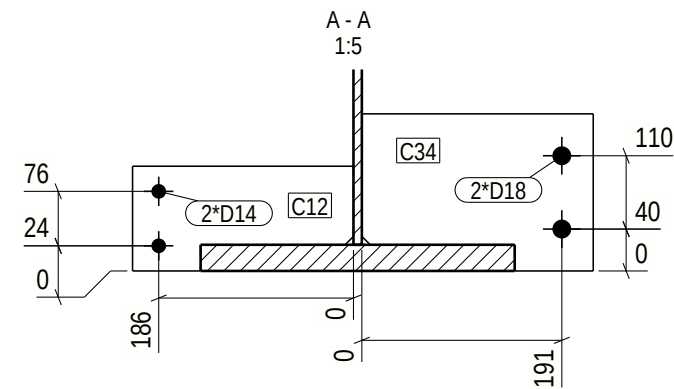
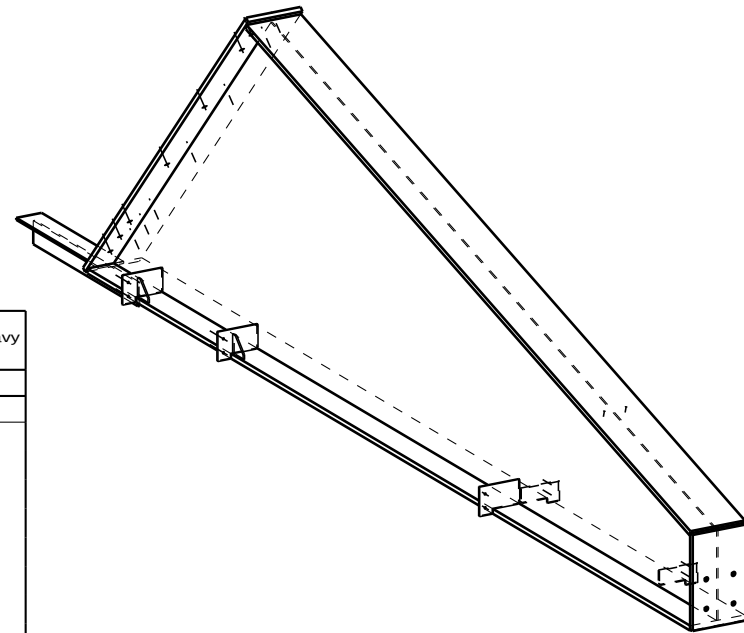


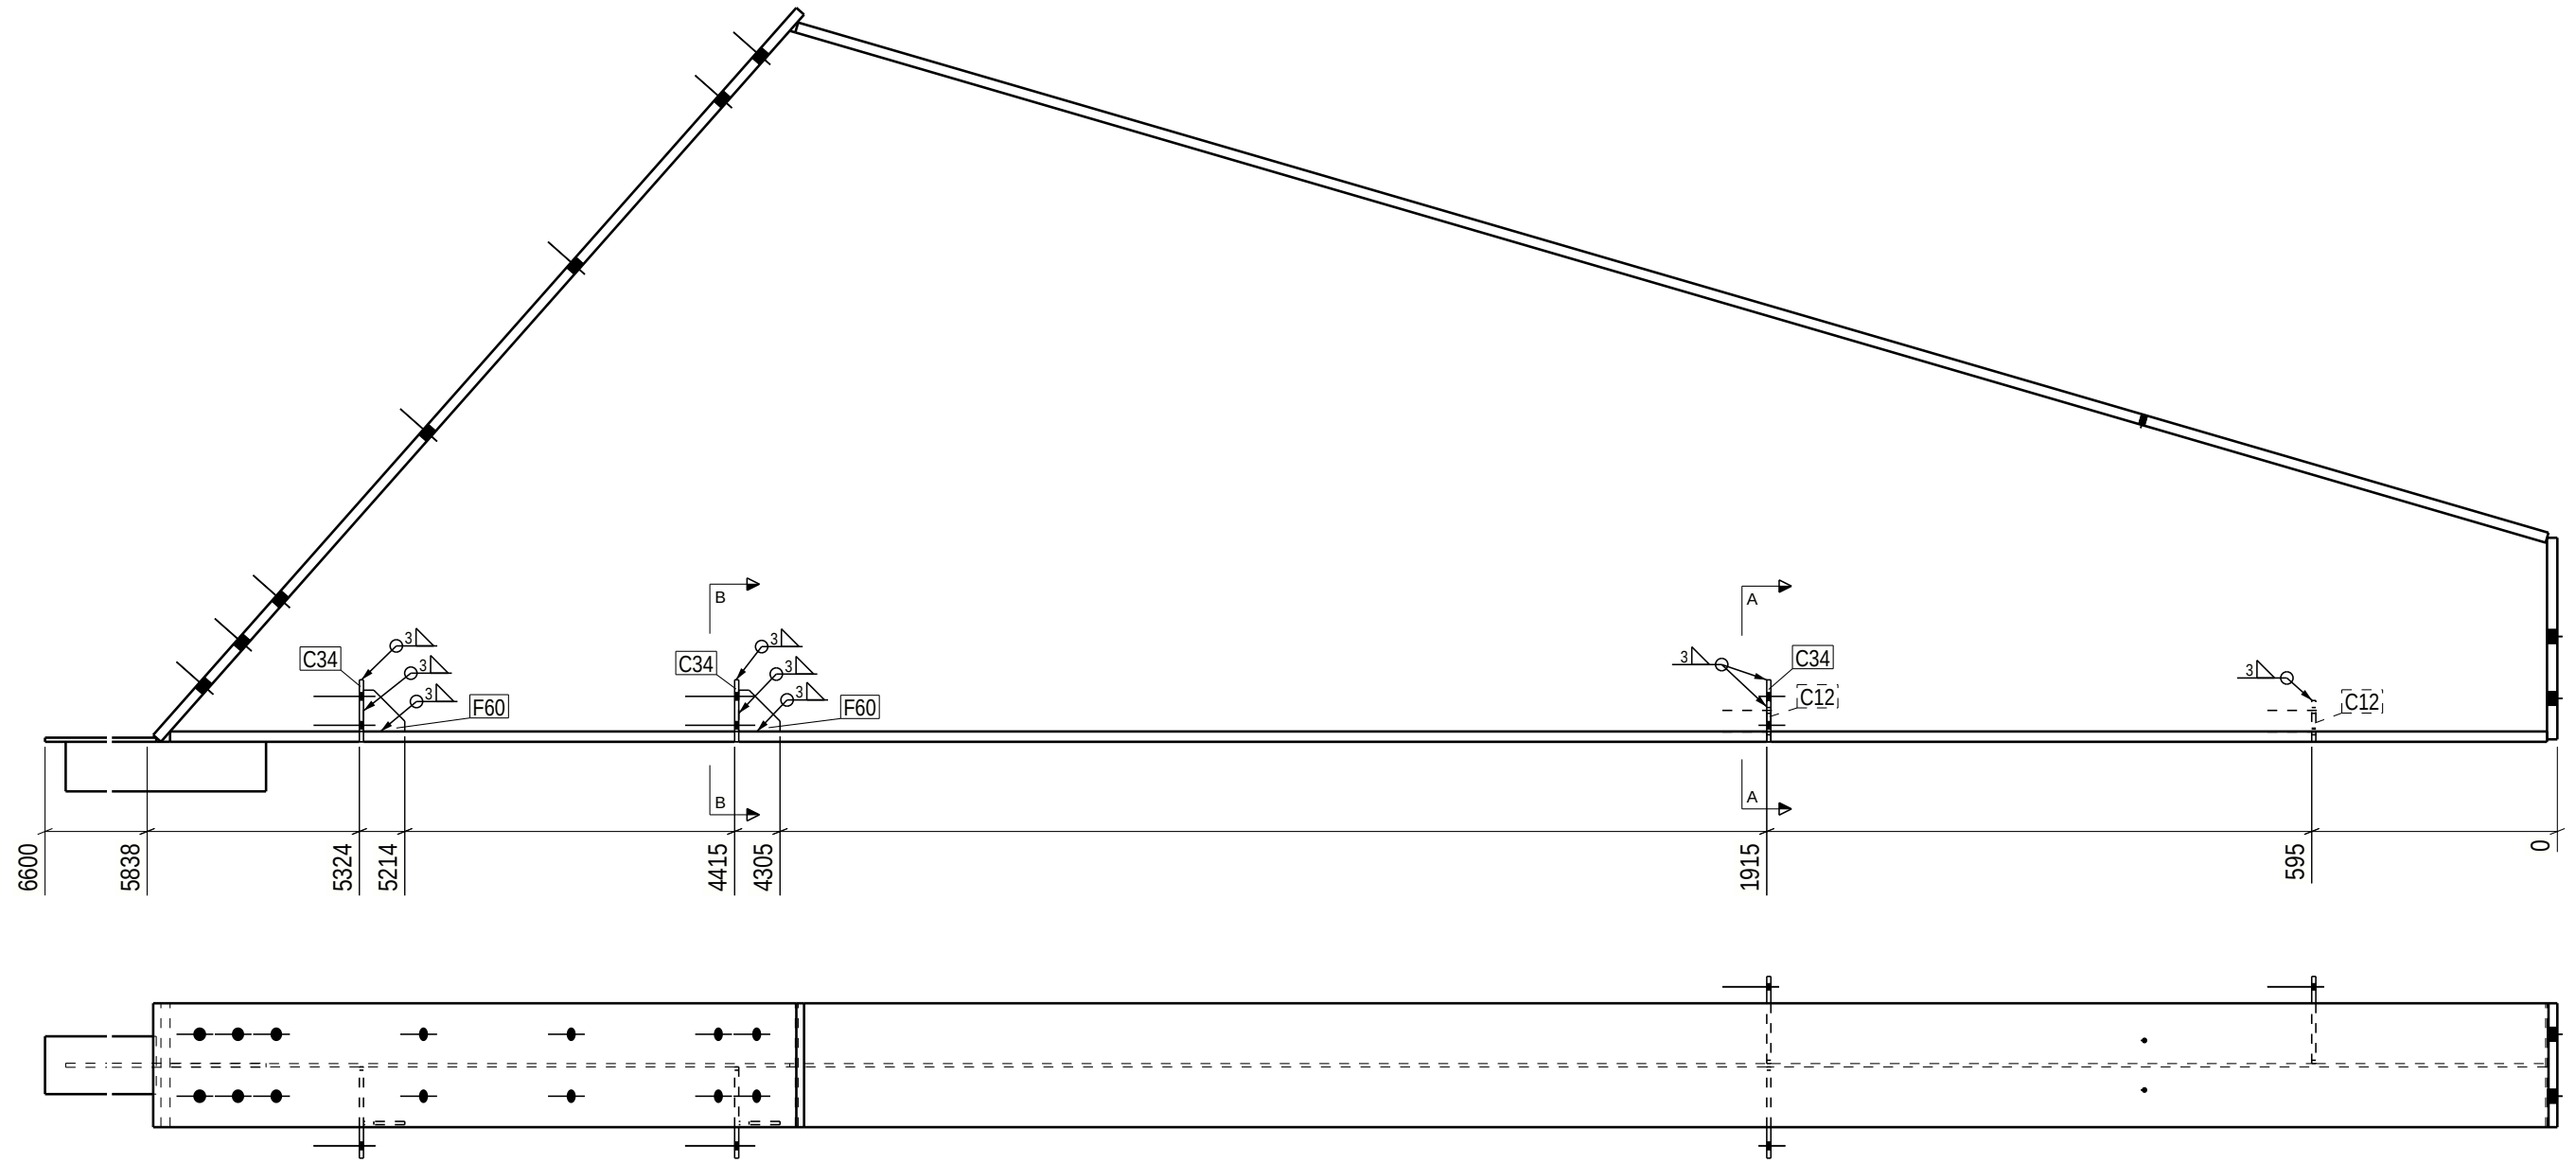

GENERAL NOTES: For your safety, check weight before handling:
0-5kg Light 5-15kg Normal 15+kg Heavy

ALL WELDS ARE 4 UNLESS NOTED ON DRAWING

MATERIAL LIST FOR ASSEMBLY MK'D **j.5** **3** No. Required

Mark	Profile	Material	No.	Length	Area	Weight
j5	PL8*1697	S355J2	1	5758	11.8	367.7 !!
C12	PL10*100	S355J2	2	211	0.0	1.4
C34	PL10*150	S355J2	3	221	0.1	2.3
F3	FL25*300	S355J2	1	2351	1.5	138.4 !!
F5	FL25*300	S355J2 Z15	1	488	0.3	28.7 !!
F60	FL8*100	S355J2	2	100	0.0	0.5
H1	FL25*300	S355J2	1	4416	2.9	260.0 !!
H2	FL25*300	S355J2	1	5758	3.8	339.0 !!
T7	FL10*140	S355J2	1	784	0.2	8.6
T8	FL10*120	S355J2	1	1000	0.3	9.4
Total				21.1	1162.4	

Finish Class
Standard

Surface treatment info: Thickness/start point-> length No.

weld a = 4

PHASE	QUANTITY
2	3

* o 3 0 4 8 0 - 2 *  DS <i>Stalkonstruktion</i> * A j 5 *			
PROJECT	Akkasæter Lager- og vedlikeholdshall	EXEC. CLASS	EXC 2
MEMBER	Benkile - UT af j5-2	QUANTITY:	3 PROJECT No 30480-2
REVISION	ISSUED: 07.11.2025	DRAFTER: ZLL	DRAWING No. j.5
	BIM control: SST		

Undertype of
j5 - 2