
 
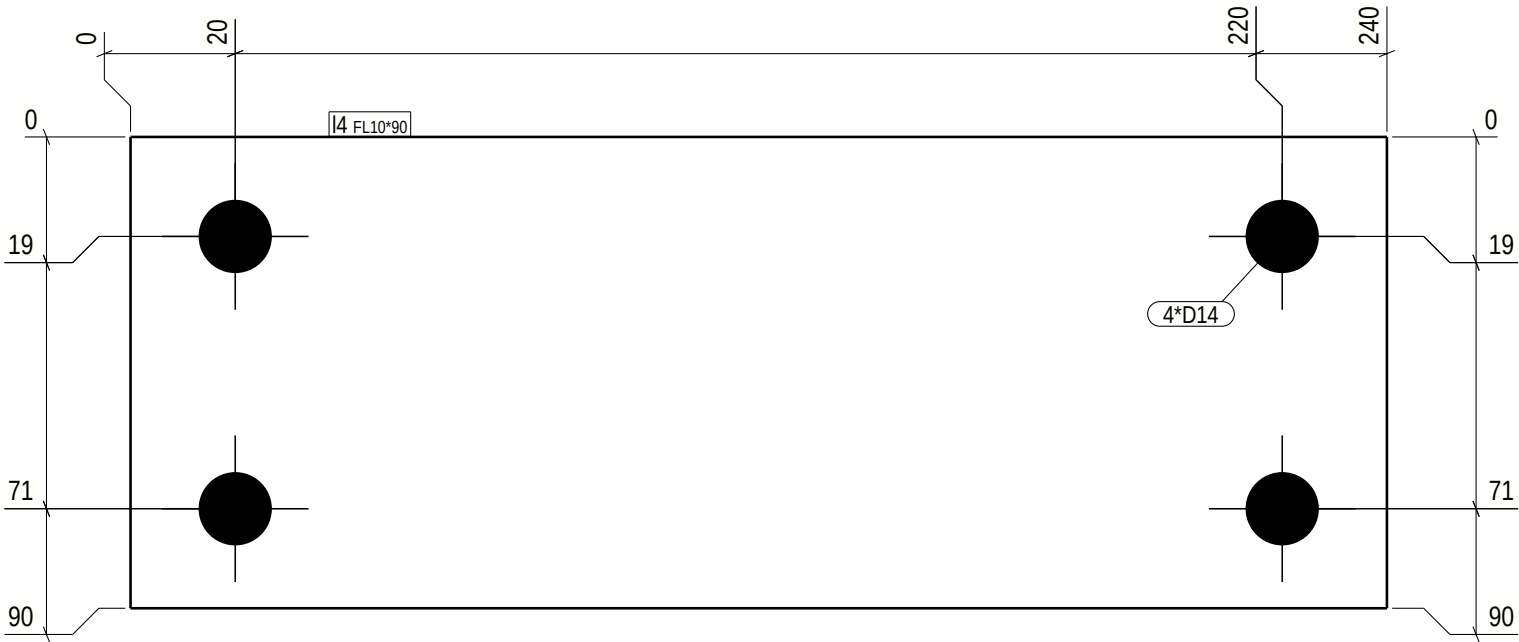


Tekla Structures

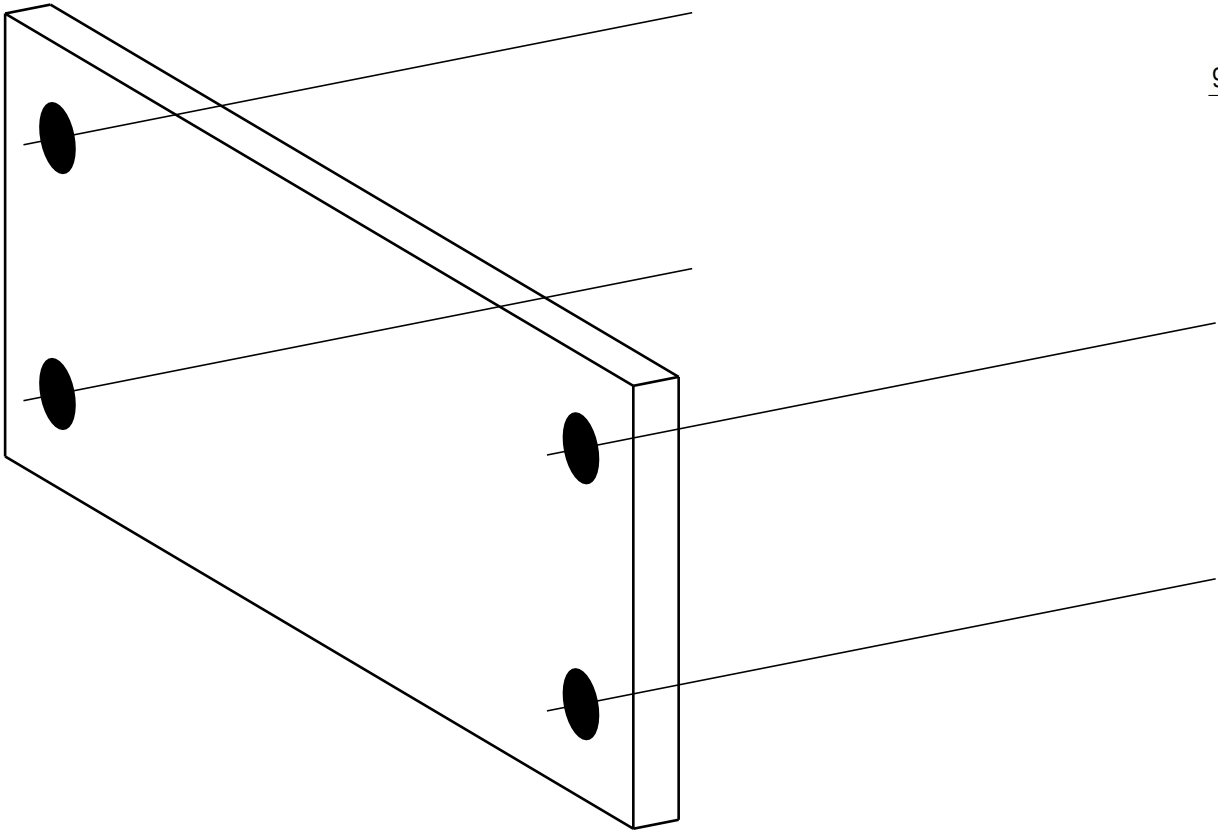

GENERAL NOTES: For your safety, check weight before handling:
0-5kg Light 5-15kg Normal 15+kg Heavy

ALL WELDS ARE 4 UNLESS NOTED ON DRAWING

MATERIAL LIST FOR ASSEMBLY MK'D I.4						
2 No. Required						
Mark	Profile	Material	No.	Length	Area	Weight
I4	FL10*90	S355J2	1	240	0.0	1.7
Total				0.0	1.7	

Finish Class
Standard

Surface treatment info:	Thickness/start point-> length	No.
-------------------------	--------------------------------	-----

weld a = 4

PHASE	QUANTITY
2	2

* o 3 0 4 8 0 - 2 * DS Steelkonstruktion * A I 4 *					
PROJECT	Akkasæter Lager- og vedlikeholdshall			EXEC. CLASS	EXC 2
MEMBER	Løsdele	QUANTITY:	2	PROJECT No	30480-2
REVISION		ISSUED:	07.11.2025	DRAFTER: ZLL	DRAWING No. I.4
		BIM control:	SST		

Loose part
no welding