
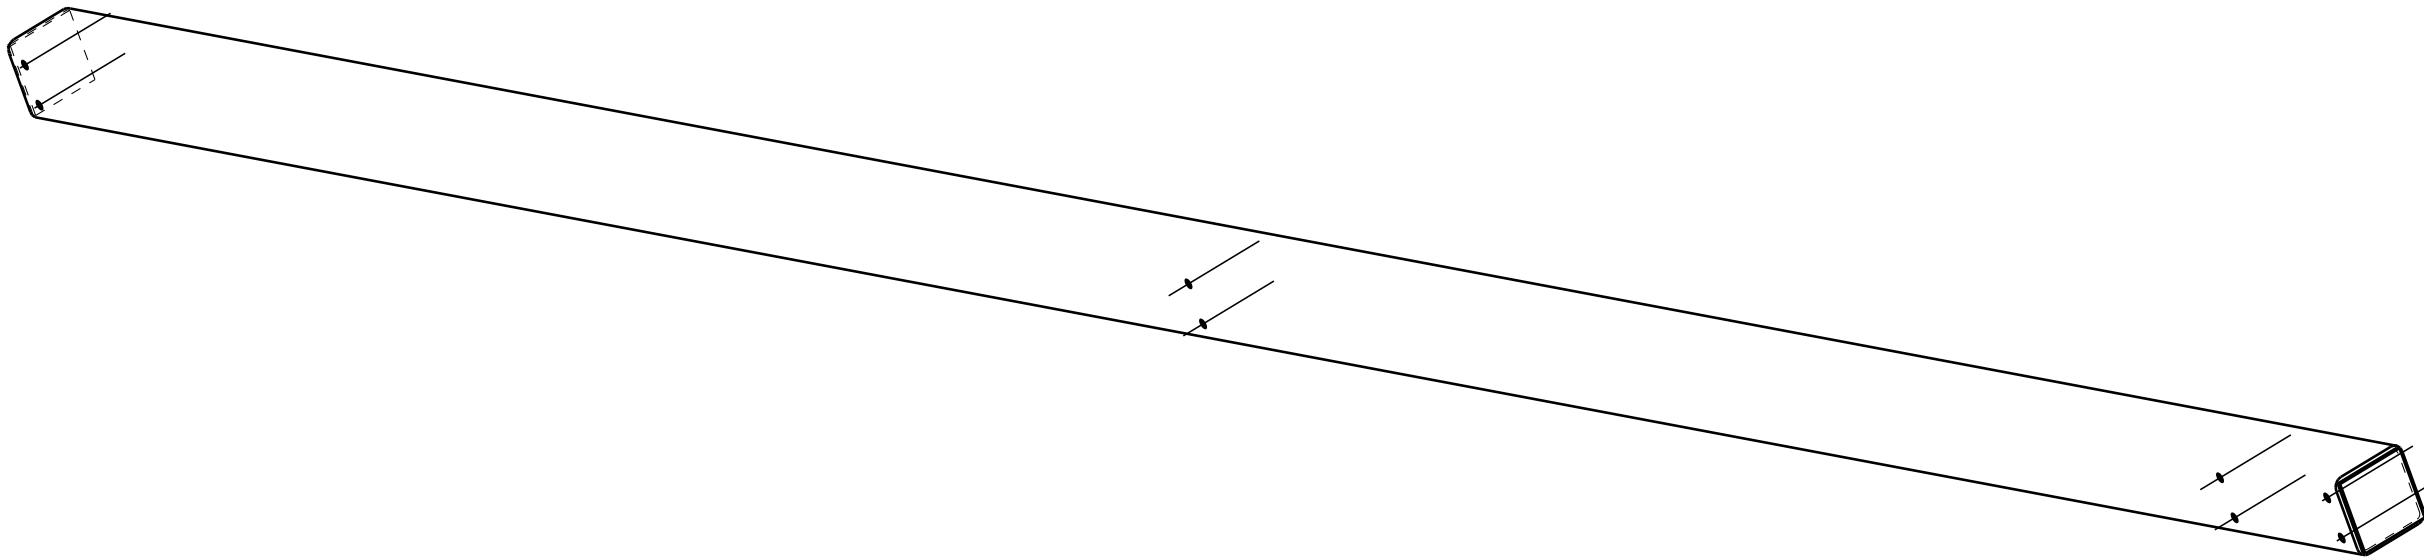
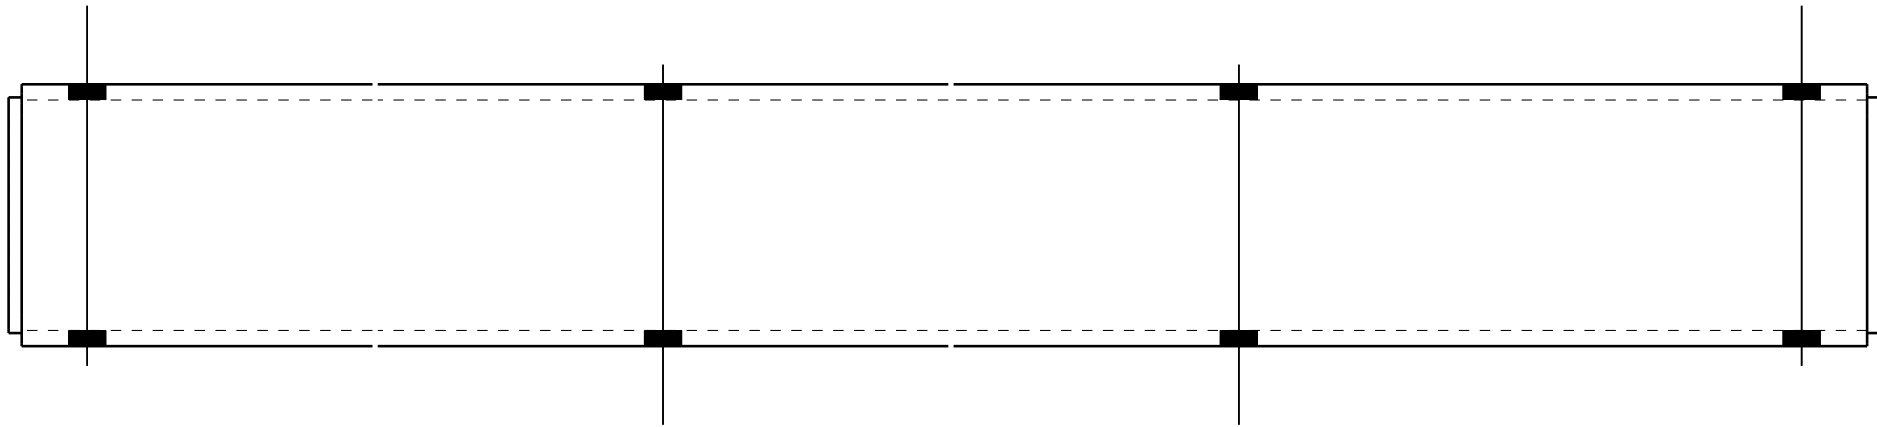


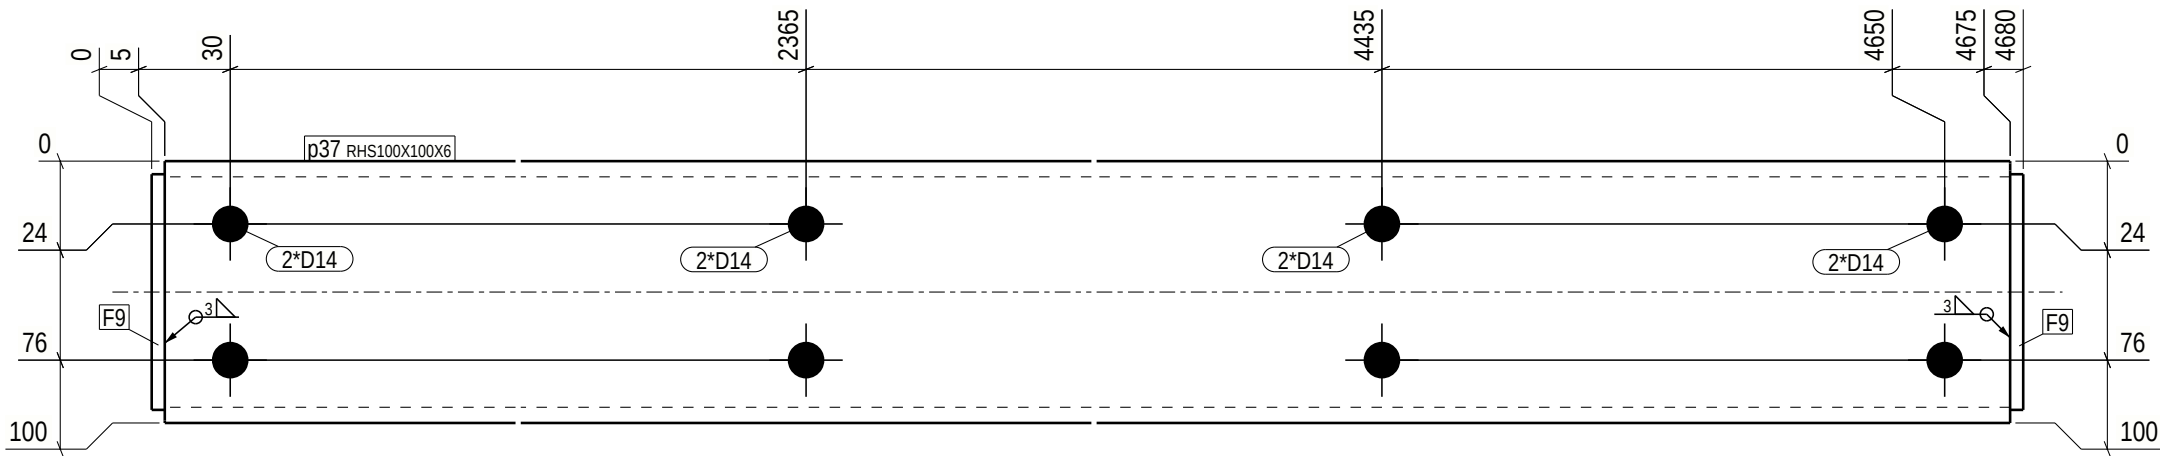

GENERAL NOTES: For your safety, check weight before handling:
0-5kg Light 5-15kg Normal 15+kg Heavy

ALL WELDS ARE 4 UNLESS NOTED ON DRAWING

MATERIAL LIST FOR ASSEMBLY MK'D **p.37** **8** No. Required

Mark	Profile	Material	No.	Length	Area	Weight
p37	RHS100X100X6	S355J2H	1	4670	1.8	79.0 !!
F9	FL5*90	S355J2	2	90	0.0	0.3
Total					1.8	79.6

Finish Class
Standard

Surface treatment info:	Thickness/start point--> length	No.
-------------------------	---------------------------------	-----

weld a = 4

PHASE	QUANTITY
2	8

* o 3 0 4 8 0 - 2 *  DS <i>Stålkonstruktion</i> * A p 3 7 *			
PROJECT	Akkasæter Lager- og vedlikeholdshall	EXEC. CLASS	EXC 2
MEMBER	Portomfatning	QUANTITY:	8 PROJECT No 30480-2
REVISION	ISSUED: 07.11.2025	DRAFTER: ZLL BIM control: SST	DRAWING No. p.37