
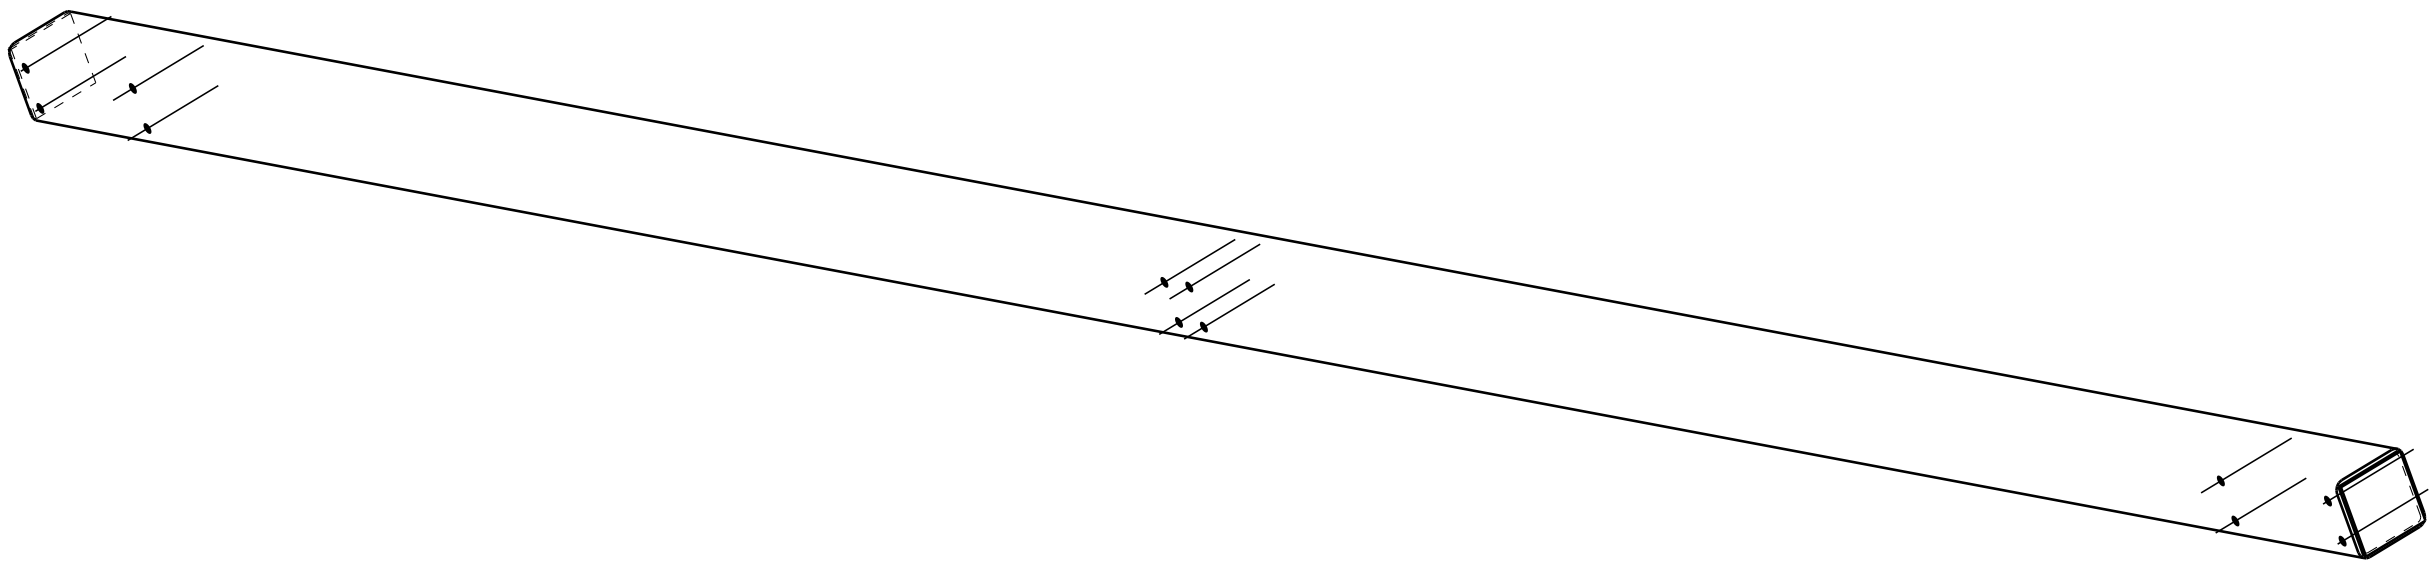
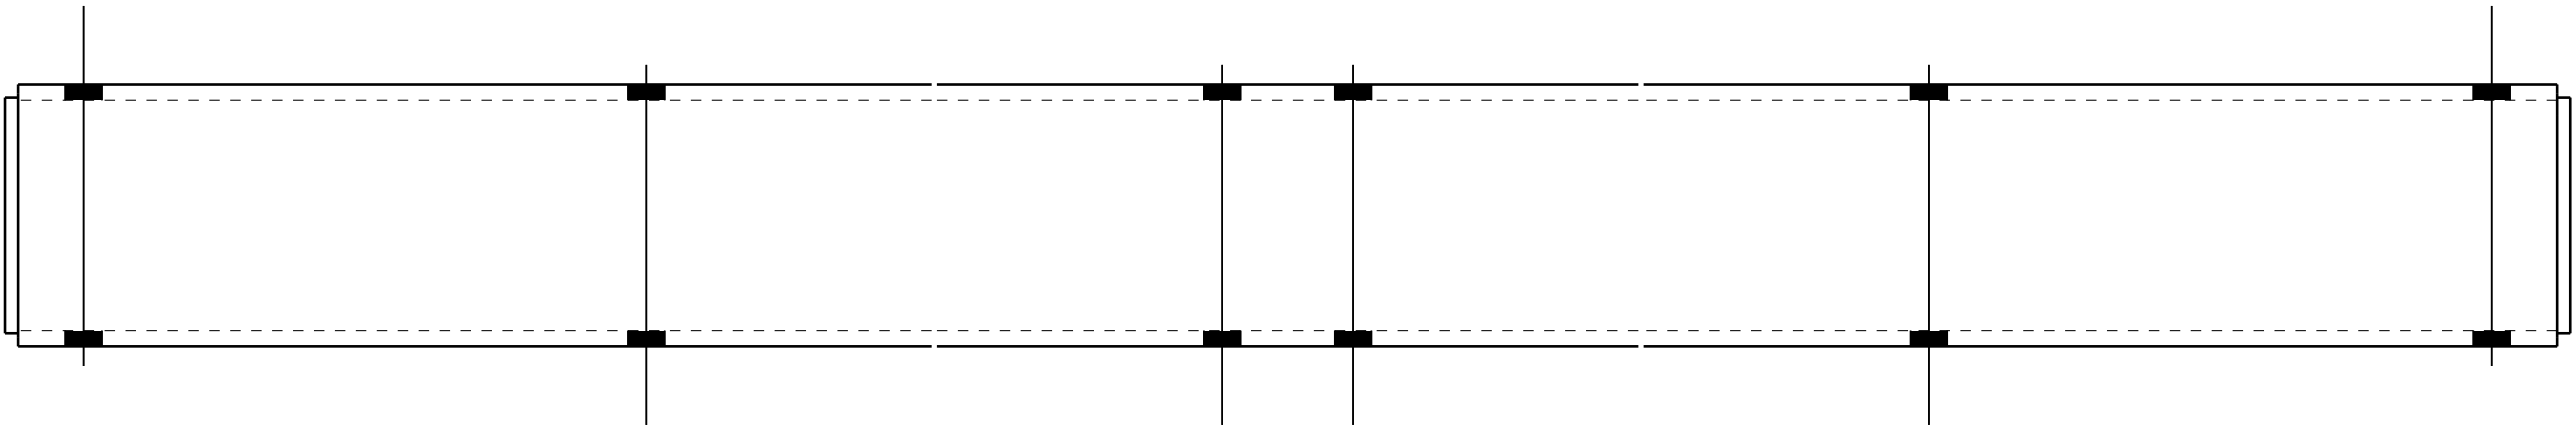


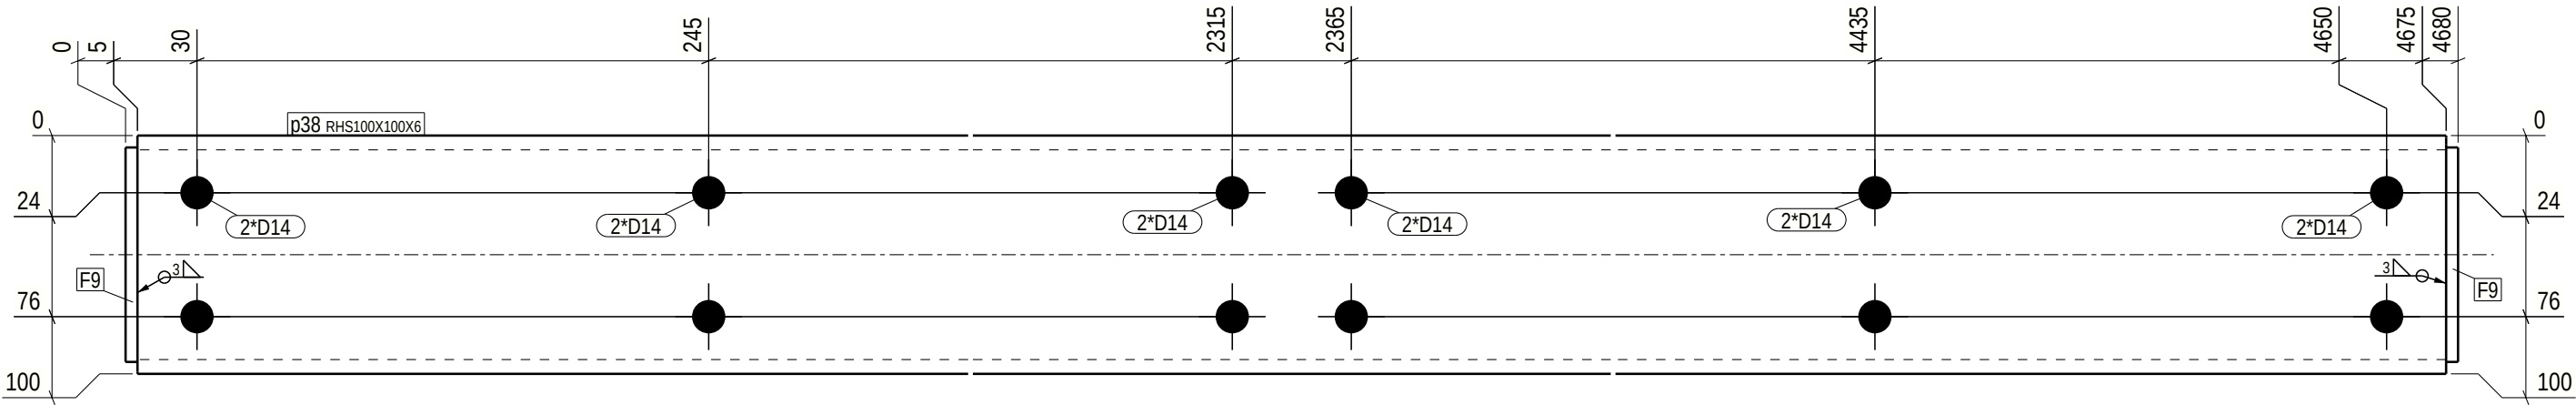

GENERAL NOTES:

For your safety, check weight before handling:

0-5kg Light 5-15kg Normal 15+kg Heavy

ALL WELDS ARE 4 UNLESS NOTED ON DRAWING

MATERIAL LIST FOR ASSEMBLY MK'D

p.38

2 No. Required

Mark	Profile	Material	No.	Length	Area	Weight
p38	RHS100X100X6	S355J2H	1	4670	1.8	79.0 !!
F9	FL5*90	S355J2	2	90	0.0	0.3
Total					1.8	79.6

Finish Class
Standard

Surface treatment info:	Thickness/start point--> length	No.
-------------------------	---------------------------------	-----

weld a = 4

PHASE	QUANTITY
2	2

* o 3 0 4 8 0 - 2 *  DS <i>Stalkonstruktion</i> * A p 3 8 *			
PROJECT	Akkasæter Lager- og vedlikeholdshall	EXEC. CLASS	EXC 2
MEMBER	Portomfatning	QUANTITY:	2
REVISION		ISSUED:	07.11.2025
		DRAFTER:	ZLL
		BIM control:	SST
		PROJECT No	30480-2
		DRAWING No.	p.38