


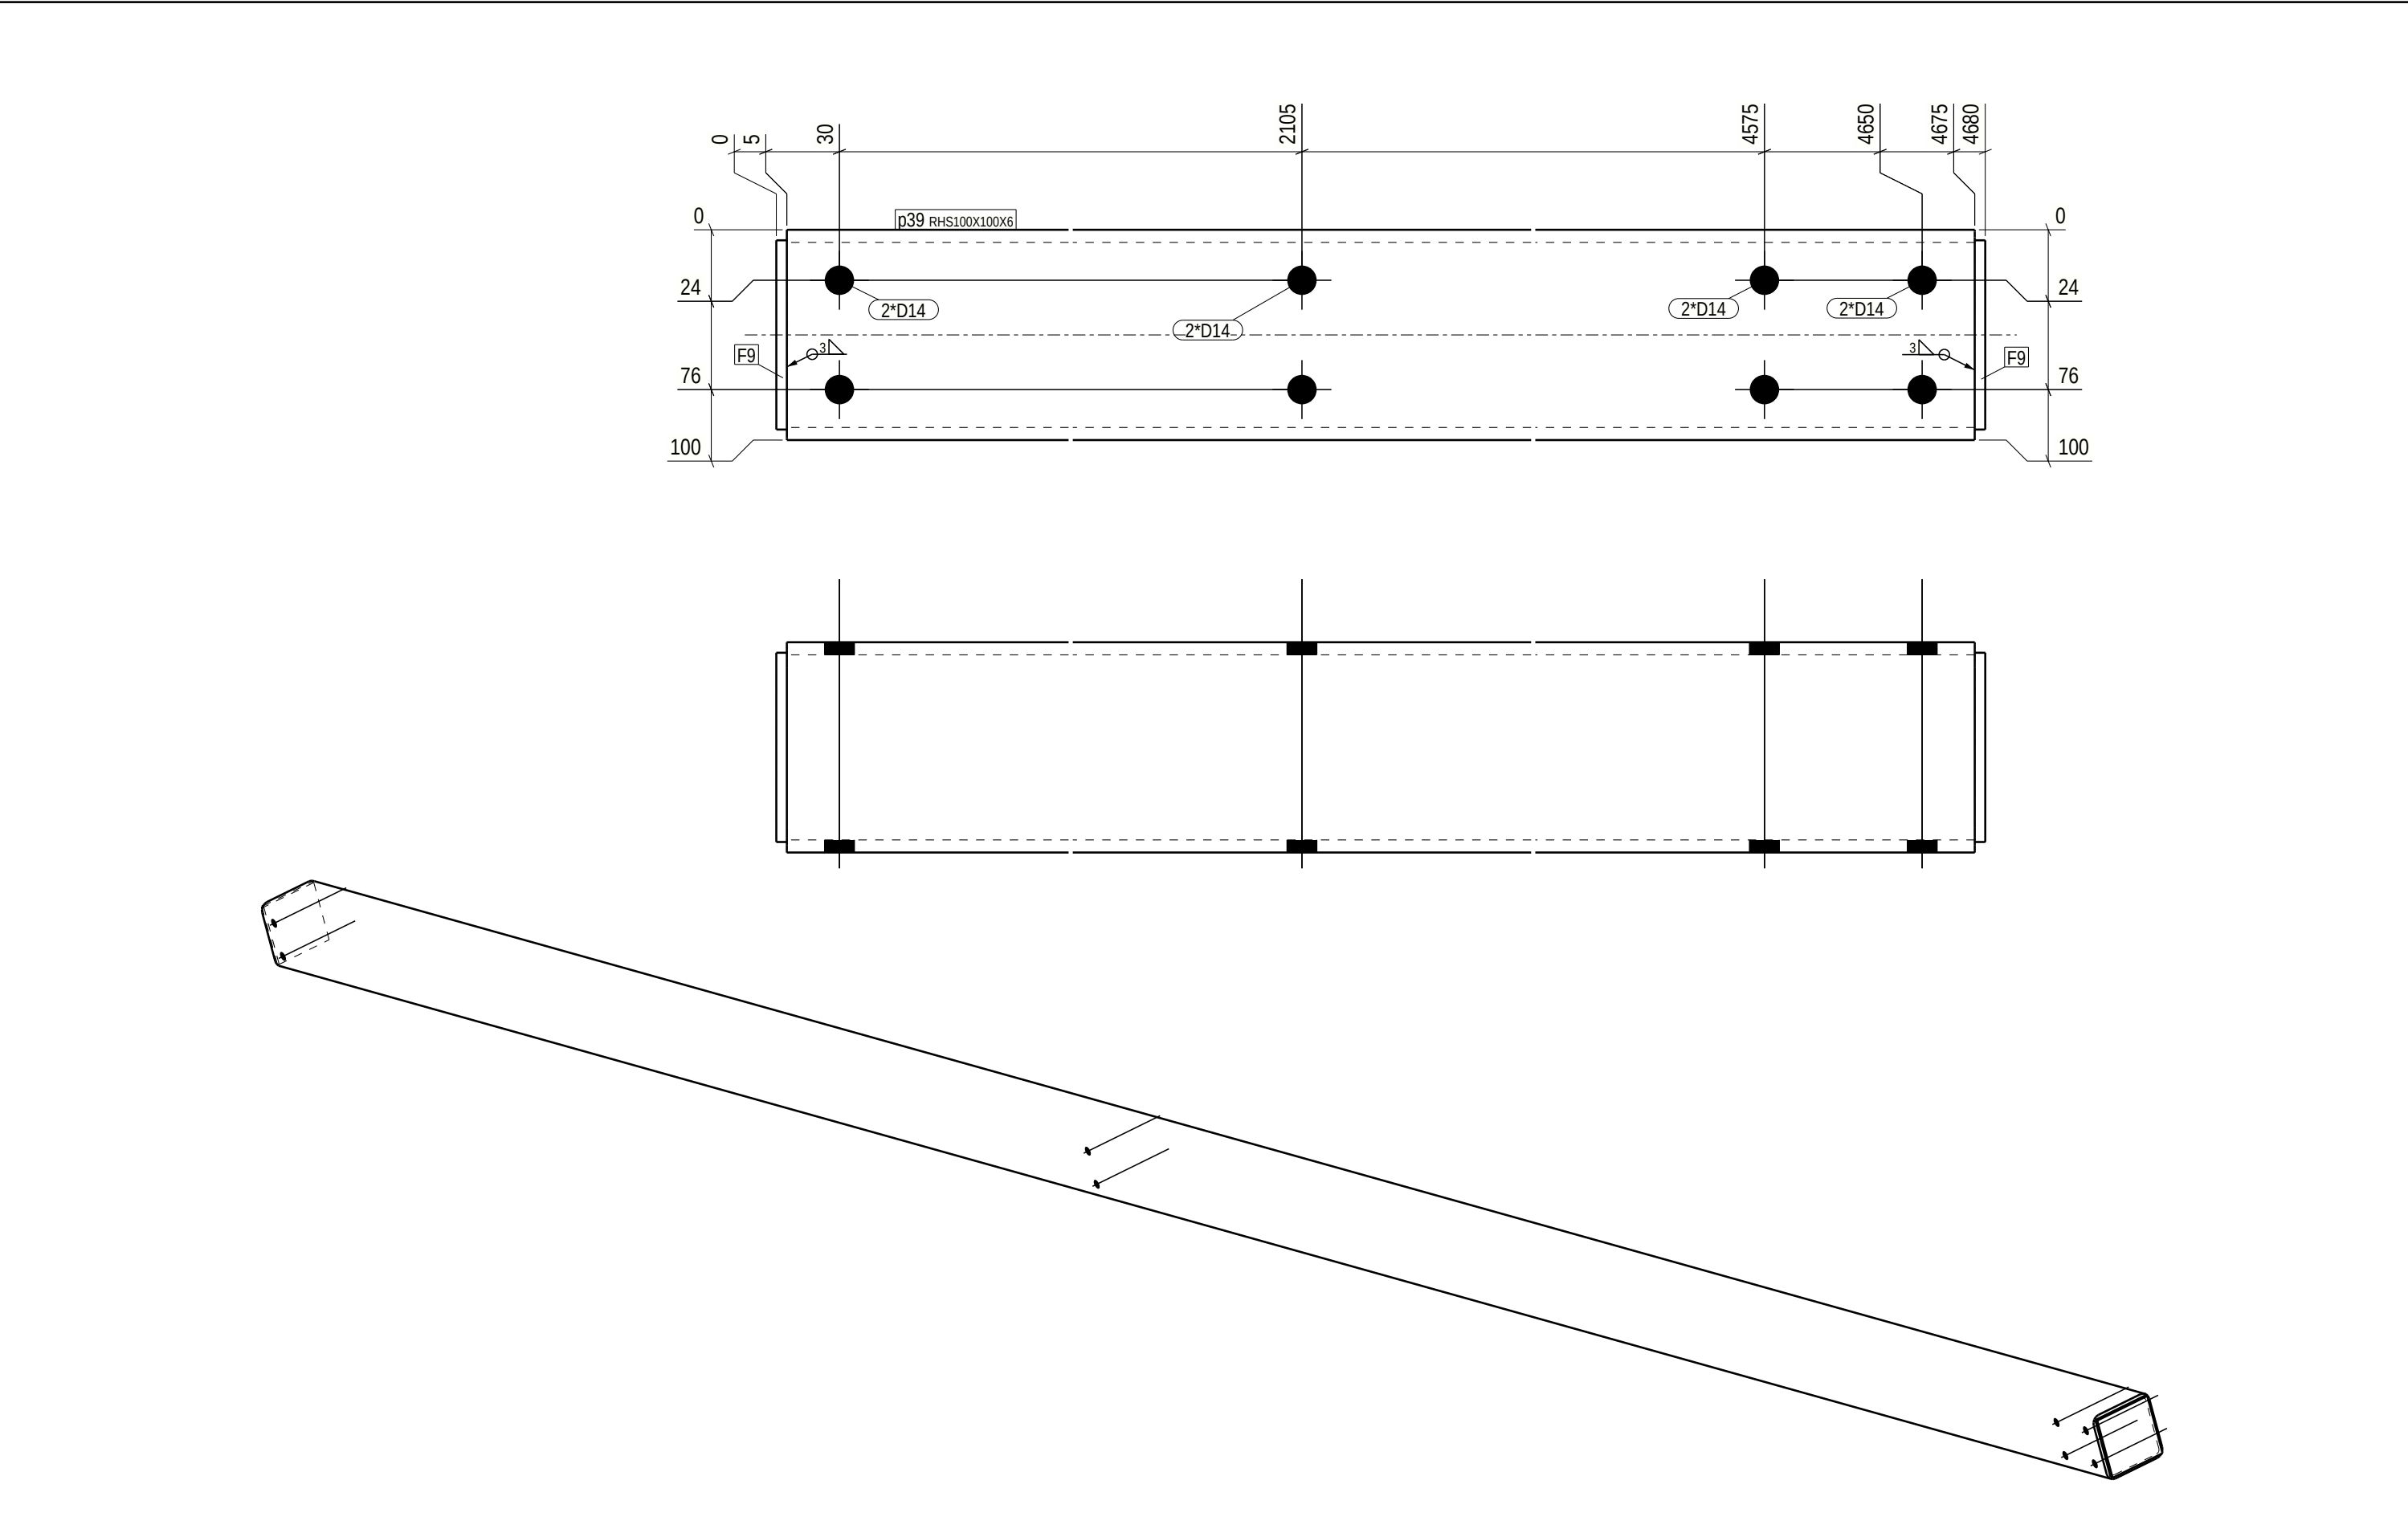

|                                      |              |          |     |                                |      |         |                                                |  |  |  |  |  |  |
|--------------------------------------|--------------|----------|-----|--------------------------------|------|---------|------------------------------------------------|--|--|--|--|--|--|
| GENERAL NOTES:                       |              |          |     |                                |      |         | For your safety, check weight before handling: |  |  |  |  |  |  |
|                                      |              |          |     |                                |      |         | 0-5kg Light    5-15kg Normal    15+kg Heavy    |  |  |  |  |  |  |
| ALL WELDS ARE 4                      |              |          |     |                                |      |         | UNLESS NOTED ON DRAWING                        |  |  |  |  |  |  |
| MATERIAL LIST FOR ASSEMBLY MK'D p.39 |              |          |     |                                |      |         | 1 No. Required                                 |  |  |  |  |  |  |
| Mark                                 | Profile      | Material | No. | Length                         | Area | Weight  | Finish Class<br>Standard                       |  |  |  |  |  |  |
| p39                                  | RHS100X100X6 | S355J2H  | 1   | 4670                           | 1.8  | 79.0 !! |                                                |  |  |  |  |  |  |
| F9                                   | FL5*90       | S355J2   | 2   | 90                             | 0.0  | 0.3     | Surface treatment info:                        |  |  |  |  |  |  |
| Total                                |              |          |     |                                | 1.8  | 79.6    |                                                |  |  |  |  |  |  |
|                                      |              |          |     | Thickness/start point-> length |      | No.     |                                                |  |  |  |  |  |  |

|       |          |   |
|-------|----------|---|
| PHASE | QUANTITY |   |
|       | 2        | 1 |

|            |  |
|------------|--|
| weld a = 4 |  |
|------------|--|

|                     |                                      |                     |                  |                  |                    |
|---------------------|--------------------------------------|---------------------|------------------|------------------|--------------------|
| * o 3 0 4 8 0 - 2 * |                                      | DS Stalkonstruktion |                  | * A p 3 9 *      |                    |
| PROJECT             | Akkasæter Lager- og vedlikeholdshall |                     | EXEC. CLASS      |                  | EXC 2              |
| MEMBER              | Portomfatning                        |                     | QUANTITY:        | 1                | PROJECT No 30480-2 |
| REVISION            |                                      | ISSUED: 07.11.2025  | DRAFTER: ZLL     | DRAWING No. p.39 |                    |
|                     |                                      |                     | BIM control: SST |                  |                    |