
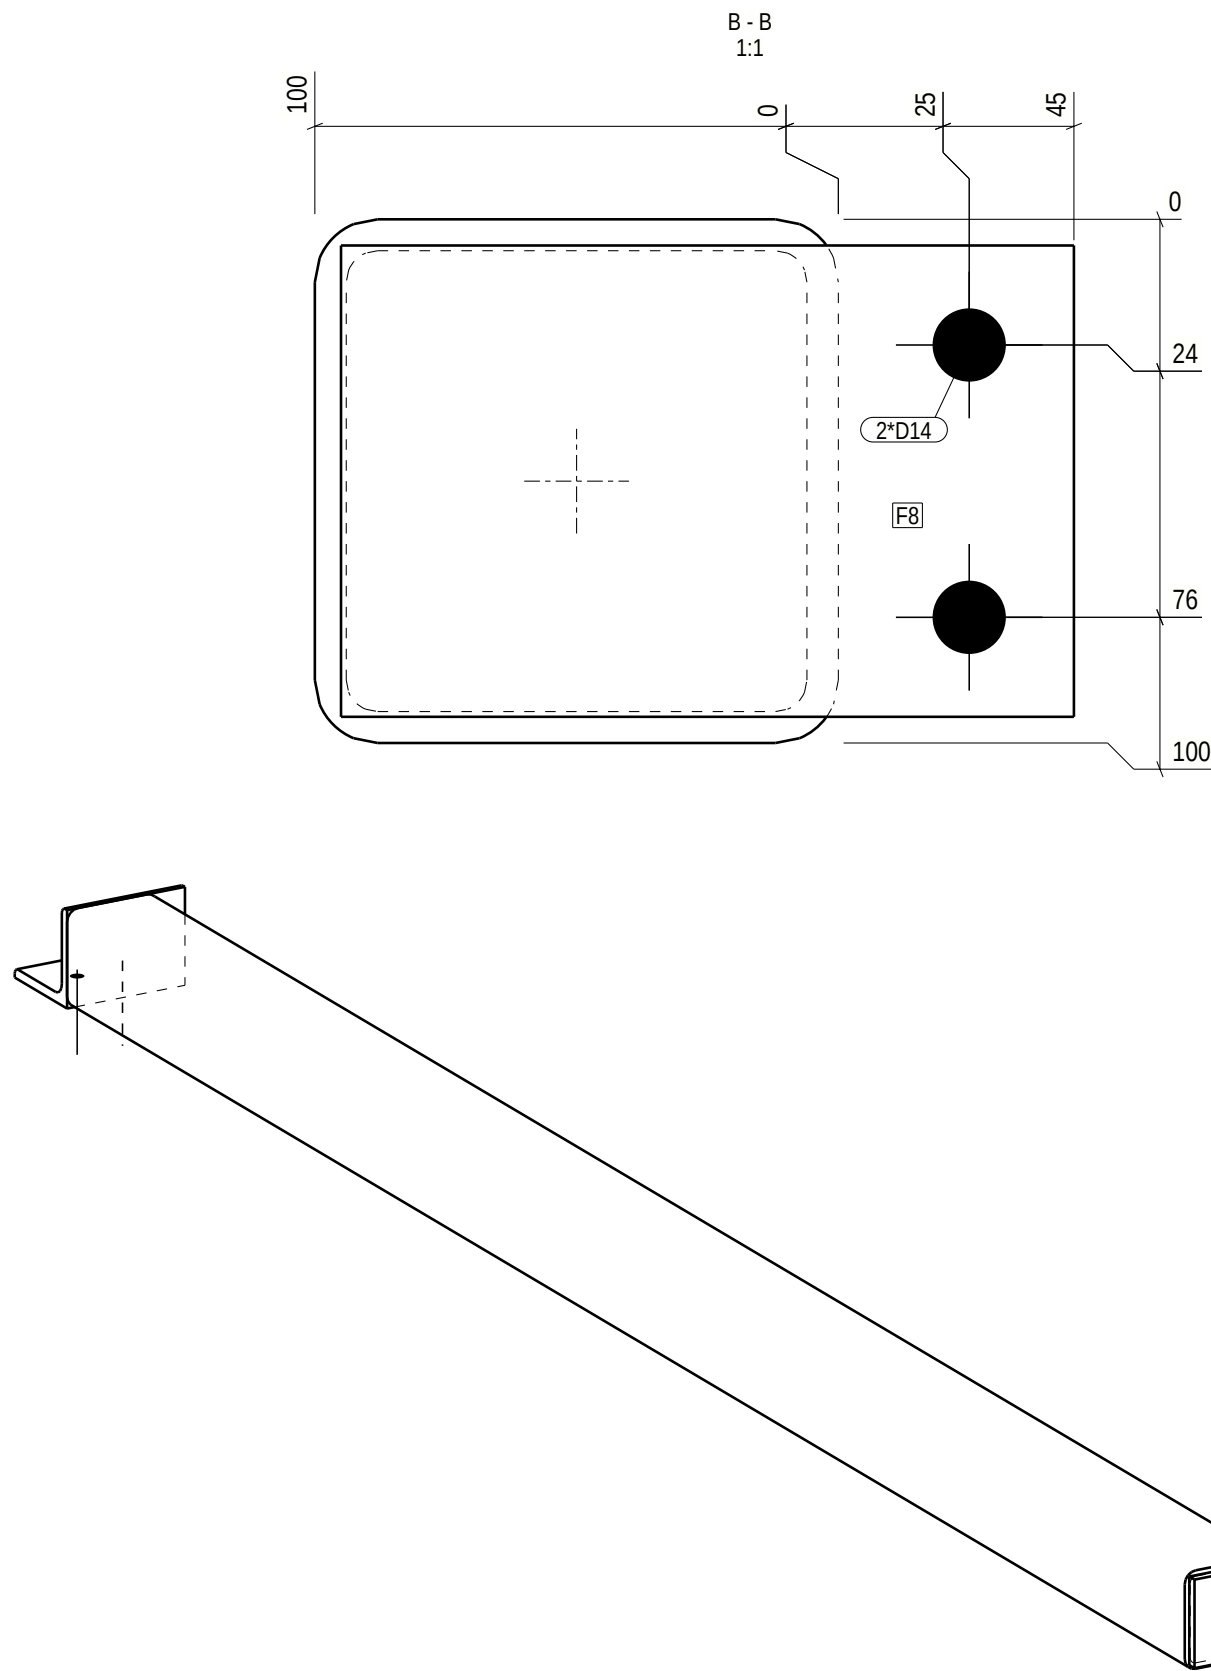
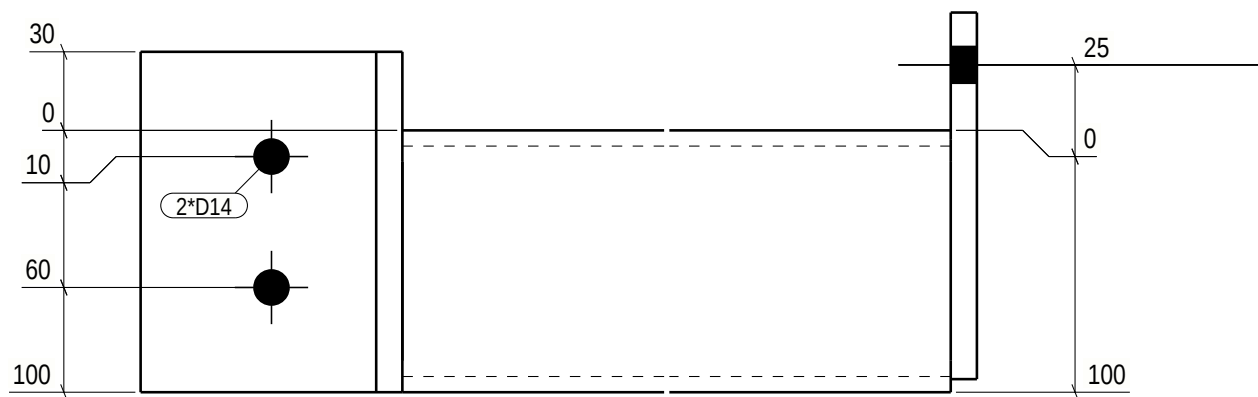


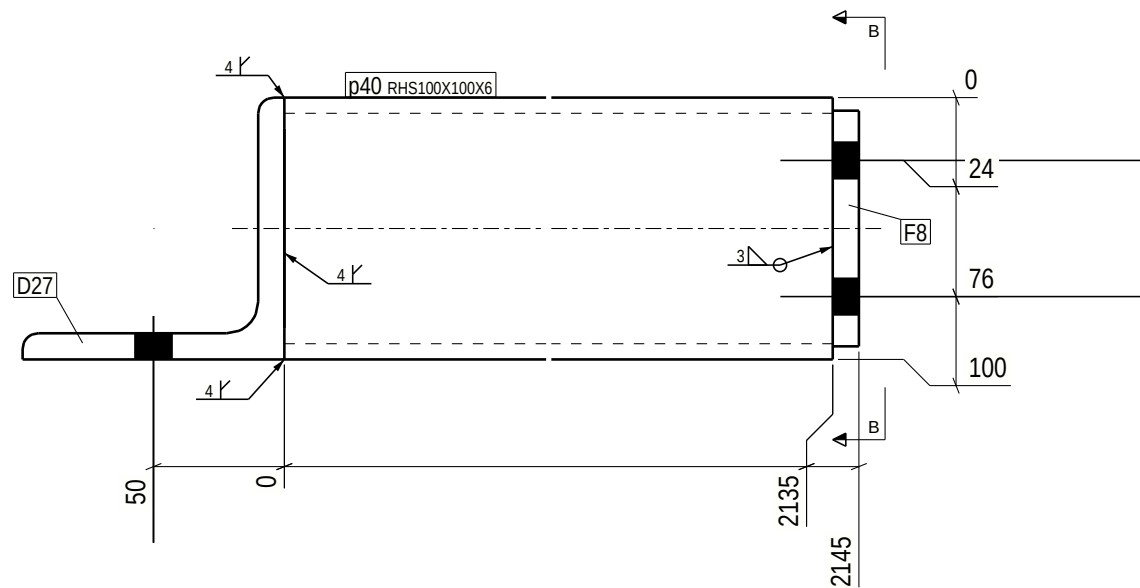

GENERAL NOTES:						
For your safety, check weight before handling:						
0-5kg Light 5-15kg Normal 15+kg Heavy						
ALL WELDS ARE 4 UNLESS NOTED ON DRAWING						
MATERIAL LIST FOR ASSEMBLY MK'D p.40						
1 No. Required						
Mark	Profile	Material	No.	Length	Area	Weight
p40	RHS100X100X6	S355J2H	1	2135	0.8	36.1 !!
D27	L100*10	S355J2	1	130	0.1	2.0
F8	FL10*90	S355J2	1	140	0.0	1.0
Total					0.9	39.1

Finish Class
Standard

Surface treatment info:	Thickness/start point-> length	No.
-------------------------	--------------------------------	-----

weld a = 4

PHASE	QUANTITY
2	1

* o 3 0 4 8 0 - 2 * DS Skalkonstruktion * A p 4 0 *					
PROJECT	Akkasæter Lager- og vedlikeholdshall			EXEC. CLASS	EXC 2
MEMBER	Portomfatning		QUANTITY:	1	PROJECT No 30480-2
REVISION		ISSUED: 07.11.2025	DRAFTER: ZLL	BIM control: SST	DRAWING No. p.40