
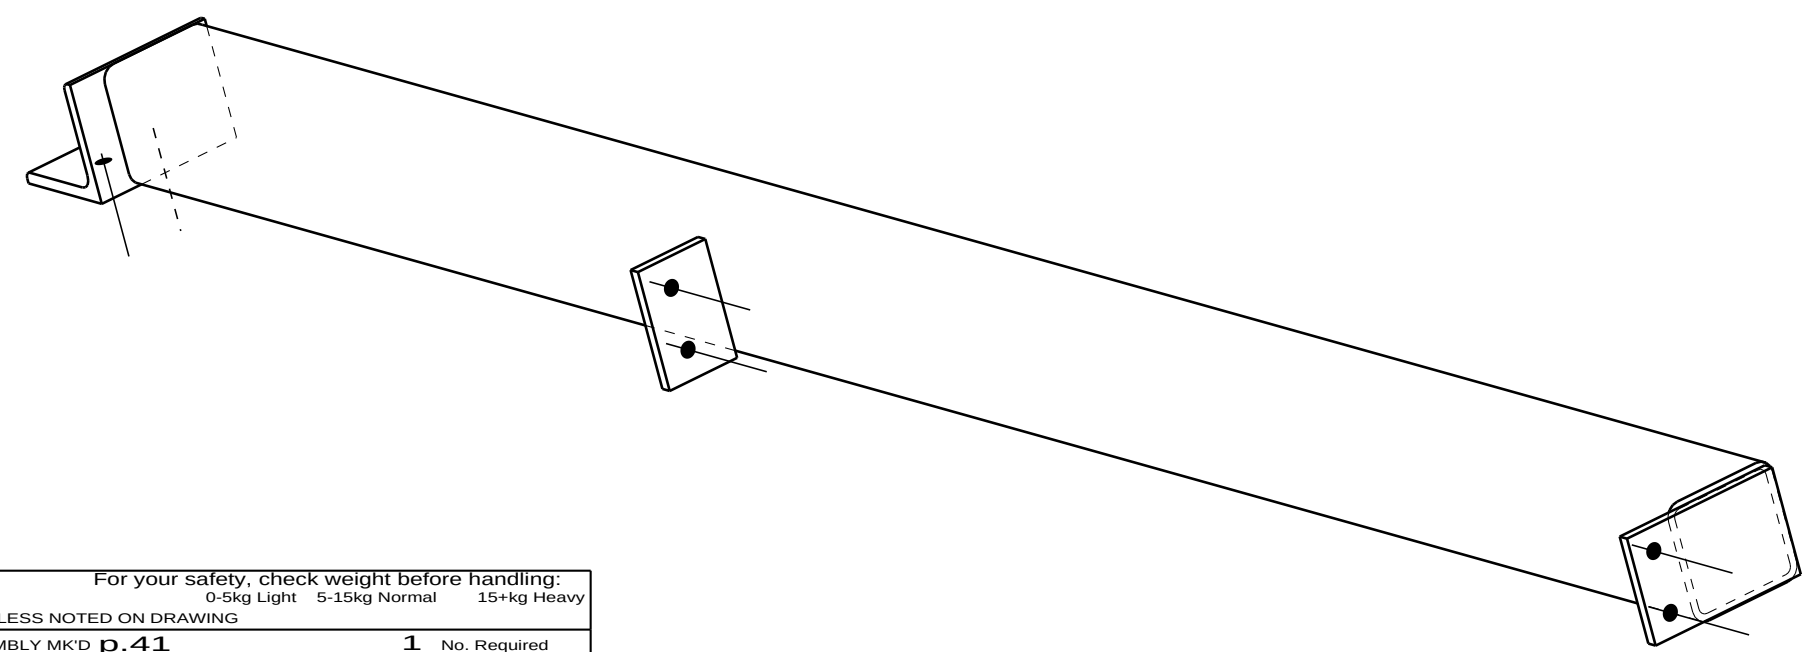
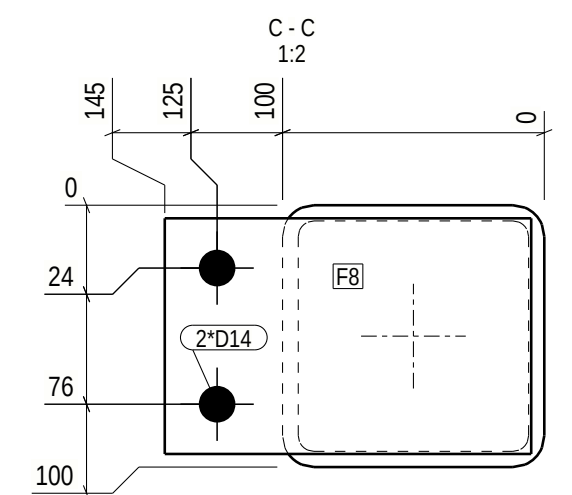
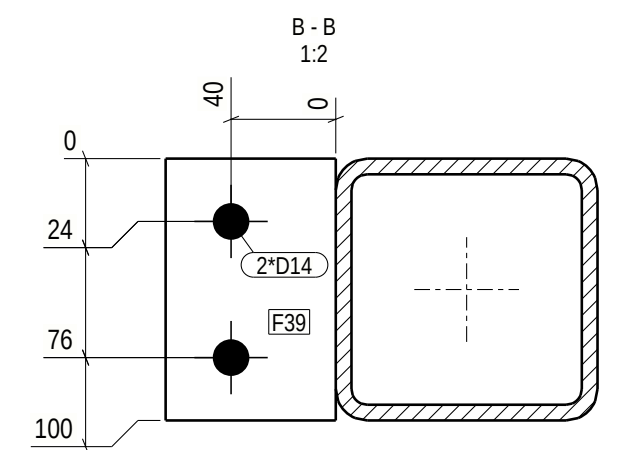


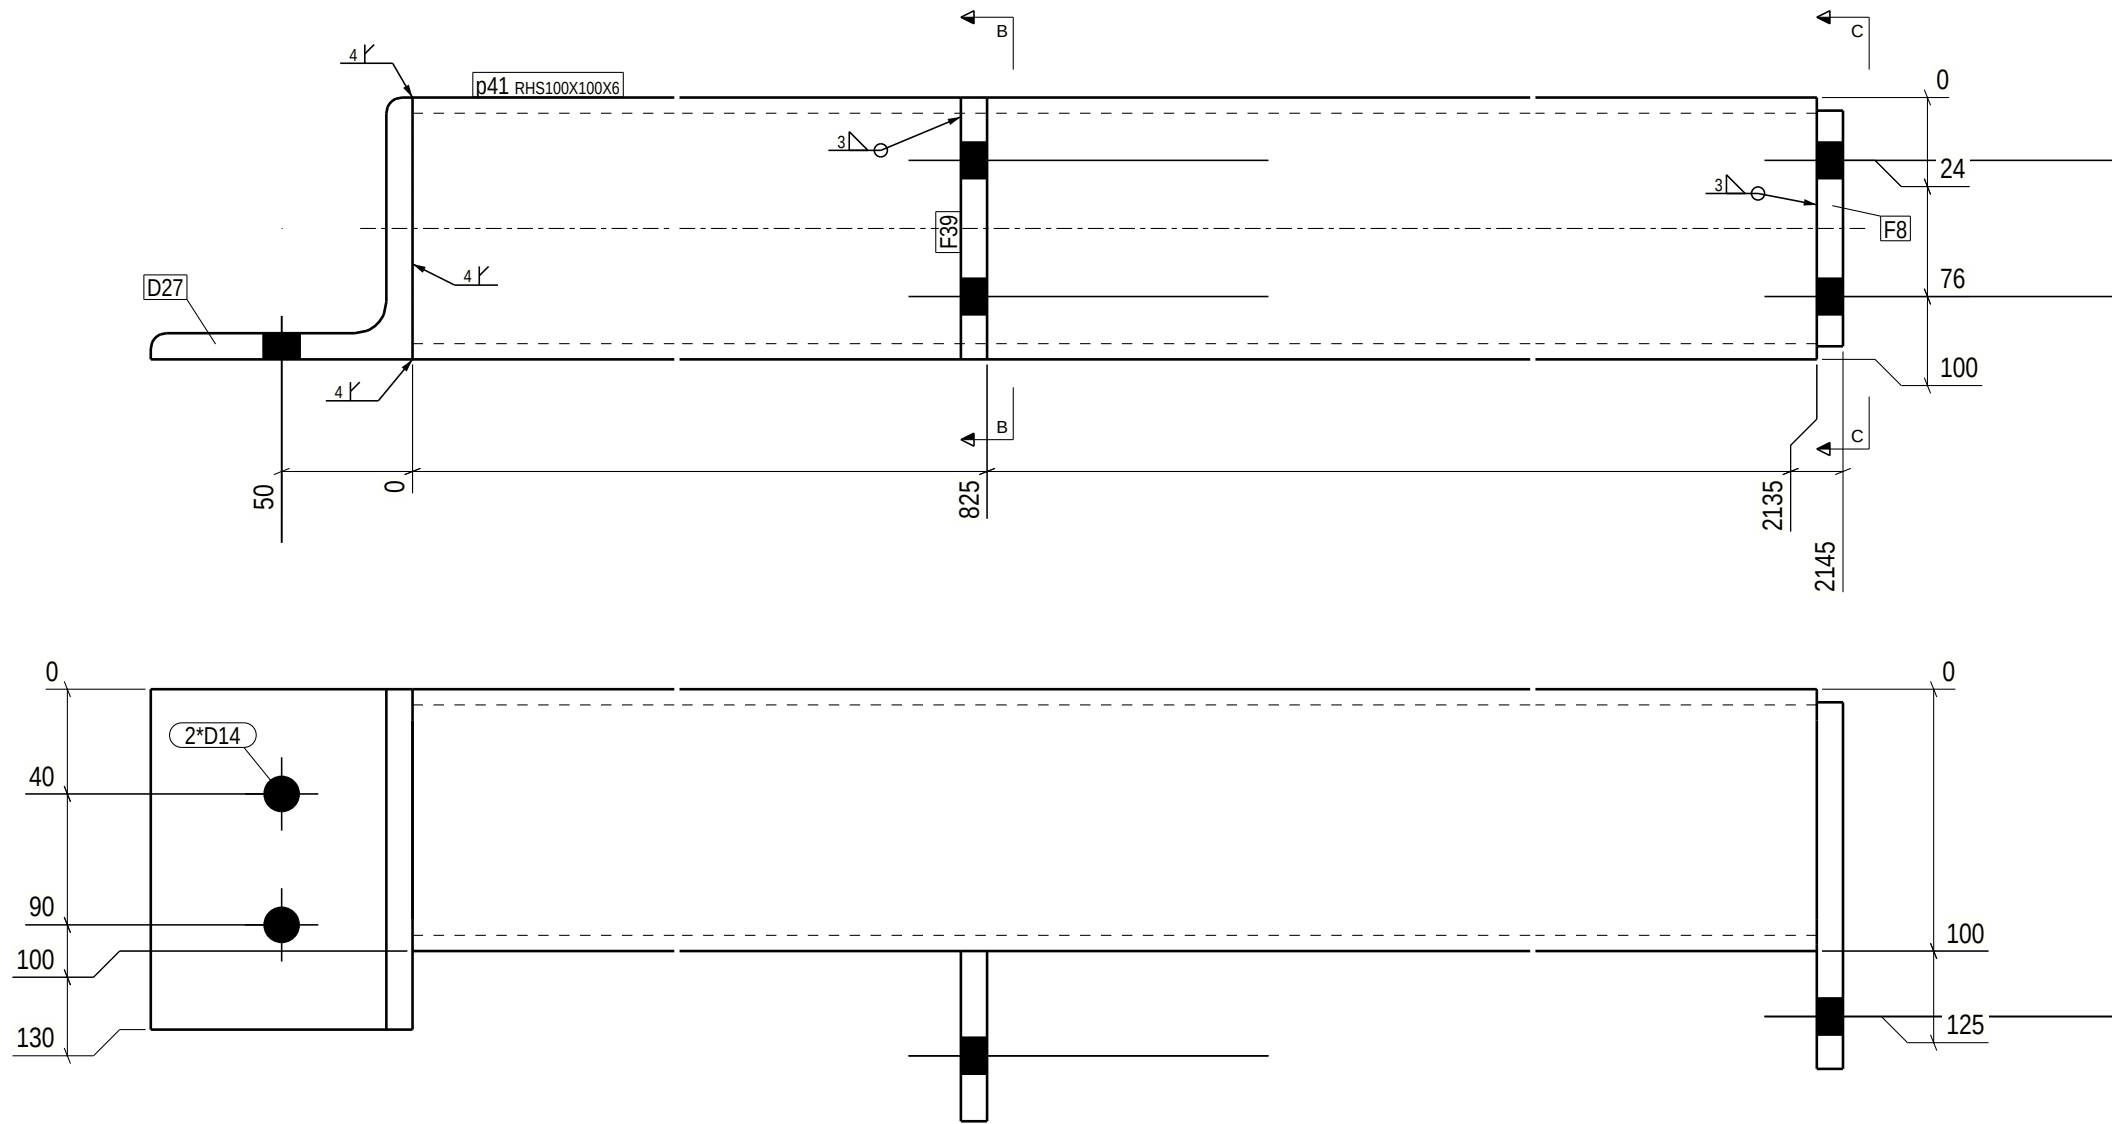

GENERAL NOTES: For your safety, check weight before handling:
0-5kg Light 5-15kg Normal 15+kg Heavy

ALL WELDS ARE 4 UNLESS NOTED ON DRAWING

MATERIAL LIST FOR ASSEMBLY MK'D p.41						1 No. Required
Mark	Profile	Material	No.	Length	Area	Weight
p41	RHS100X100X6	S355J2H	1	2135	0.8	36.1 !!
D27	L100*10	S355J2	1	130	0.1	2.0
F8	FL10*90	S355J2	1	140	0.0	1.0
F39	FL10*65	S355J2	1	100	0.0	0.5
Total					0.9	39.6

Finish Class
Standard

Surface treatment info: Thickness/start point--> length No.

weld a = 4

PHASE	QUANTITY
2	1

* o 3 0 4 8 0 - 2 * DS Steelkonstruktion * A p 4 1 *			
PROJECT	Akkasæter Lager- og vedlikeholdshall	EXEC. CLASS	EXC 2
MEMBER	Portomfatning	QUANTITY:	1 PROJECT No 30480-2
REVISION	ISSUED: 07.11.2025	DRAFTER: ZLL SST	DRAWING No. p.41