
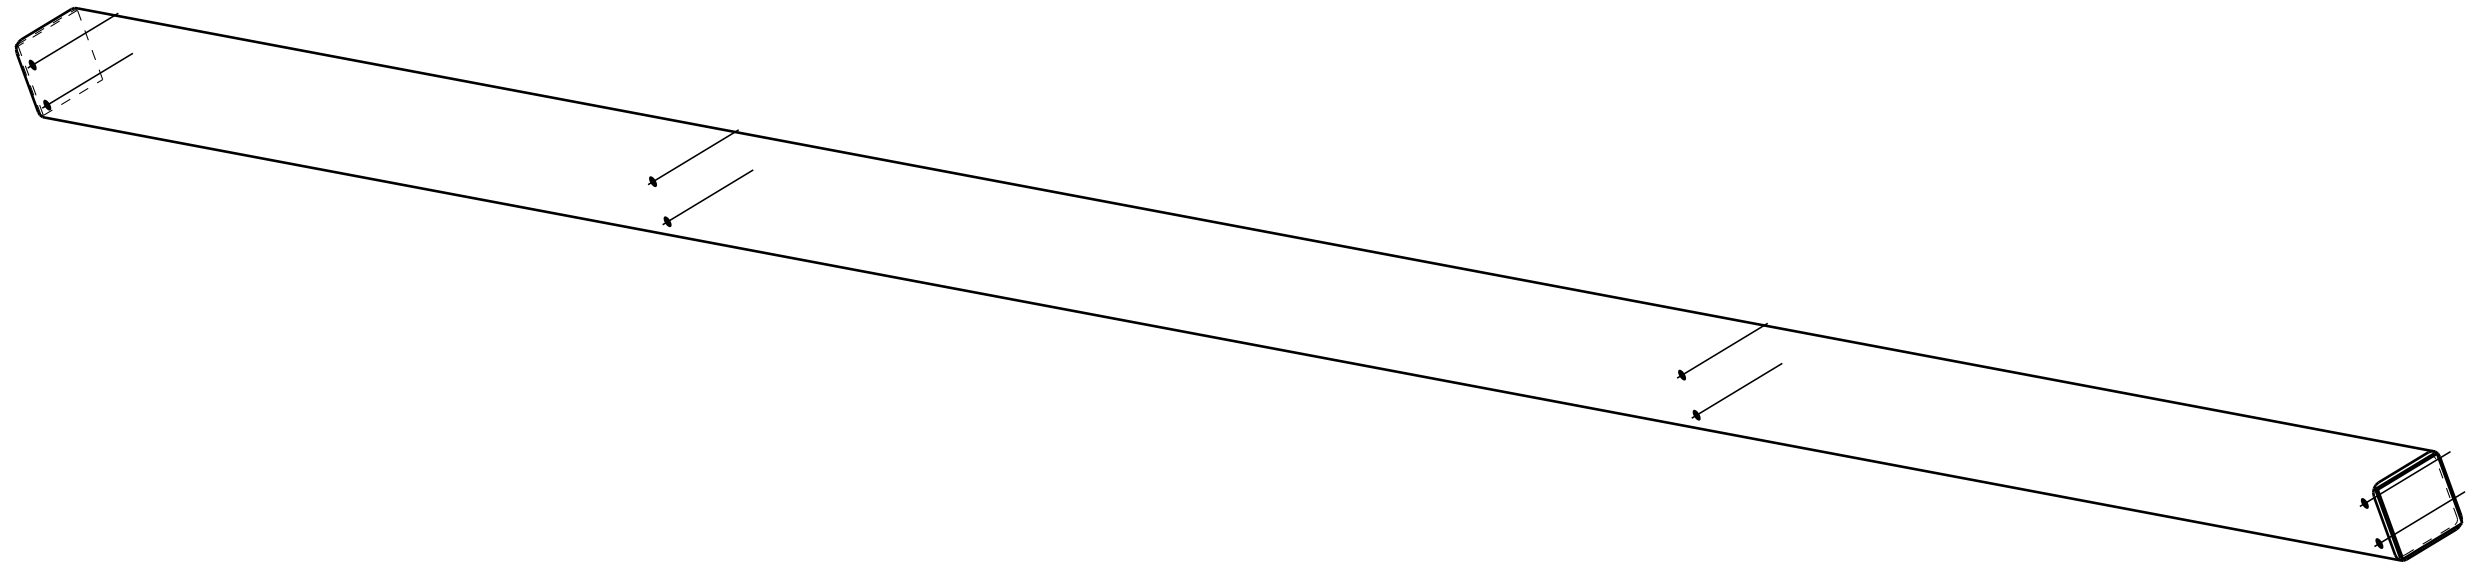
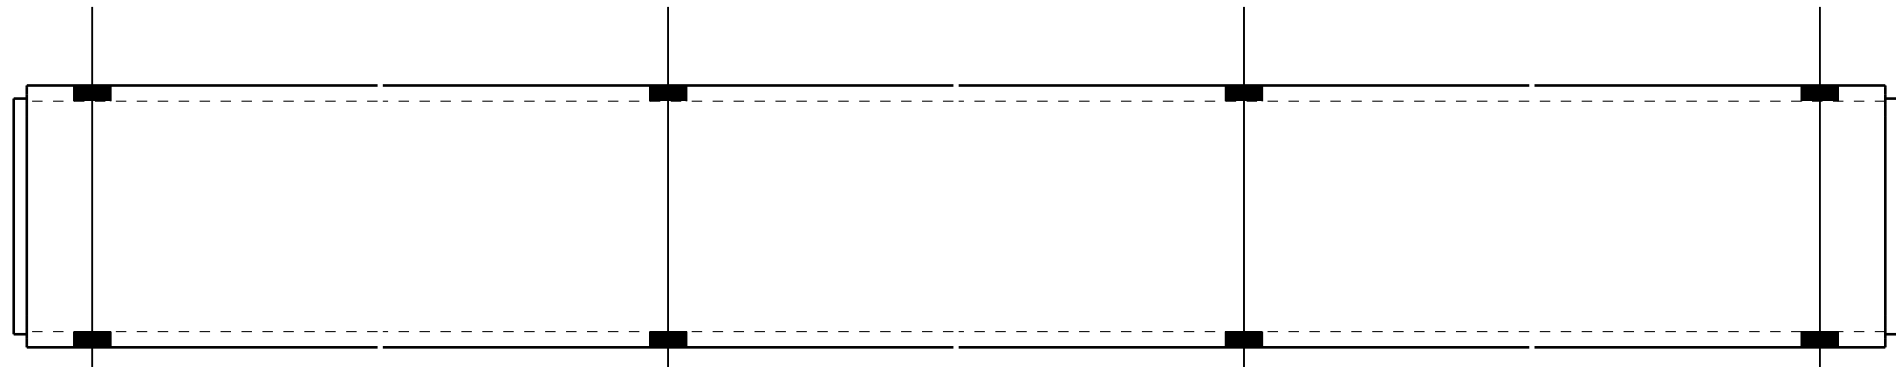


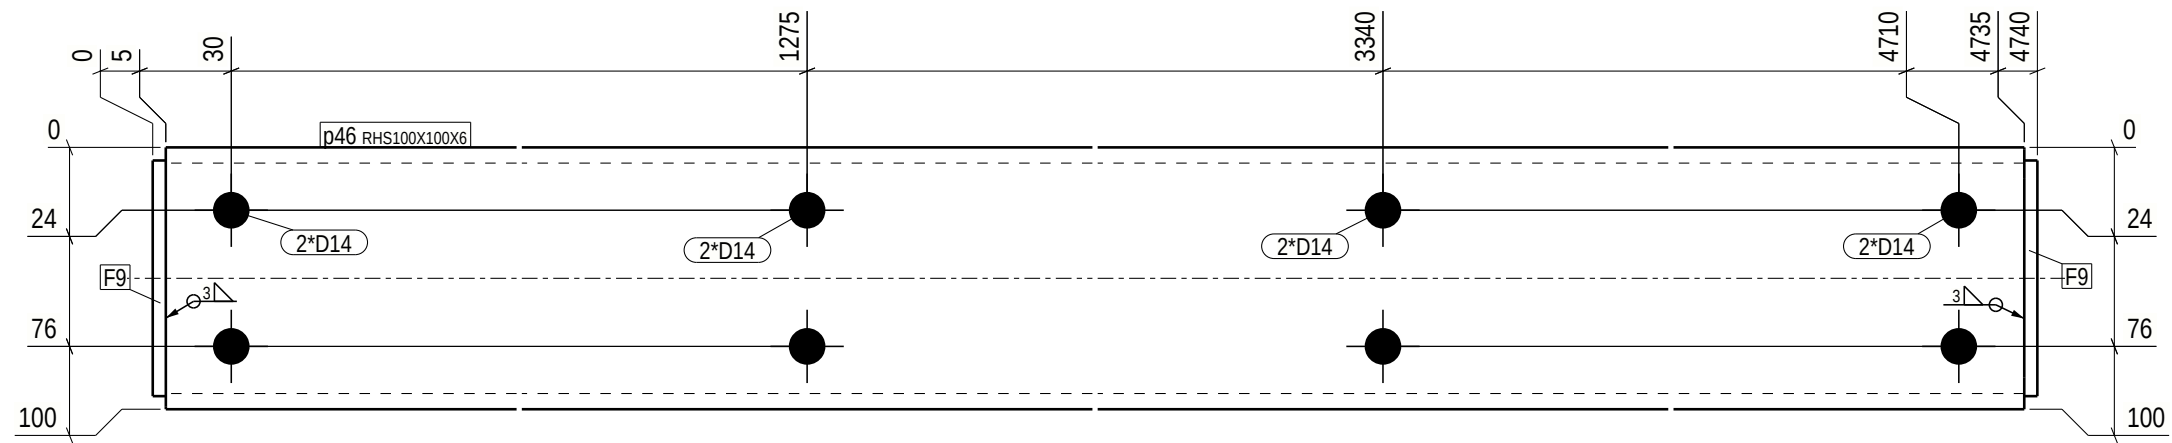

GENERAL NOTES:						
For your safety, check weight before handling:						
0-5kg Light 5-15kg Normal 15+kg Heavy						
ALL WELDS ARE 4 UNLESS NOTED ON DRAWING						
MATERIAL LIST FOR ASSEMBLY MK'D p.46						
2 No. Required						
Mark	Profile	Material	No.	Length	Area	Weight
p46	RHS100X100X6	S355J2H	1	4730	1.8	80.0 !!
F9	FL5*90	S355J2	2	90	0.0	0.3
Total				1.9	80.6	

Finish Class
Standard

Surface treatment info:	Thickness/start point--> length	No.
-------------------------	---------------------------------	-----

weld a = 4

PHASE	QUANTITY
2	2

* o 3 0 4 8 0 - 2 * DS Steelkonstruktion * A p 4 6 *					
PROJECT	Akkasæter Lager- og vedlikeholdshall			EXEC. CLASS	EXC 2
MEMBER	Portomfatning		QUANTITY:	2	PROJECT No 30480-2
REVISION	ISSUED: 07.11.2025		DRAFTER:	ZLL	DRAWING No. p.46
		BIM control:	ZLL	SST	