


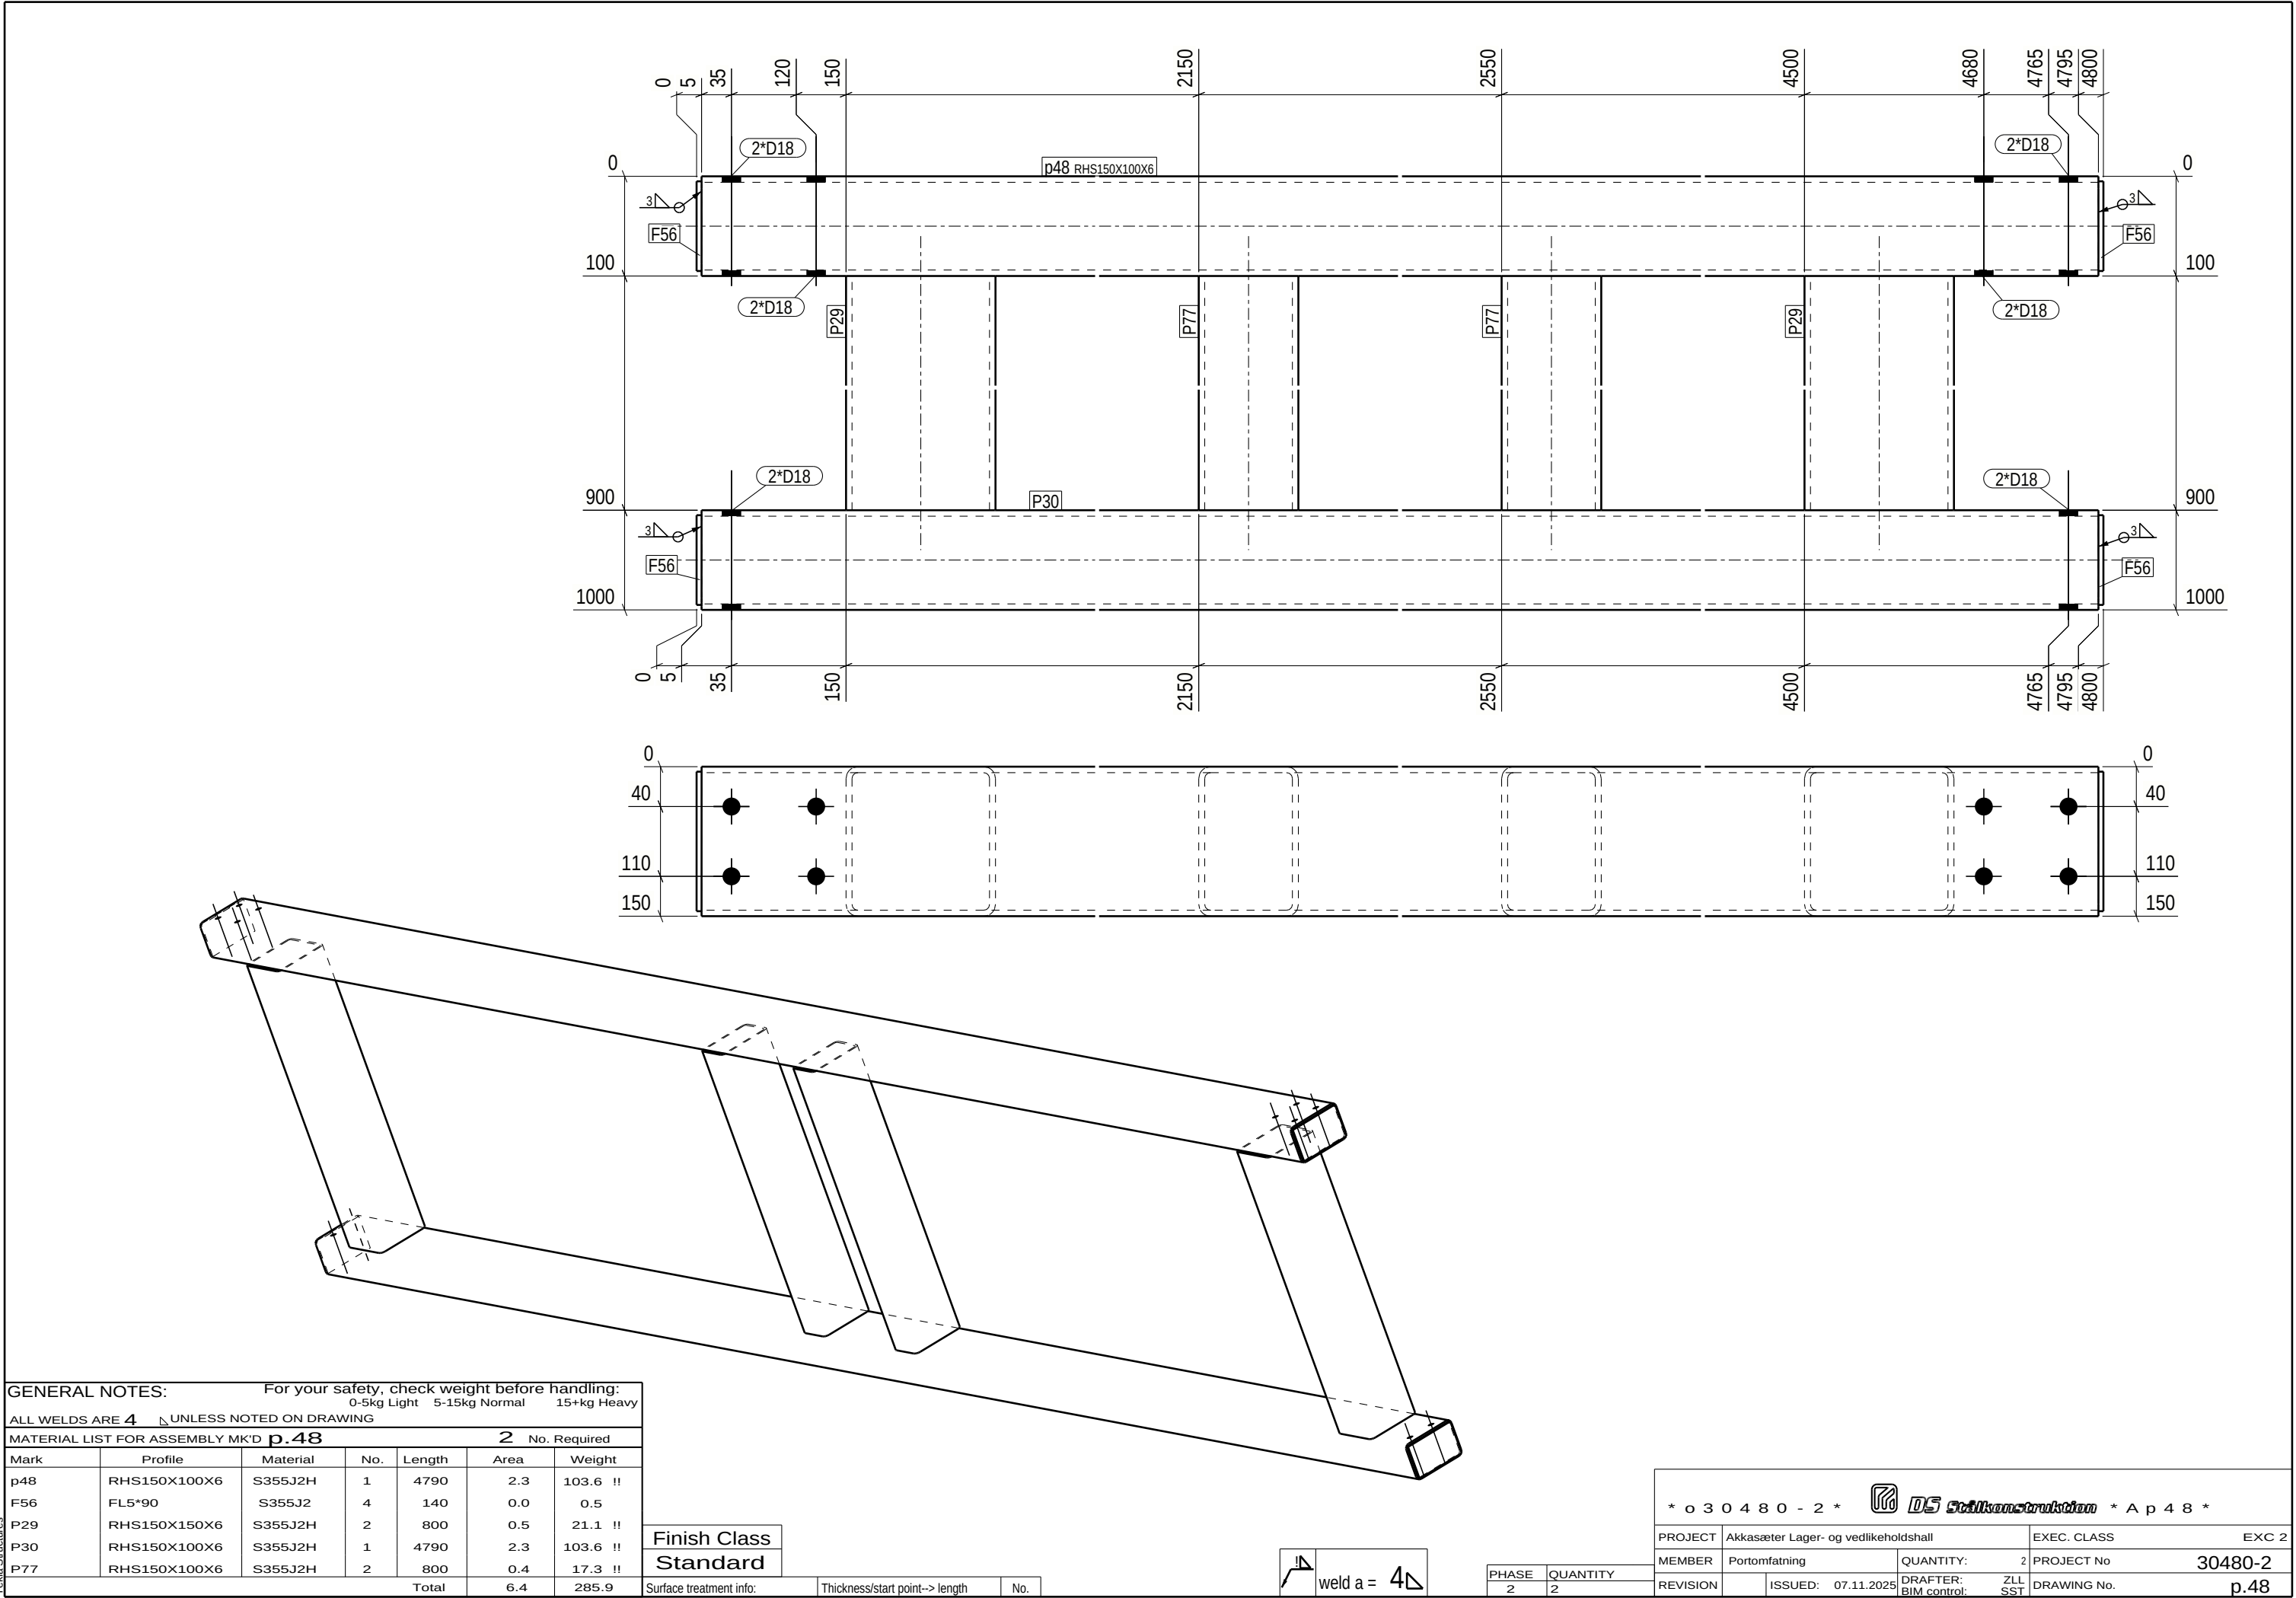

GENERAL NOTES: For your safety, check weight before handling:
0-5kg Light 5-15kg Normal 15+kg Heavy

ALL WELDS ARE 4 UNLESS NOTED ON DRAWING

MATERIAL LIST FOR ASSEMBLY MK'D p.48						2	No. Required
Mark	Profile	Material	No.	Length	Area	Weight	
p48	RHS150X100X6	S355J2H	1	4790	2.3	103.6 !!	
F56	FL5*90	S355J2	4	140	0.0	0.5	
P29	RHS150X150X6	S355J2H	2	800	0.5	21.1 !!	
P30	RHS150X100X6	S355J2H	1	4790	2.3	103.6 !!	
P77	RHS150X100X6	S355J2H	2	800	0.4	17.3 !!	
Total				6.4	285.9		

Finish Class
Standard

Surface treatment info: Thickness/start point-> length No.

weld a = 4

PHASE	QUANTITY
2	2

* o 3 0 4 8 0 - 2 * DS Steelkonstruktion * A p 4 8 *			
PROJECT	Akkasæter Lager- og vedlikeholdshall	EXEC. CLASS	EXC 2
MEMBER	Portomfatning	QUANTITY:	2 PROJECT No 30480-2
REVISION	ISSUED: 07.11.2025	DRAFTER: ZLL SST	DRAWING No. p.48