


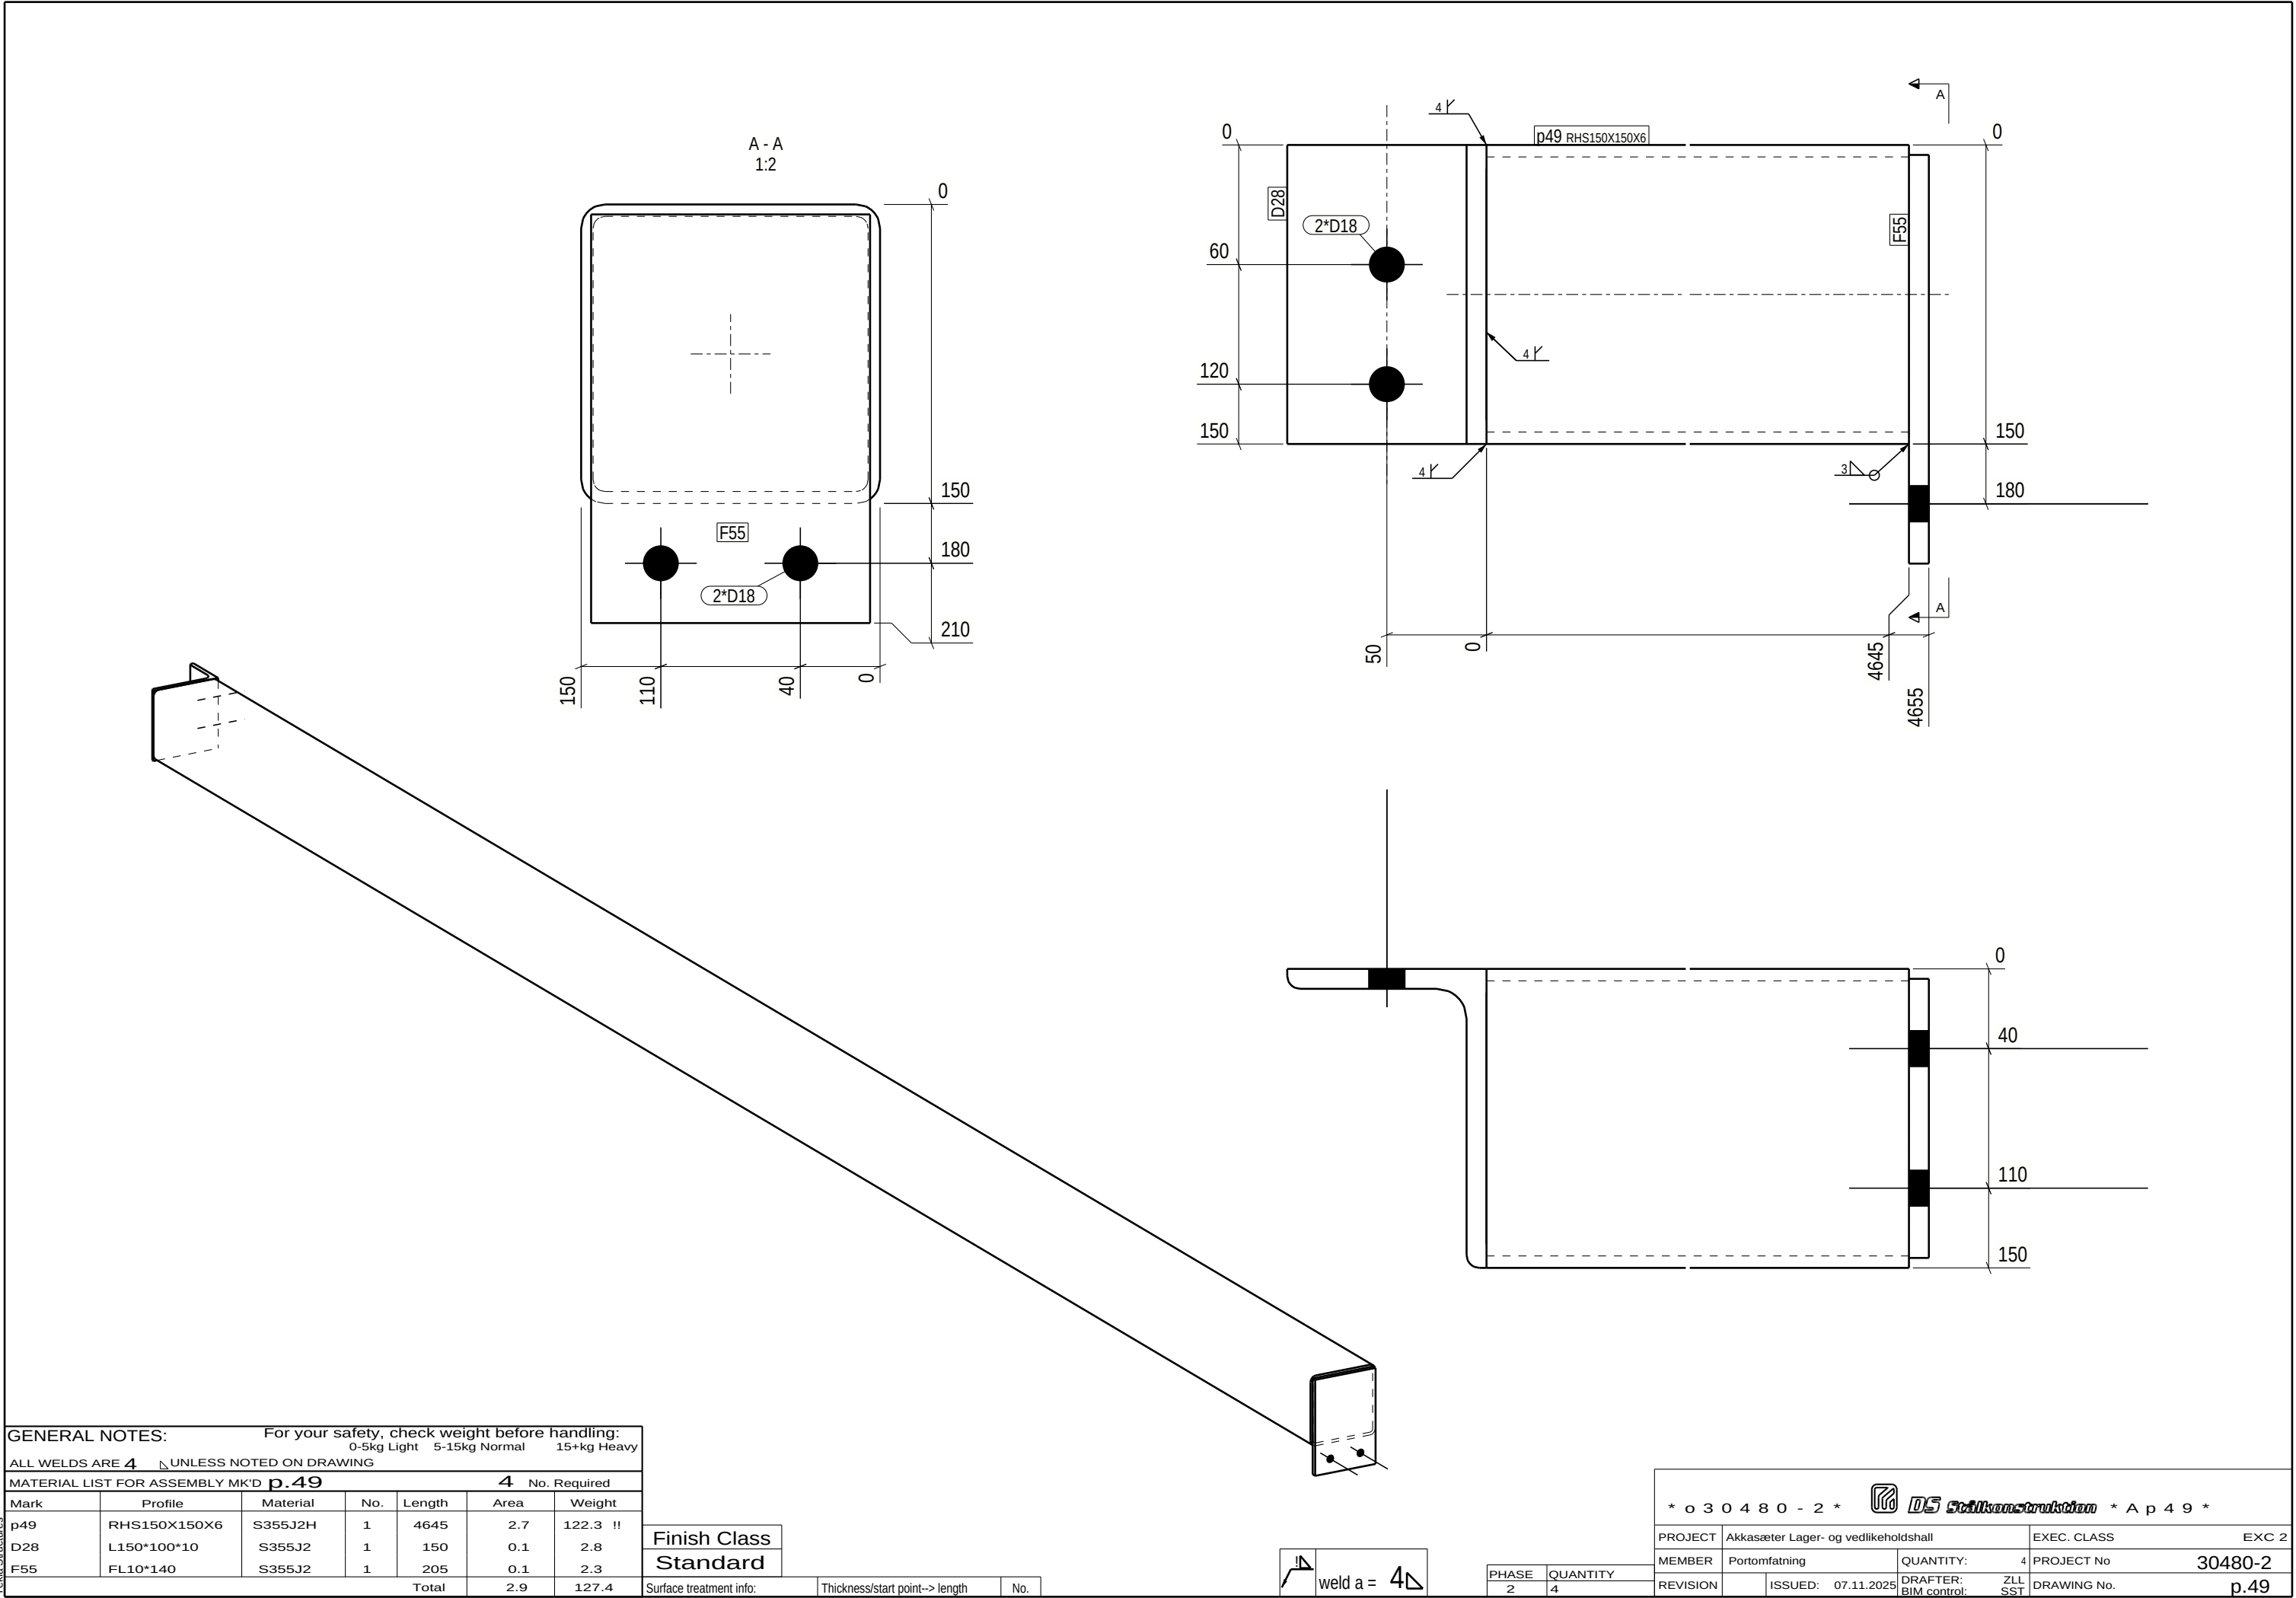

GENERAL NOTES:						
For your safety, check weight before handling:						
0-5kg Light 5-15kg Normal 15+kg Heavy						
ALL WELDS ARE 4 UNLESS NOTED ON DRAWING						
MATERIAL LIST FOR ASSEMBLY MK'D p.49						
4 No. Required						
Mark	Profile	Material	No.	Length	Area	Weight
p49	RHS150X150X6	S355J2H	1	4645	2.7	122.3 !!
D28	L150*100*10	S355J2	1	150	0.1	2.8
F55	FL10*140	S355J2	1	205	0.1	2.3
Total				2.9	127.4	

Finish Class
Standard

Surface treatment info:	Thickness/start point--> length	No.
-------------------------	---------------------------------	-----

weld a = 4

PHASE	QUANTITY
2	4

* o 3 0 4 8 0 - 2 * DS Skanska Konstruktion * A p 4 9 *			
PROJECT	Akkasæter Lager- og vedlikeholdshall	EXEC. CLASS	EXC 2
MEMBER	Portomfatning	QUANTITY:	4
REVISION	ISSUED: 07.11.2025	DRAFTER: ZLL	PROJECT No 30480-2
		BIM control: SST	DRAWING No. p.49