


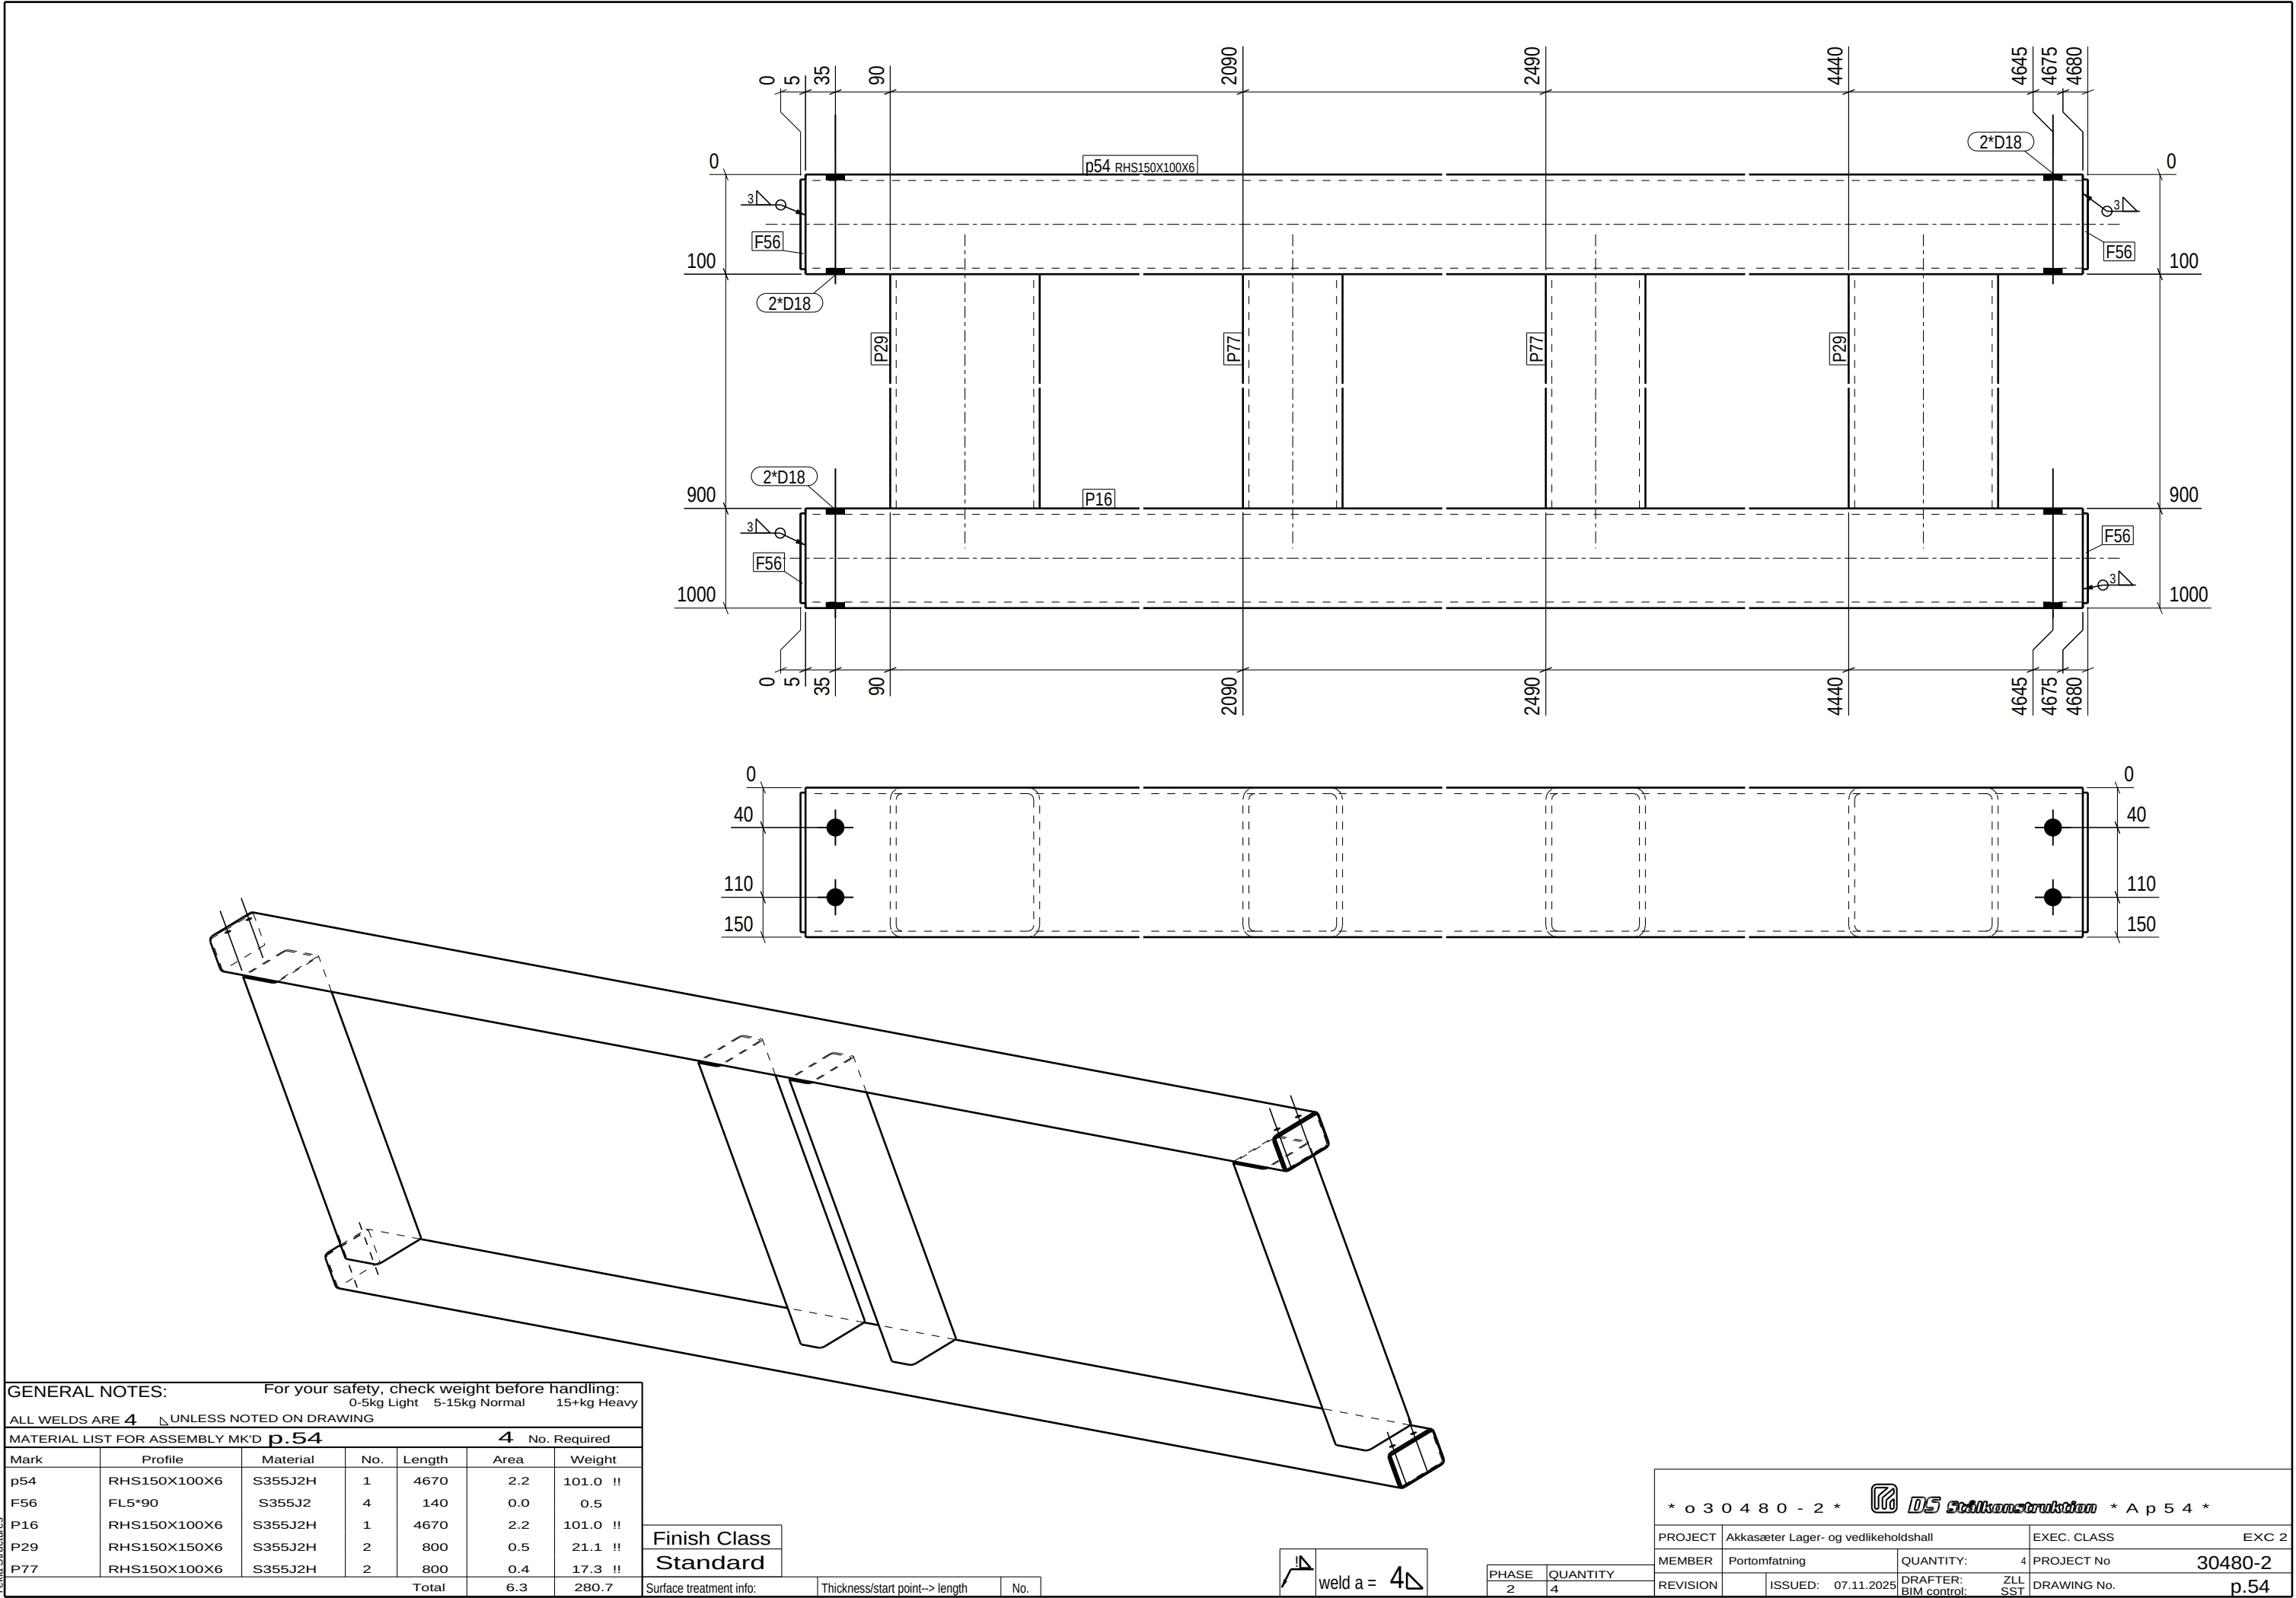

GENERAL NOTES: For your safety, check weight before handling:
0-5kg Light 5-15kg Normal 15+kg Heavy

MATERIAL LIST FOR ASSEMBLY MK'D p.54						4 No. Required
Mark	Profile	Material	No.	Length	Area	Weight
p54	RHS150X100X6	S355J2H	1	4670	2.2	101.0 !!
F56	FL5*90	S355J2	4	140	0.0	0.5
P16	RHS150X100X6	S355J2H	1	4670	2.2	101.0 !!
P29	RHS150X150X6	S355J2H	2	800	0.5	21.1 !!
P77	RHS150X100X6	S355J2H	2	800	0.4	17.3 !!
Total					6.3	280.7

Finish Class
Standard

Surface treatment info: Thickness/start point-> length No.

weld a = 4

PHASE	QUANTITY
2	4

* o 3 0 4 8 0 - 2 *  DS <i>Stålkonstruktion</i> * A p 5 4 *			
PROJECT	Akkasæter Lager- og vedlikeholdshall		EXEC. CLASS
MEMBER	Portomfatning	QUANTITY:	PROJECT No
REVISION	ISSUED: 07.11.2025	DRAFTER: ZLL	DRAWING No.
		BIM control: SST	

30480-2

p.54