


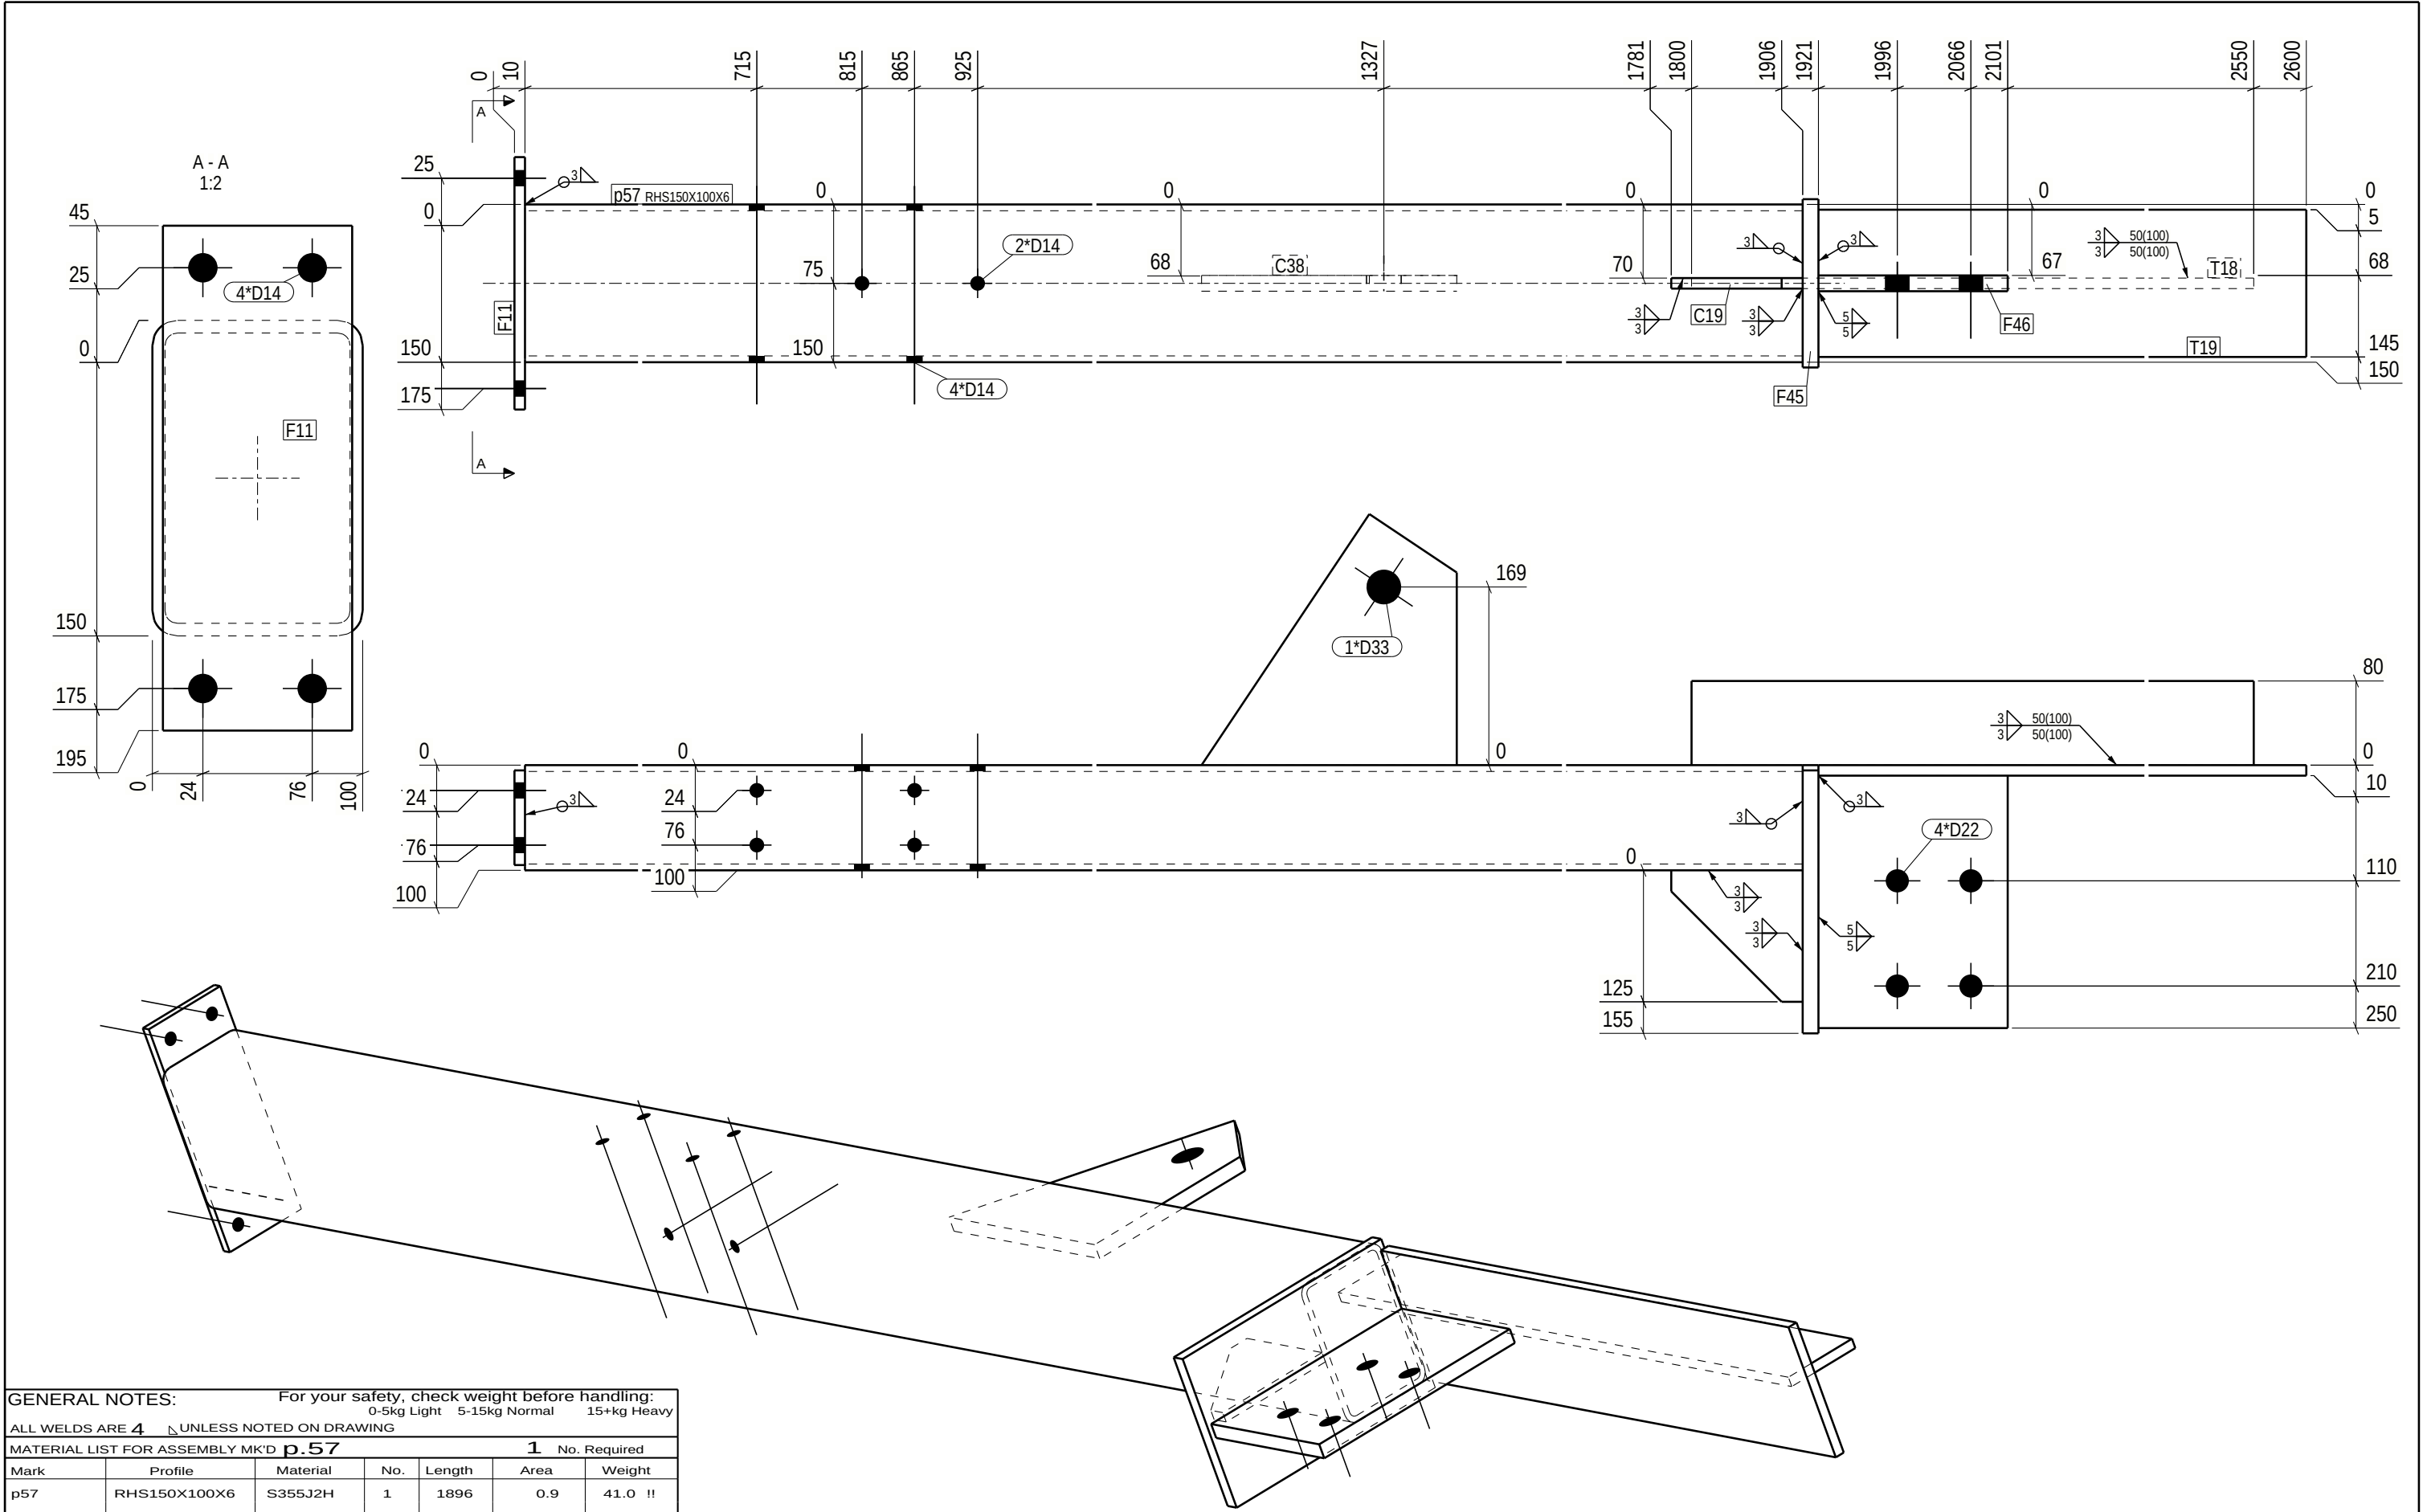

GENERAL NOTES: For your safety, check weight before handling:

ALL WELDS ARE 4 UNLESS NOTED ON DRAWING

MATERIAL LIST FOR ASSEMBLY MK'D p.57 1 No. Required

Mark	Profile	Material	No.	Length	Area	Weight
p57	RHS150X100X6	S355J2H	1	1896	0.9	41.0 !!
C19	PL10*125	S355J2	1	125	0.0	0.8
C38	PL15*202	S355J2	1	287	0.1	4.3
F11	FL10*90	S355J2	1	240	0.0	1.7
F45	FL15*160	S355J2	1	250	0.1	4.7
F46	FL15*180	S355J2	1	240	0.1	5.1
T18	FL10*80	S355J2	1	750	0.1	4.7
T19	FL10*140	S355J2	1	679	0.2	7.5
Total					1.6	69.8

Finish Class
Standard

Surface treatment info: Thickness/start point-> length No.

weld a = 4

PHASE	QUANTITY
2	1

* o 3 0 4 8 0 - 2 * DS Steelkonstruktion * A p 5 7 *			
PROJECT	Akkasæter Lager- og vedlikeholdshall	EXEC. CLASS	EXC 2
MEMBER	Portomfatning	QUANTITY:	1 PROJECT No 30480-2
REVISION	ISSUED: 07.11.2025	DRAFTER: ZLL SST	DRAWING No. p.57