
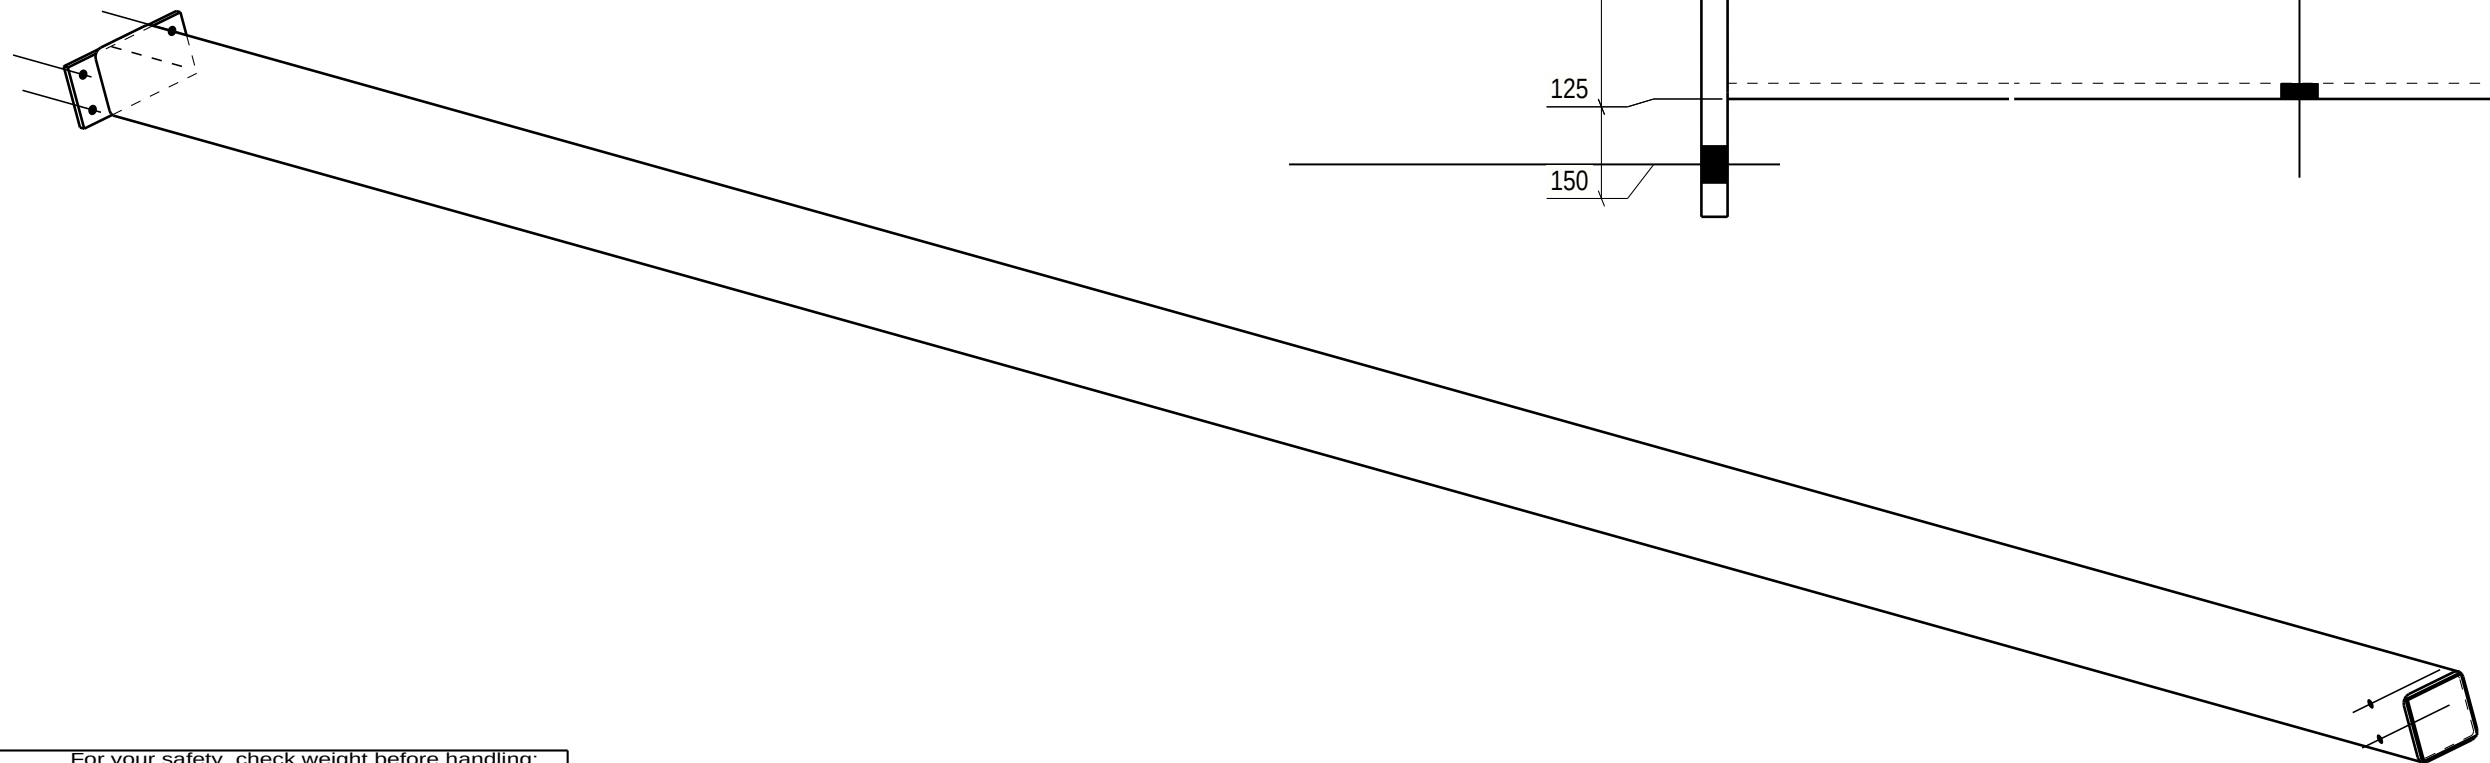
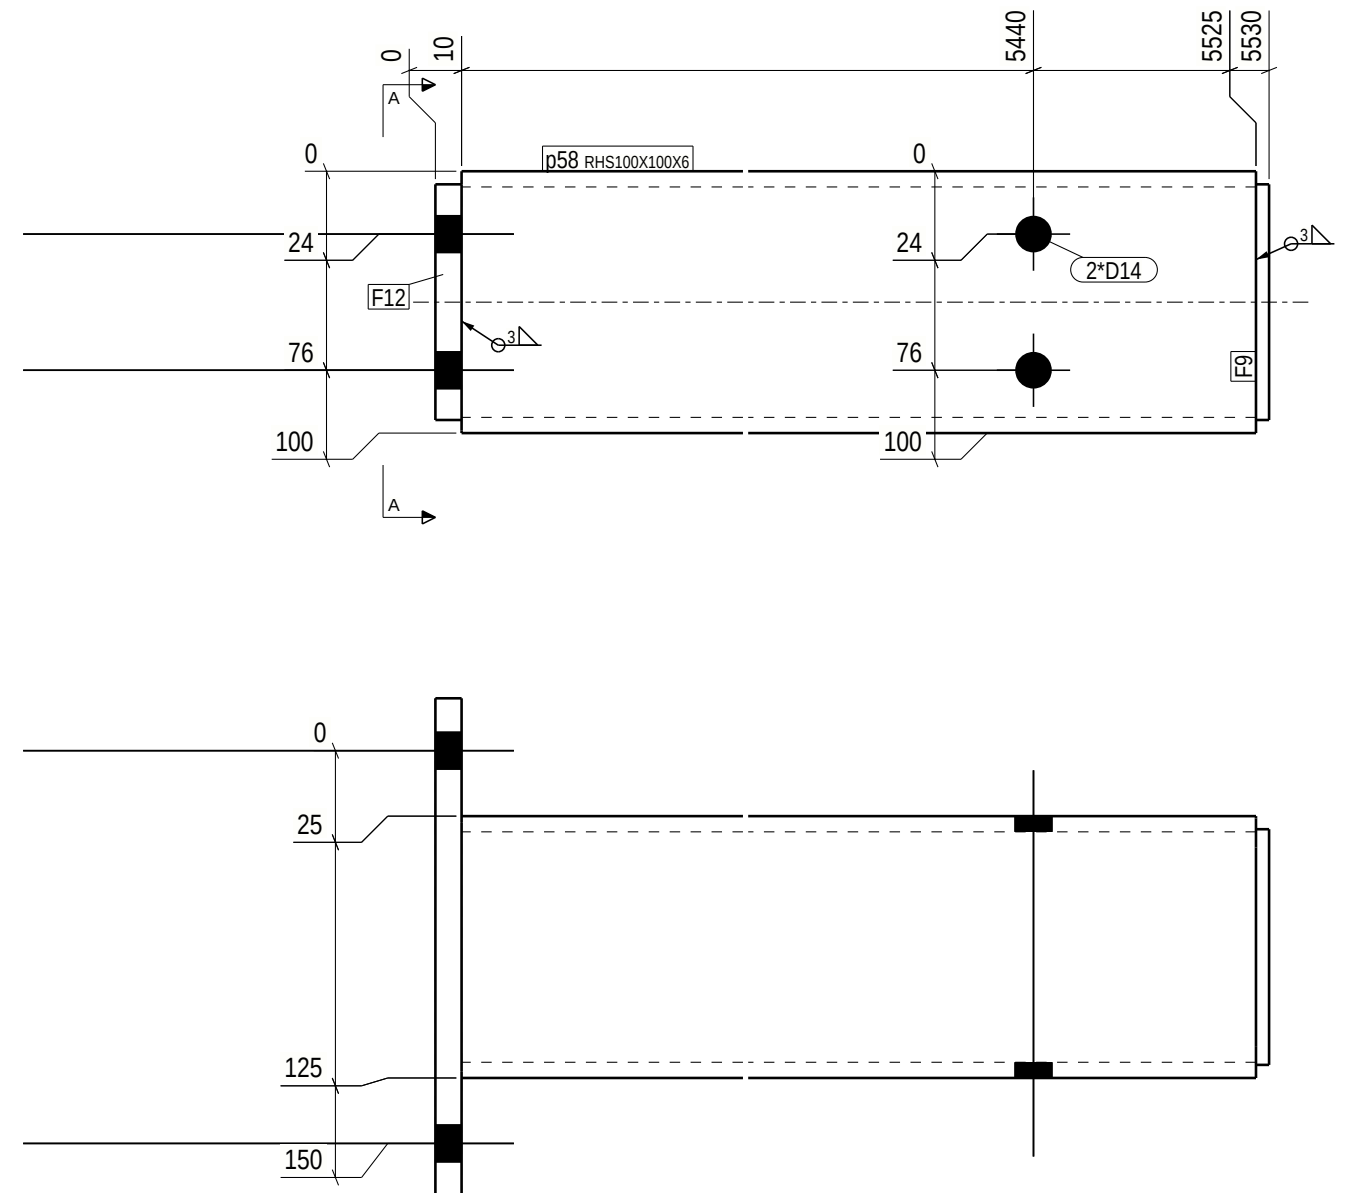


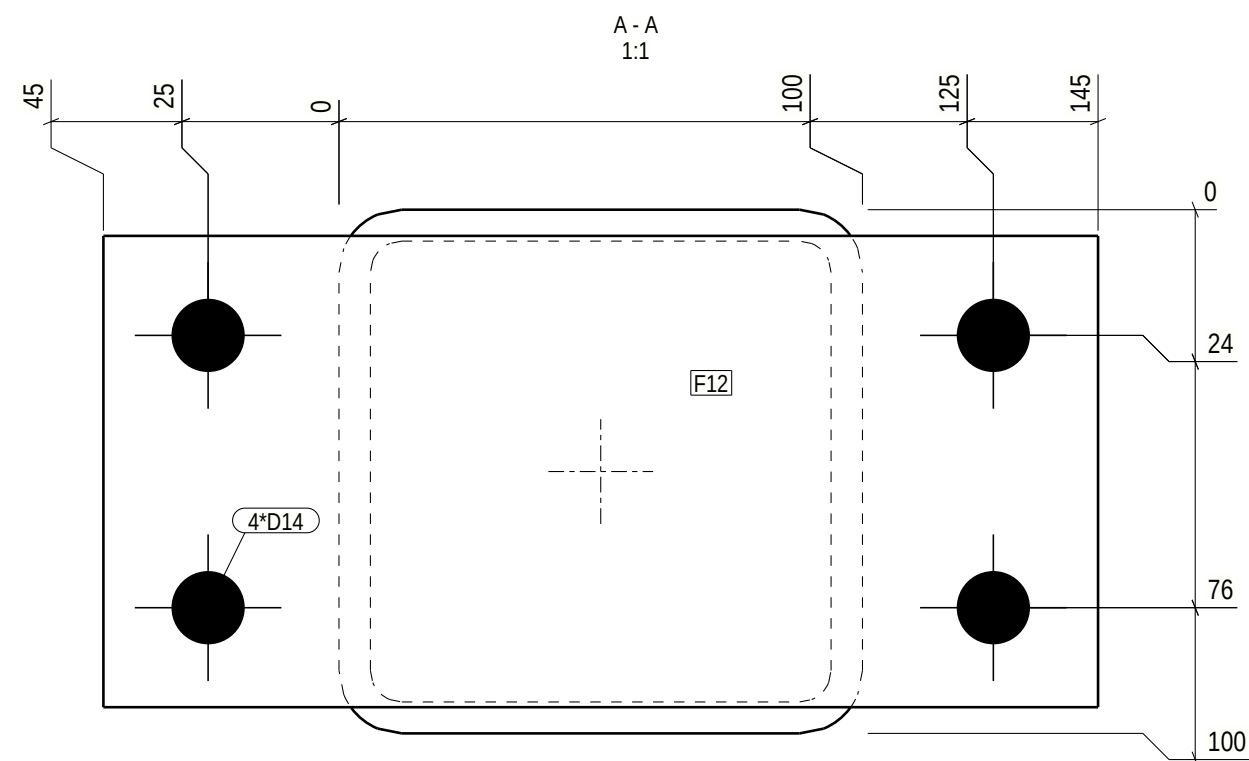

GENERAL NOTES:	For your safety, check weight before handling:		
	0-5kg Light	5-15kg Normal	15+kg Heavy

ALL WELDS ARE 4 UNLESS NOTED ON DRAWING

MATERIAL LIST FOR ASSEMBLY MK'D p.58 2 No. Required

Mark	Profile	Material	No.	Length	Area	Weight
p58	RHS100X100X6	S355J2H	1	5515	2.1	93.3 !!
F9	FL5*90	S355J2	1	90	0.0	0.3
F12	FL10*90	S355J2	1	190	0.0	1.3
Total					2.2	94.9

Finish Class
Standard

Surface treatment info:

 Thickness/start point--> length |

No



PHASE	QUANTITY
2	2

* o 3 0 4 8 0 - 2 *					 DS <i>Stalkonstruktion</i>					* A p 5 8 *				
PROJECT		Akkasæter Lager- og vedlikeholdshall						EXEC. CLASS			EXC 2			
MEMBER		Portomfatning			QUANTITY:		2		PROJECT No			30480-2		
REVISION		ISSUED: 07.11.2025			DRAFTER: BIM control:		ZLL		DRAWING No.			p.58		