
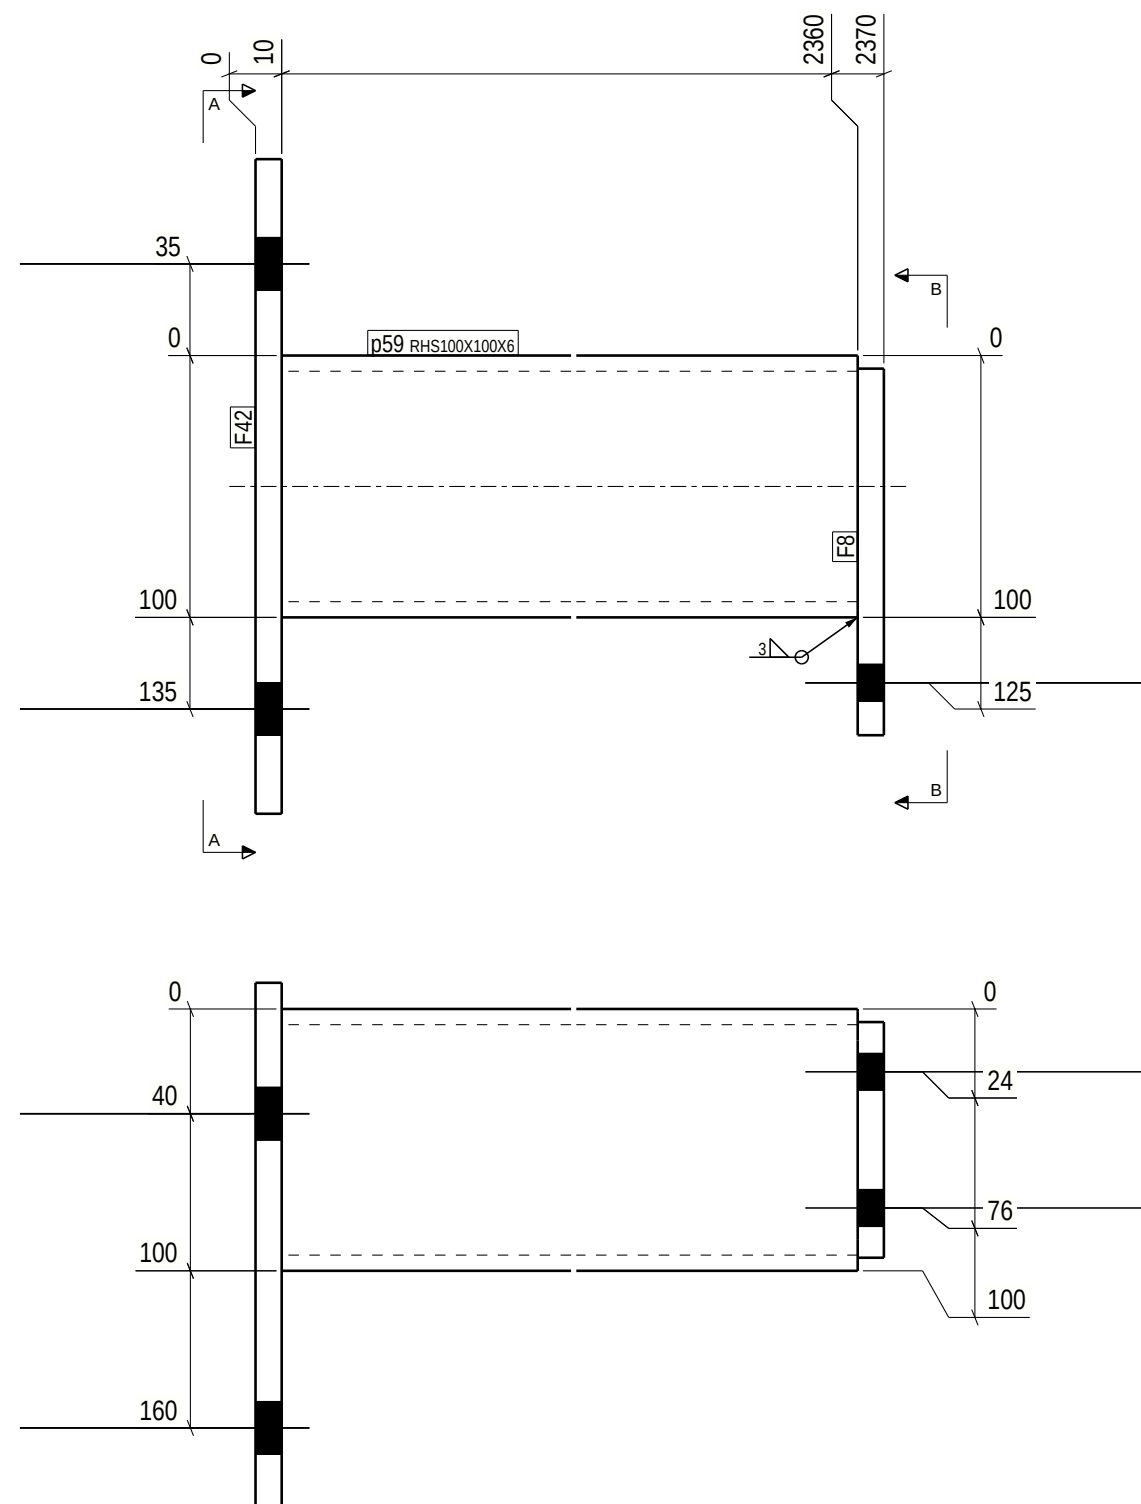


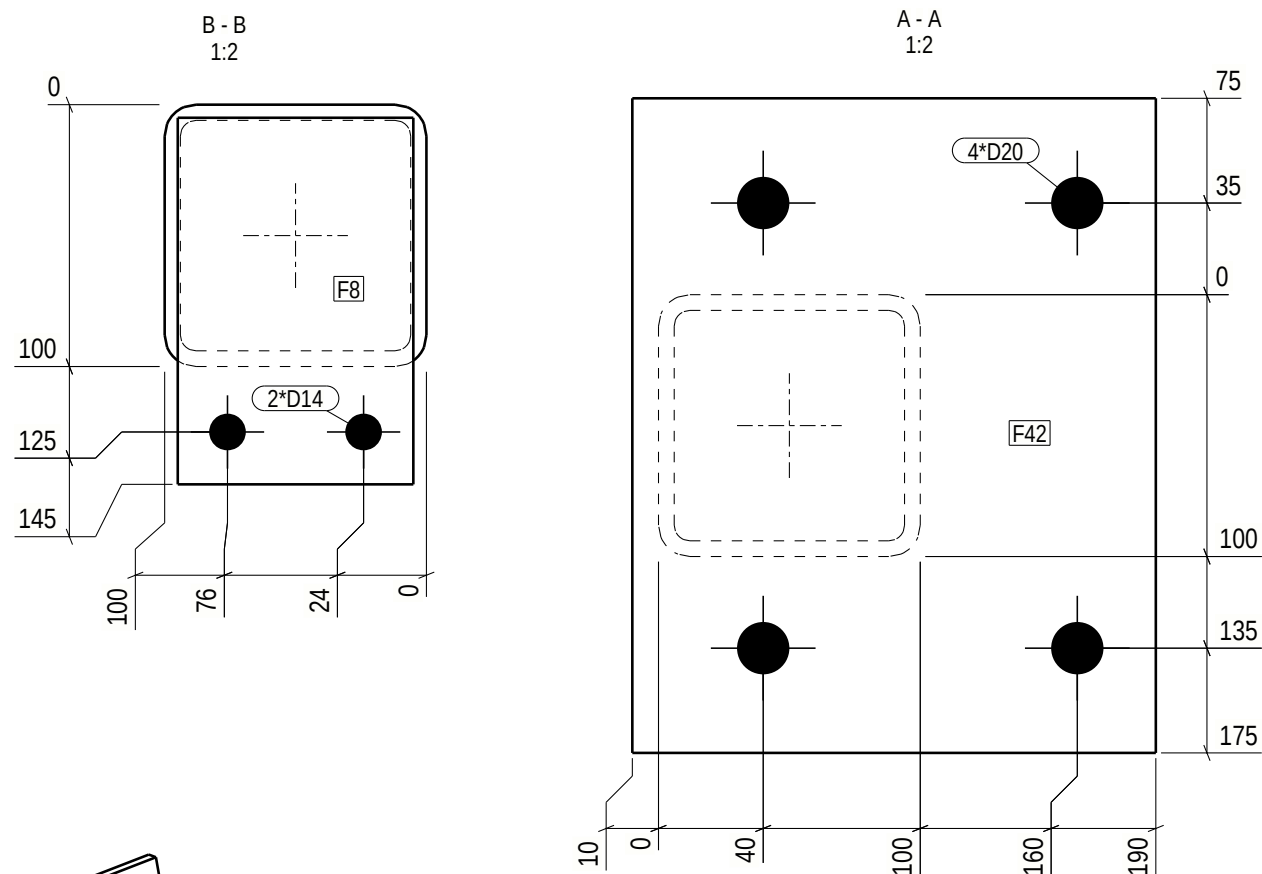

GENERAL NOTES: For your safety, check weight before handling:
0-5kg Light 5-15kg Normal 15+kg Heavy

ALL WELDS ARE 4 UNLESS NOTED ON DRAWING

MATERIAL LIST FOR ASSEMBLY MK'D **p.59** 2 No. Required

Mark	Profile	Material	No.	Length	Area	Weight
p59	RHS100X100X6	S355J2H	1	2350	0.9	39.7 !!
F8	FL10*90	S355J2	1	140	0.0	1.0
F42	FL10*200	S355J2	1	250	0.1	3.9
Total					1.0	44.7

Finish Class
Standard

Surface treatment info:	Thickness/start point-> length	No.
-------------------------	--------------------------------	-----

weld a = 4

PHASE	QUANTITY
2	2

* o 3 0 4 8 0 - 2 * DS Steelkonstruktion * A p 5 9 *			
PROJECT	Akkasæter Lager- og vedlikeholdshall	EXEC. CLASS	EXC 2
MEMBER	Portomfatning	QUANTITY:	2 PROJECT No 30480-2
REVISION	ISSUED: 07.11.2025	DRAFTER: ZLL SST	DRAWING No. p.59