
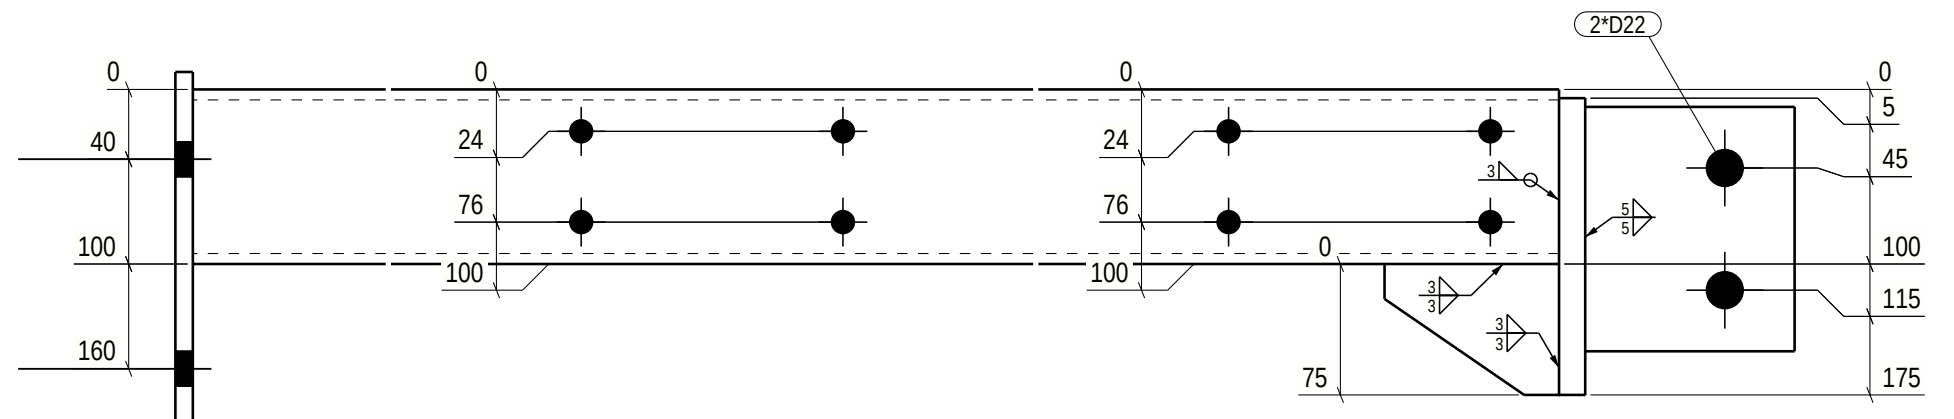
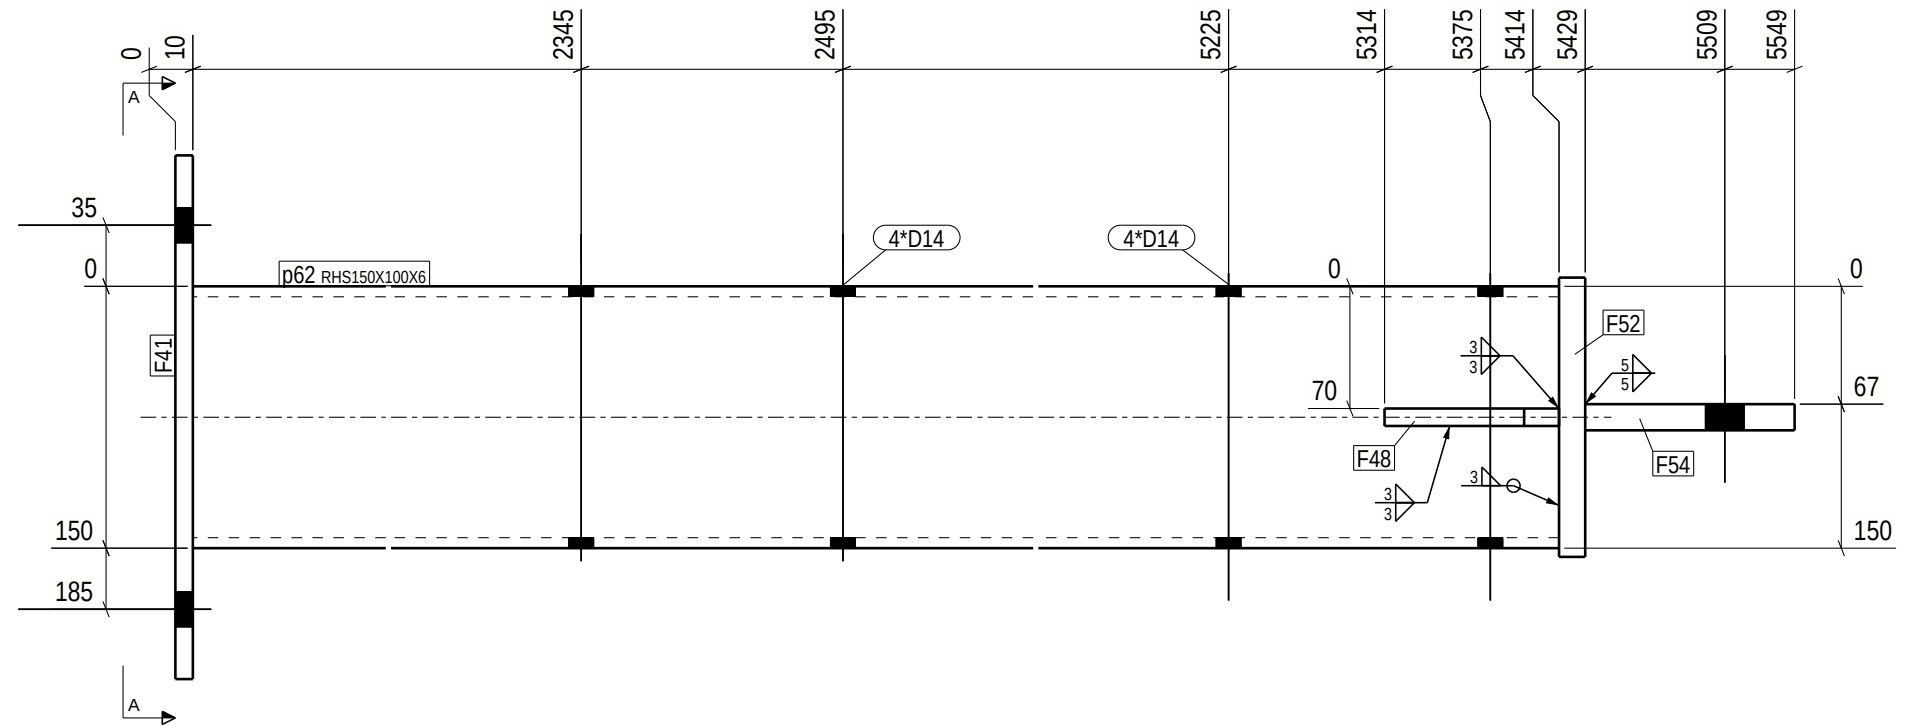


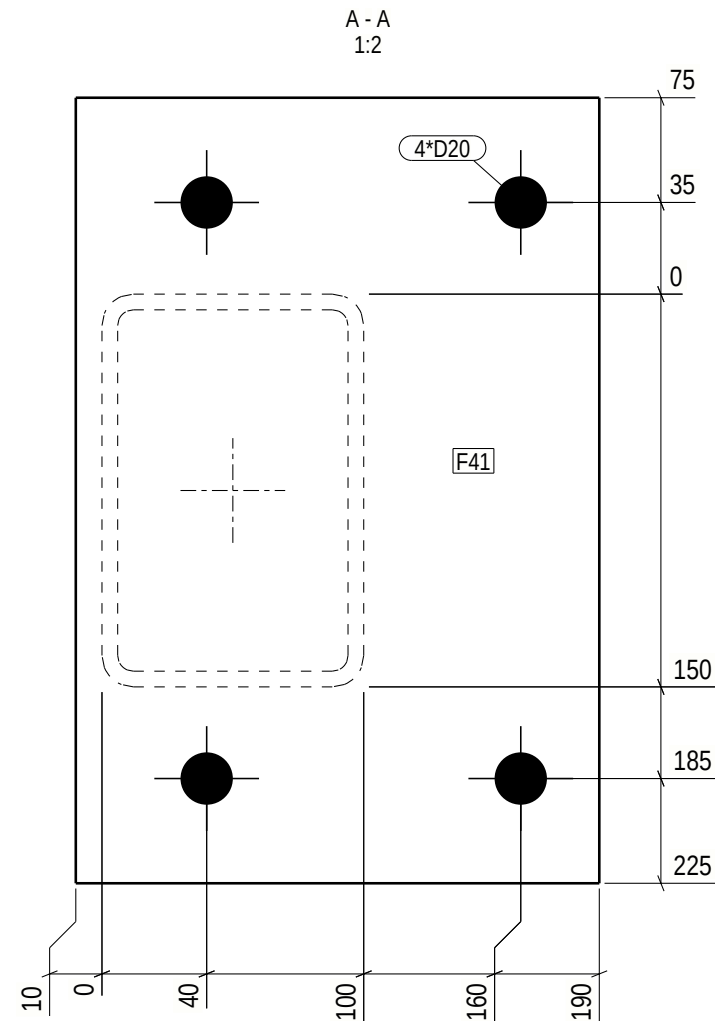

GENERAL NOTES: For your safety, check weight before handling:
0-5kg Light 5-15kg Normal 15+kg Heavy

ALL WELDS ARE 4 UNLESS NOTED ON DRAWING

MATERIAL LIST FOR ASSEMBLY MK'D p.62 2 No. Required

Mark	Profile	Material	No.	Length	Area	Weight
p62	RHS150X100X6	S355J2H	1	5404	2.6	116.9 !!
F41	FL10*200	S355J2	1	300	0.1	4.7
F48	FL10*75	S355J2	1	100	0.0	0.4
F52	FL15*160	S355J2	1	170	0.1	3.2
F54	FL15*120	S355J2	1	140	0.0	2.0
Total					2.8	127.2

Finish Class
Standard

Surface treatment info: Thickness/start point--> length No.

weld a = 4

PHASE	QUANTITY
2	2

* o 3 0 4 8 0 - 2 * DS Stalkonstruktion * A p 6 2 *			
PROJECT	Akkasæter Lager- og vedlikeholdshall	EXEC. CLASS	EXC 2
MEMBER	Portomfatning	QUANTITY:	2 PROJECT No 30480-2
REVISION	ISSUED: 07.11.2025	DRAFTER: ZLL	DRAWING No. p.62
		BIM control: SST	