
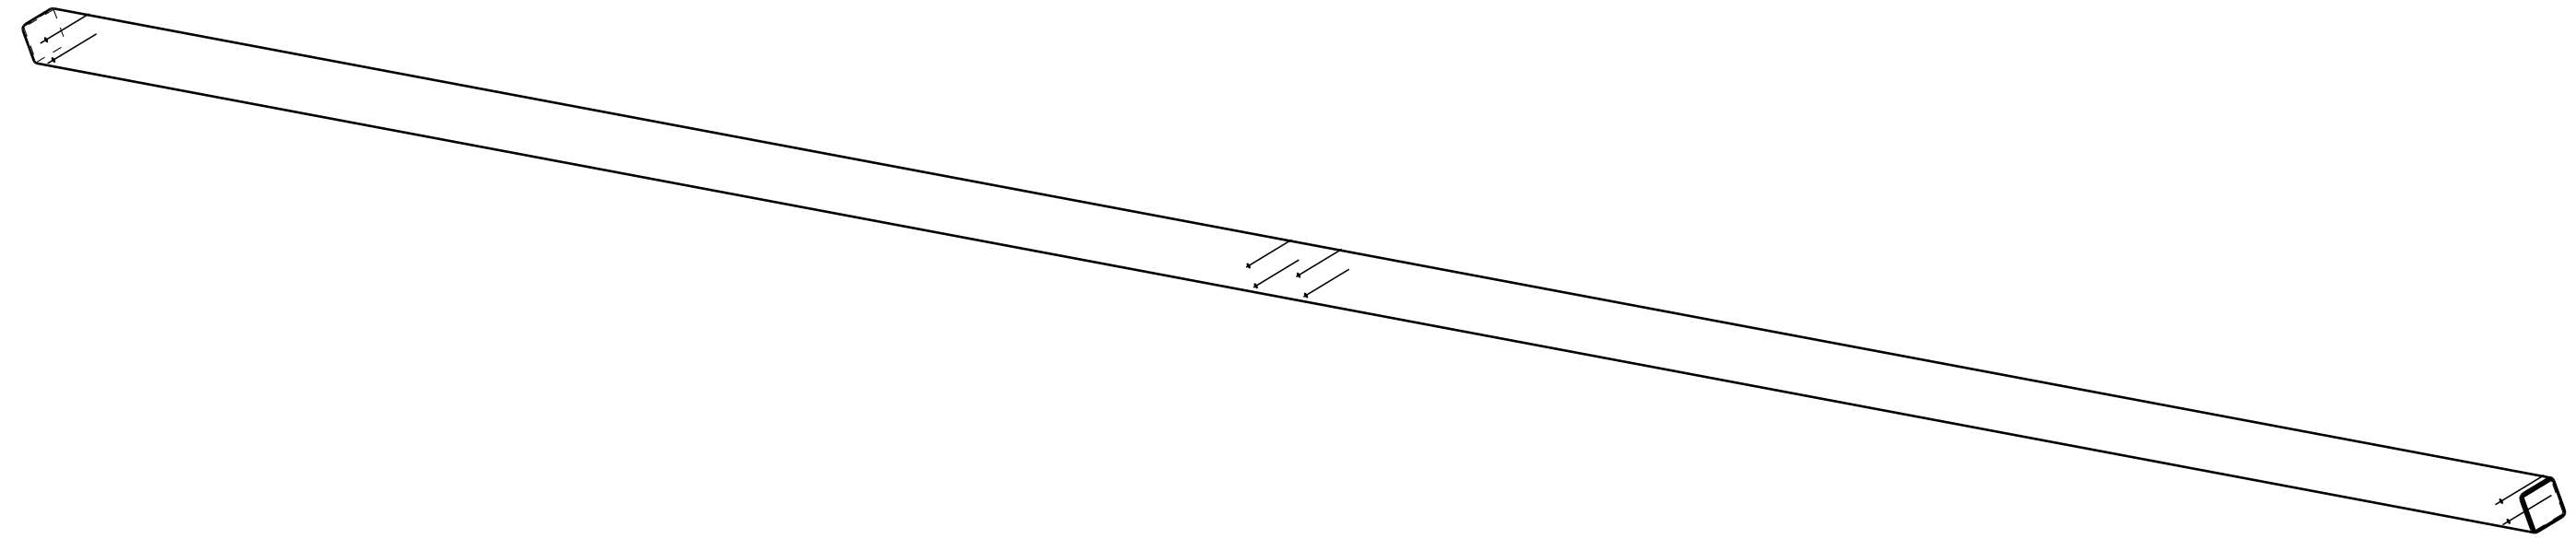
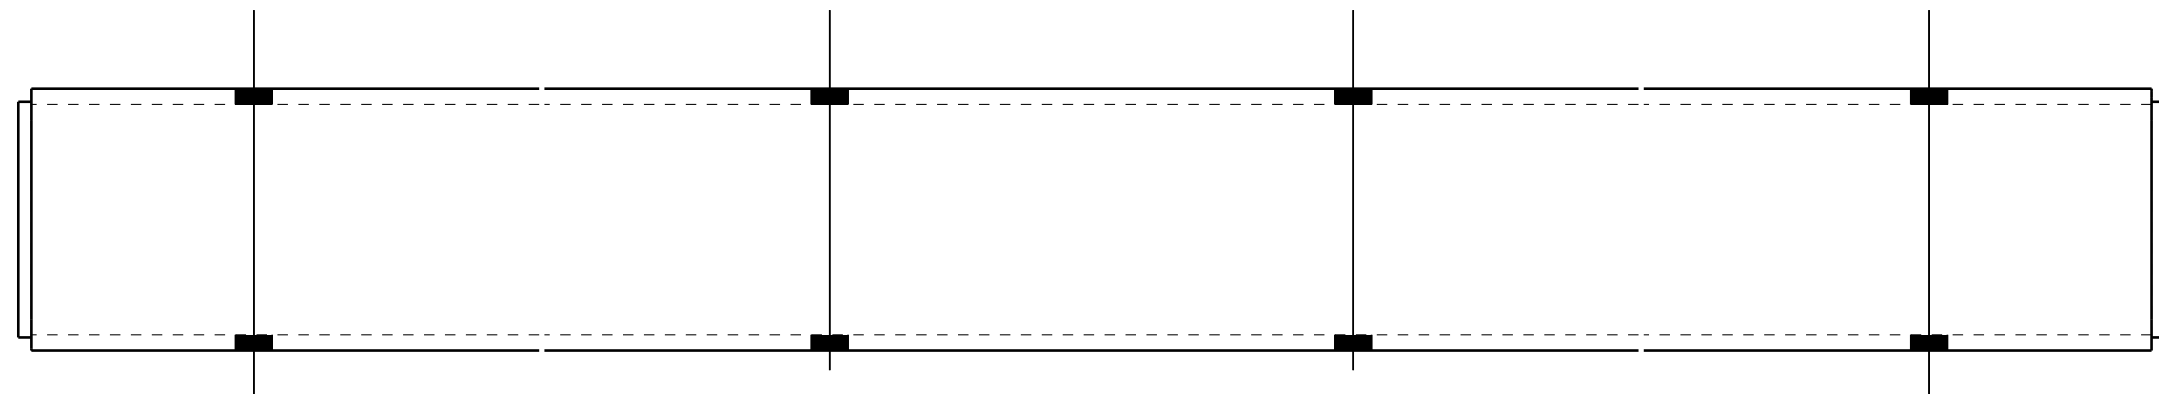


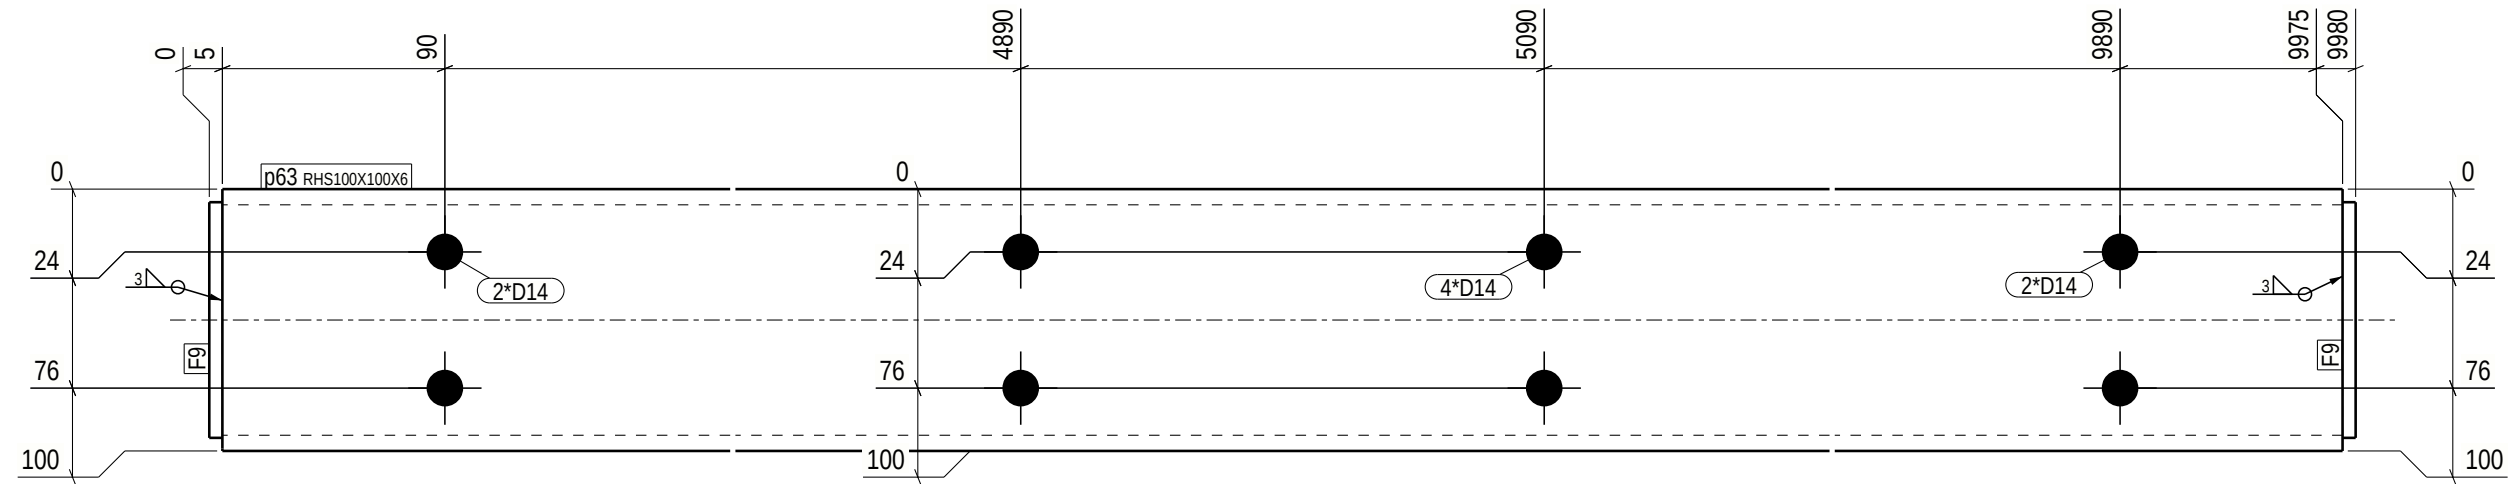

GENERAL NOTES: For your safety, check weight before handling:						
ALL WELDS ARE 4 UNLESS NOTED ON DRAWING						
MATERIAL LIST FOR ASSEMBLY MK'D p.63						
Mark	Profile	Material	No.	Length	Area	Weight
p63	RHS100X100X6	S355J2H	1	9970	3.8	168.6 !!
F9	FL5*90	S355J2	2	90	0.0	0.3
Total				3.9	169.3	

Finish Class
Standard

Surface treatment info:	Thickness/start point--> length	No.
-------------------------	---------------------------------	-----

weld a = 4

PHASE	QUANTITY
2	1

* o 3 0 4 8 0 - 2 *				DS Stalkonstruktion * A p 6 3 *			
PROJECT	Akkasæter Lager- og vedlikeholdshall			EXEC. CLASS	EXC 2		
MEMBER	Portomfatning			QUANTITY:	1	PROJECT No	30480-2
REVISION		ISSUED:	07.11.2025	DRAFTER:	ZLL	DRAWING No.	p.63
				BIM control:	SST		