
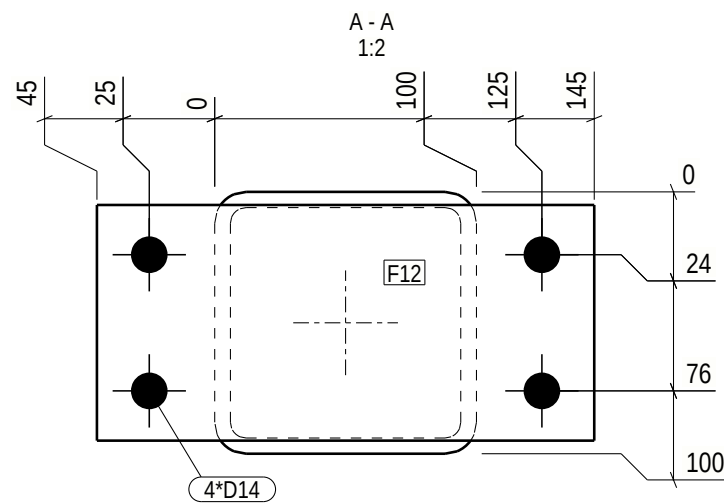
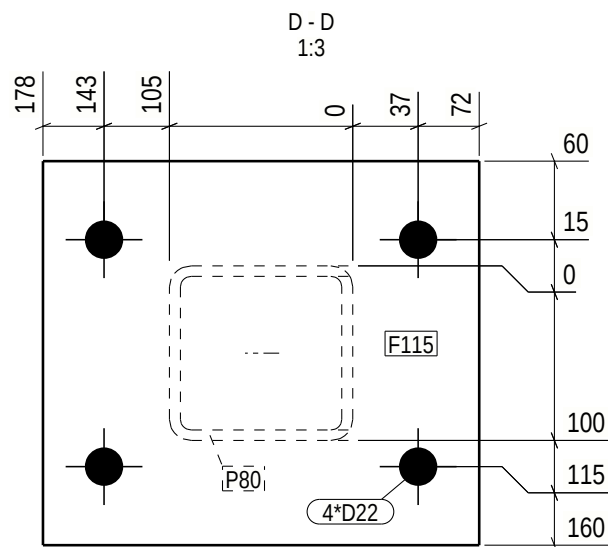


Tekla Structures

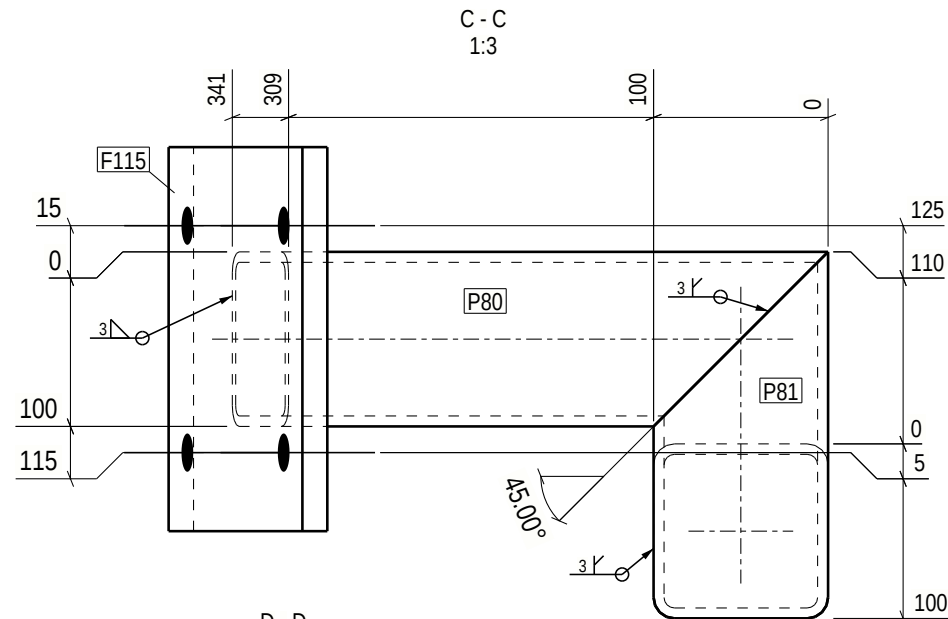

GENERAL NOTES: For your safety, check weight before handling:
0-5kg Light 5-15kg Normal 15+kg Heavy





ALL WELDS ARE 4 UNLESS NOTED ON DRAWING

MATERIAL LIST FOR ASSEMBLY MK'D **p.66** **1** No. Required

Mark	Profile	Material	No.	Length	Area	Weight
p66	RHS100X100X6	S355J2H	1	2965	1.1	49.3 !!
C35	PL6*60	S355J2	2	60	0.0	0.2
F12	FL10*90	S355J2	1	190	0.0	1.3
F115	FL15*220	S355J2	1	250	0.1	6.5
P80	RHS100X100X6	S355J2H	1	341	0.1	4.7
P81	RHS100X100X6	S355J2H	1	210	0.0	1.9
Total					1.5	64.0

Finish Class
Standard

Surface treatment info: Thickness/start point-> length No.

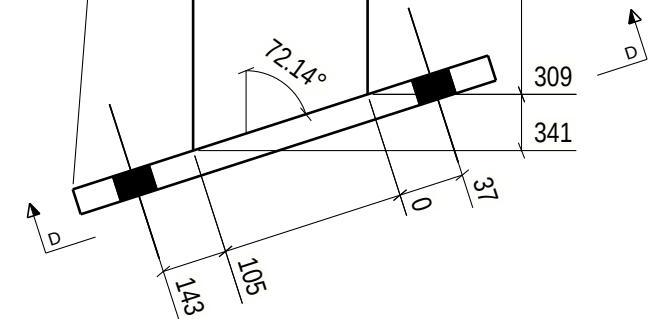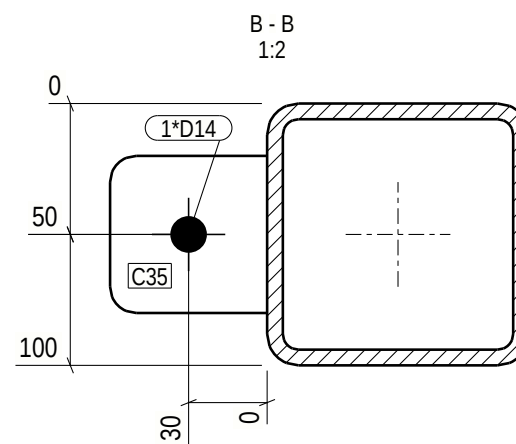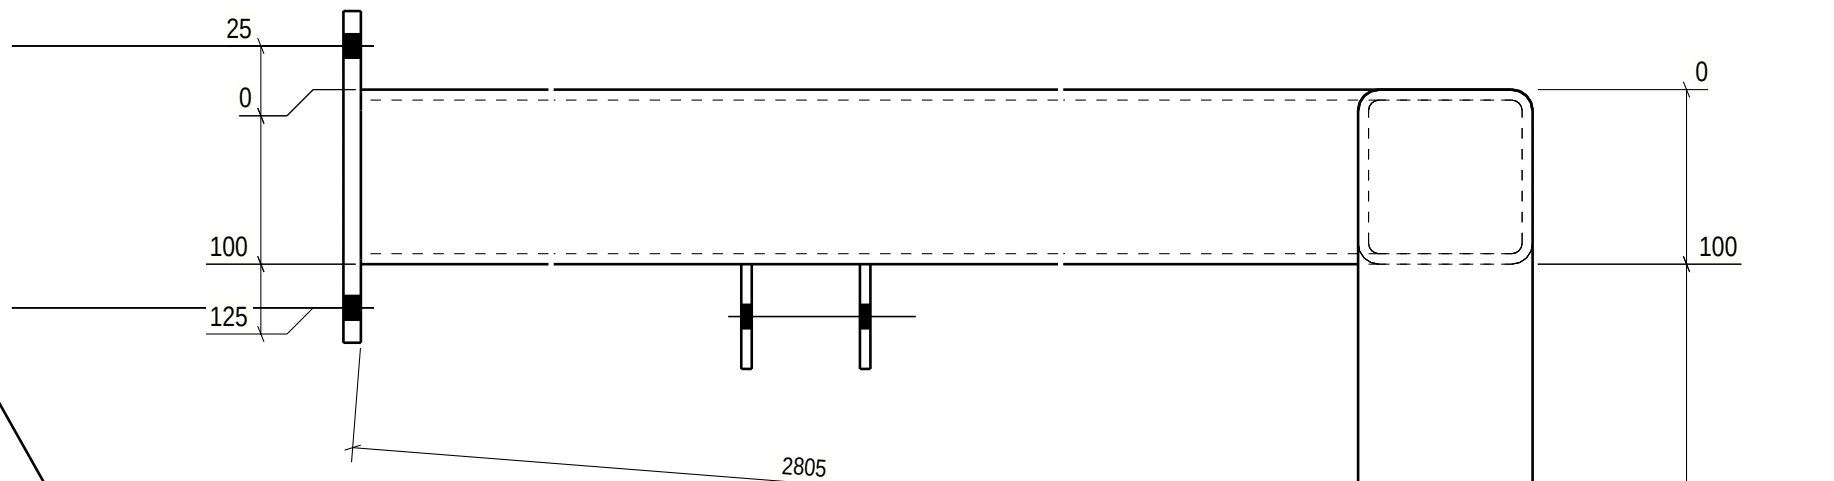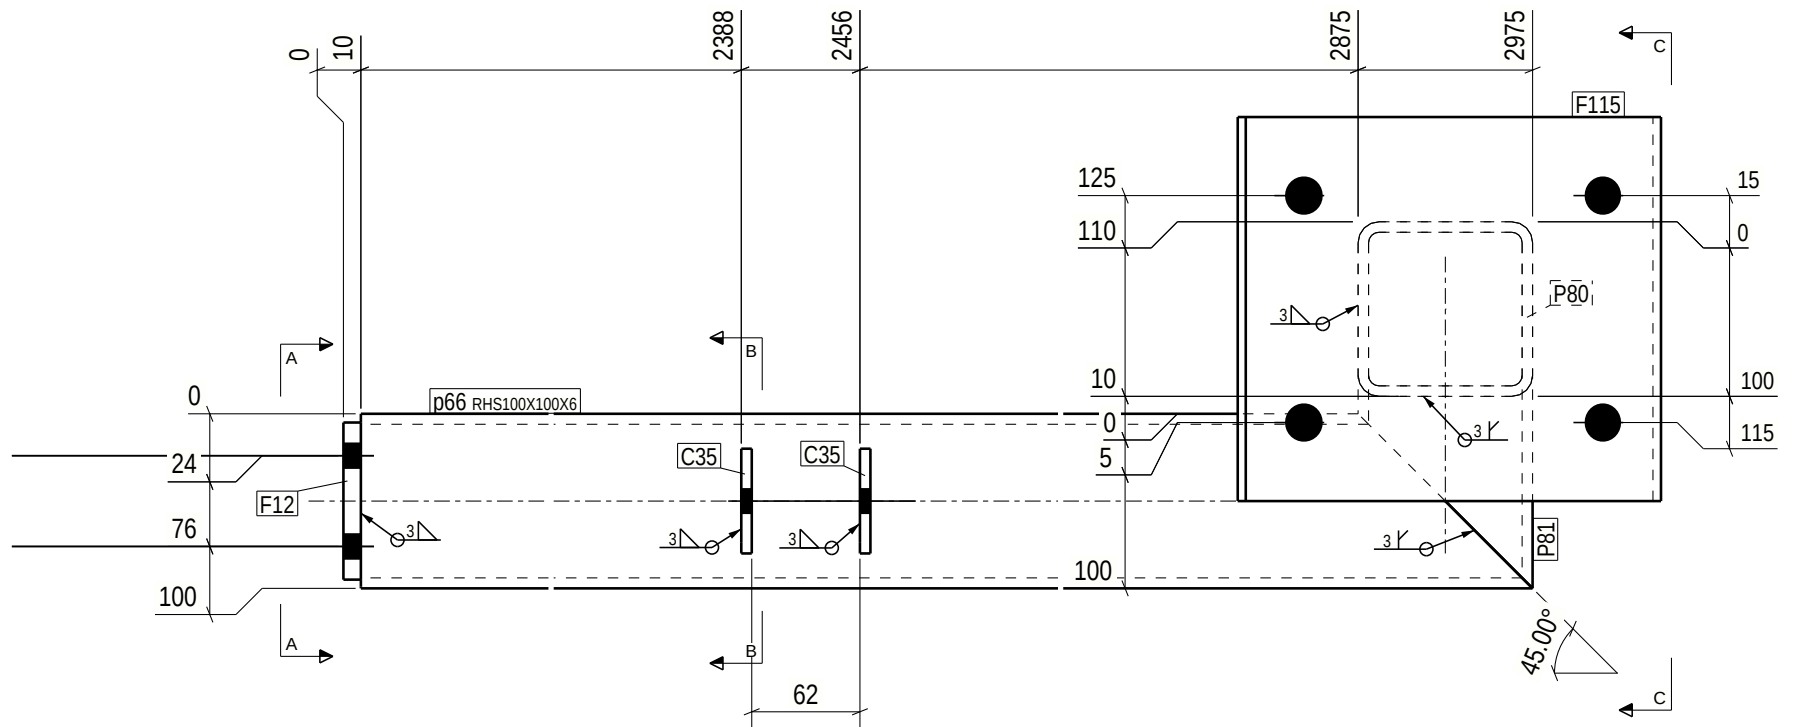

weld a = 4

PHASE	QUANTITY
2	1

* o 3 0 4 8 0 - 2 *  DS <i>Stålkonstruktion</i> * A p 6 6 *			
PROJECT	Akkasæter Lager- og vedlikeholdshall	EXEC. CLASS	EXC 2
MEMBER	Portomfatning	QUANTITY:	1 PROJECT No 30480-2
REVISION	ISSUED: 07.11.2025	DRAFTER: ZLL SST	DRAWING No. p.66