
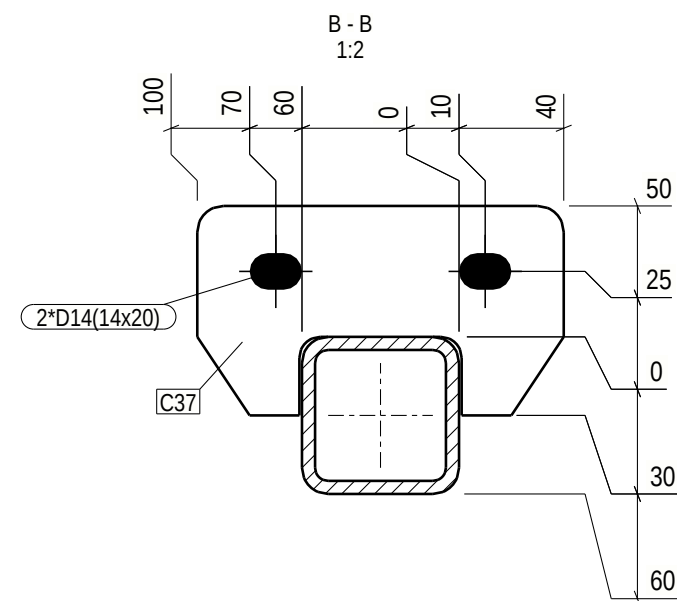
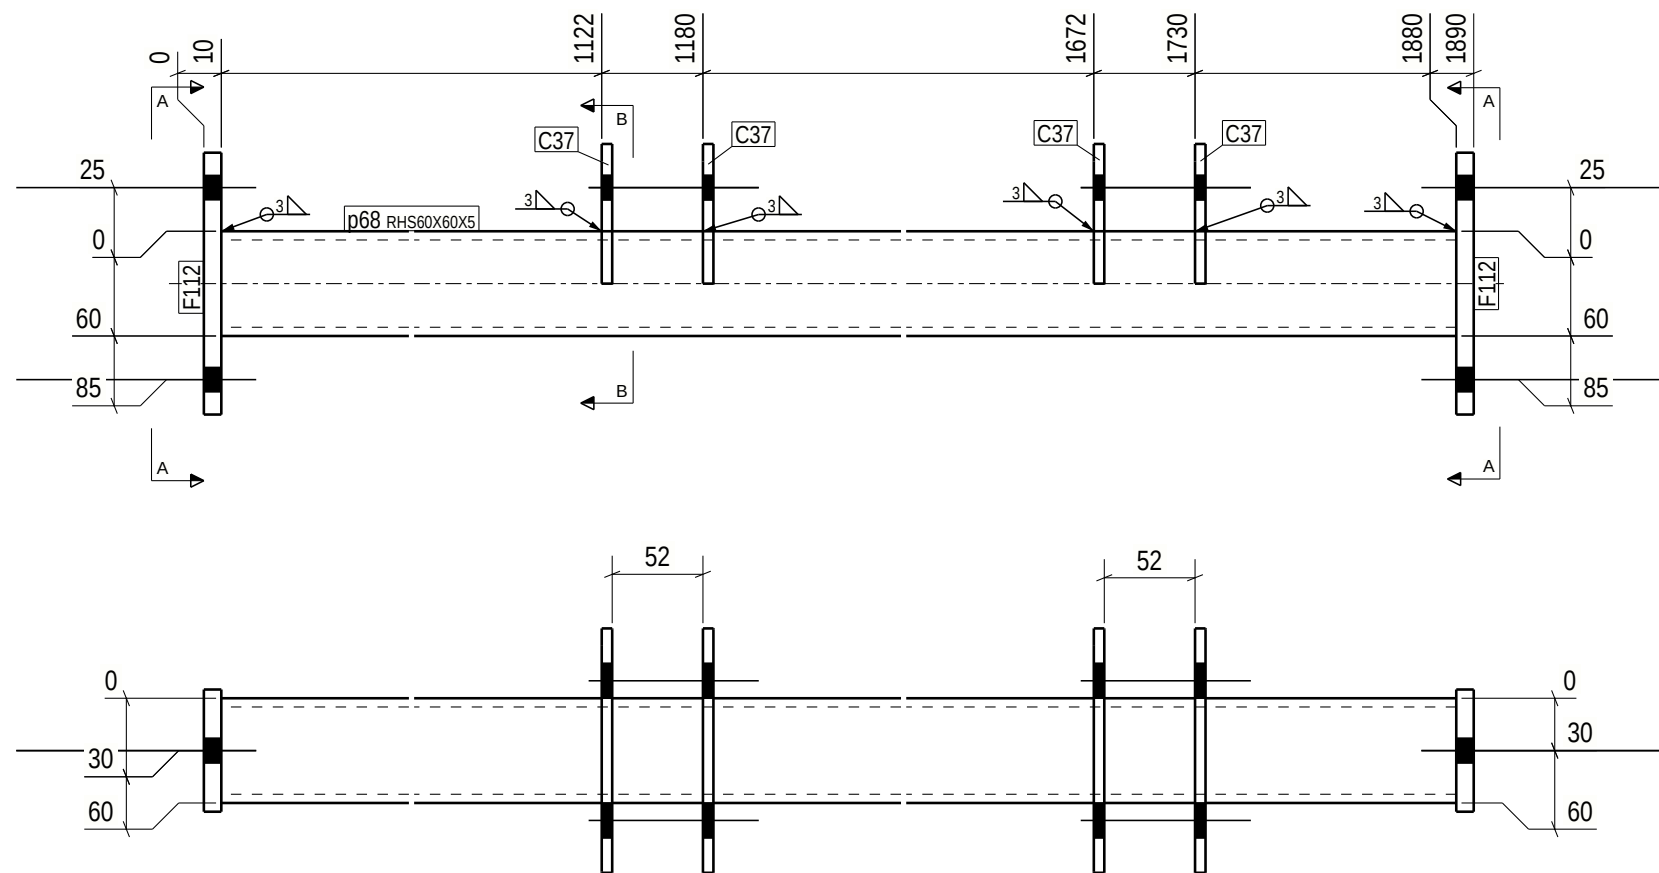


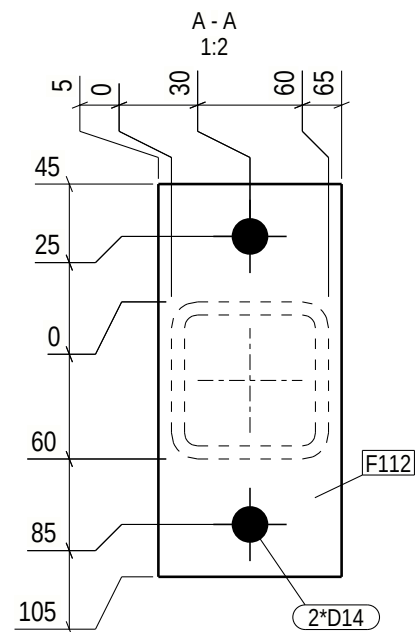

GENERAL NOTES: For your safety, check weight before handling:
0-5kg Light 5-15kg Normal 15+kg Heavy

ALL WELDS ARE 4 UNLESS NOTED ON DRAWING

MATERIAL LIST FOR ASSEMBLY MK'D **p.68** **3** No. Required

Mark	Profile	Material	No.	Length	Area	Weight
p68	RHS60X60X5	S355J2H	1	1870	0.4	15.1 !!
C37	PL6*80	S355J2	4	140	0.0	0.4
F112	FL10*70	S355J2	2	150	0.0	0.8
Total					0.6	18.4

Finish Class
Standard

Surface treatment info: Thickness/start point-> length No.

weld a = 4

PHASE	QUANTITY
2	3

* o 3 0 4 8 0 - 2 * DS <i>Stalkonstruktion</i> * A p 6 8 *			
PROJECT	Akkasæter Lager- og vedlikeholdshall		EXEC. CLASS
MEMBER	Portomfatning	QUANTITY:	3
REVISION	ISSUED: 07.11.2025	DRAFTER: ZLL	PROJECT No. 30480-2
		BIM control: SST	DRAWING No. p.68