
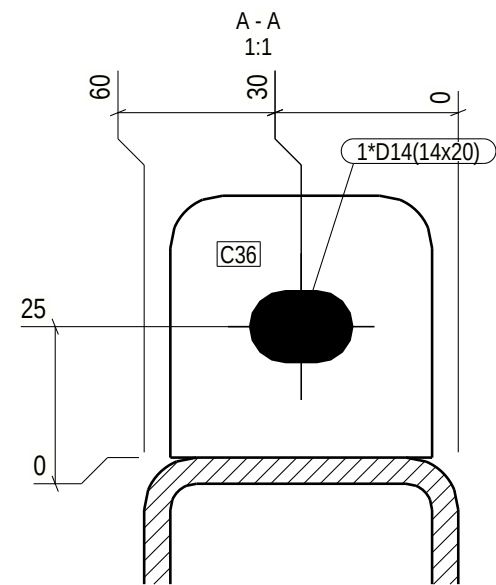
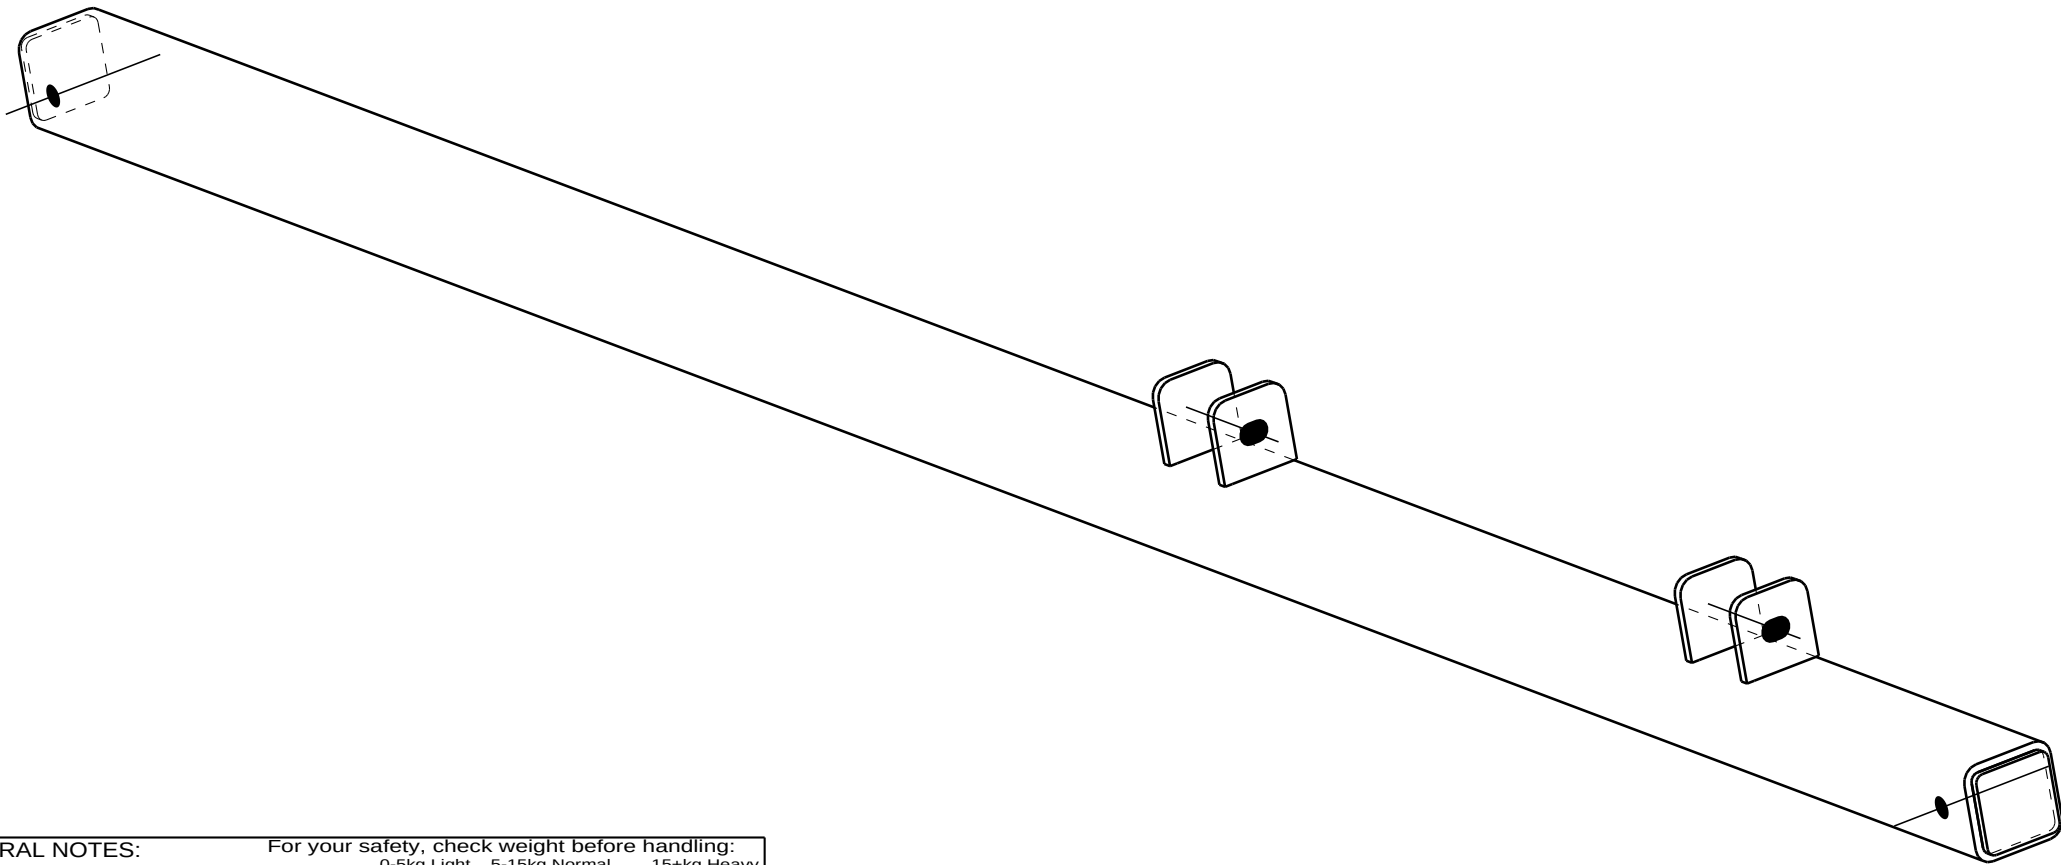


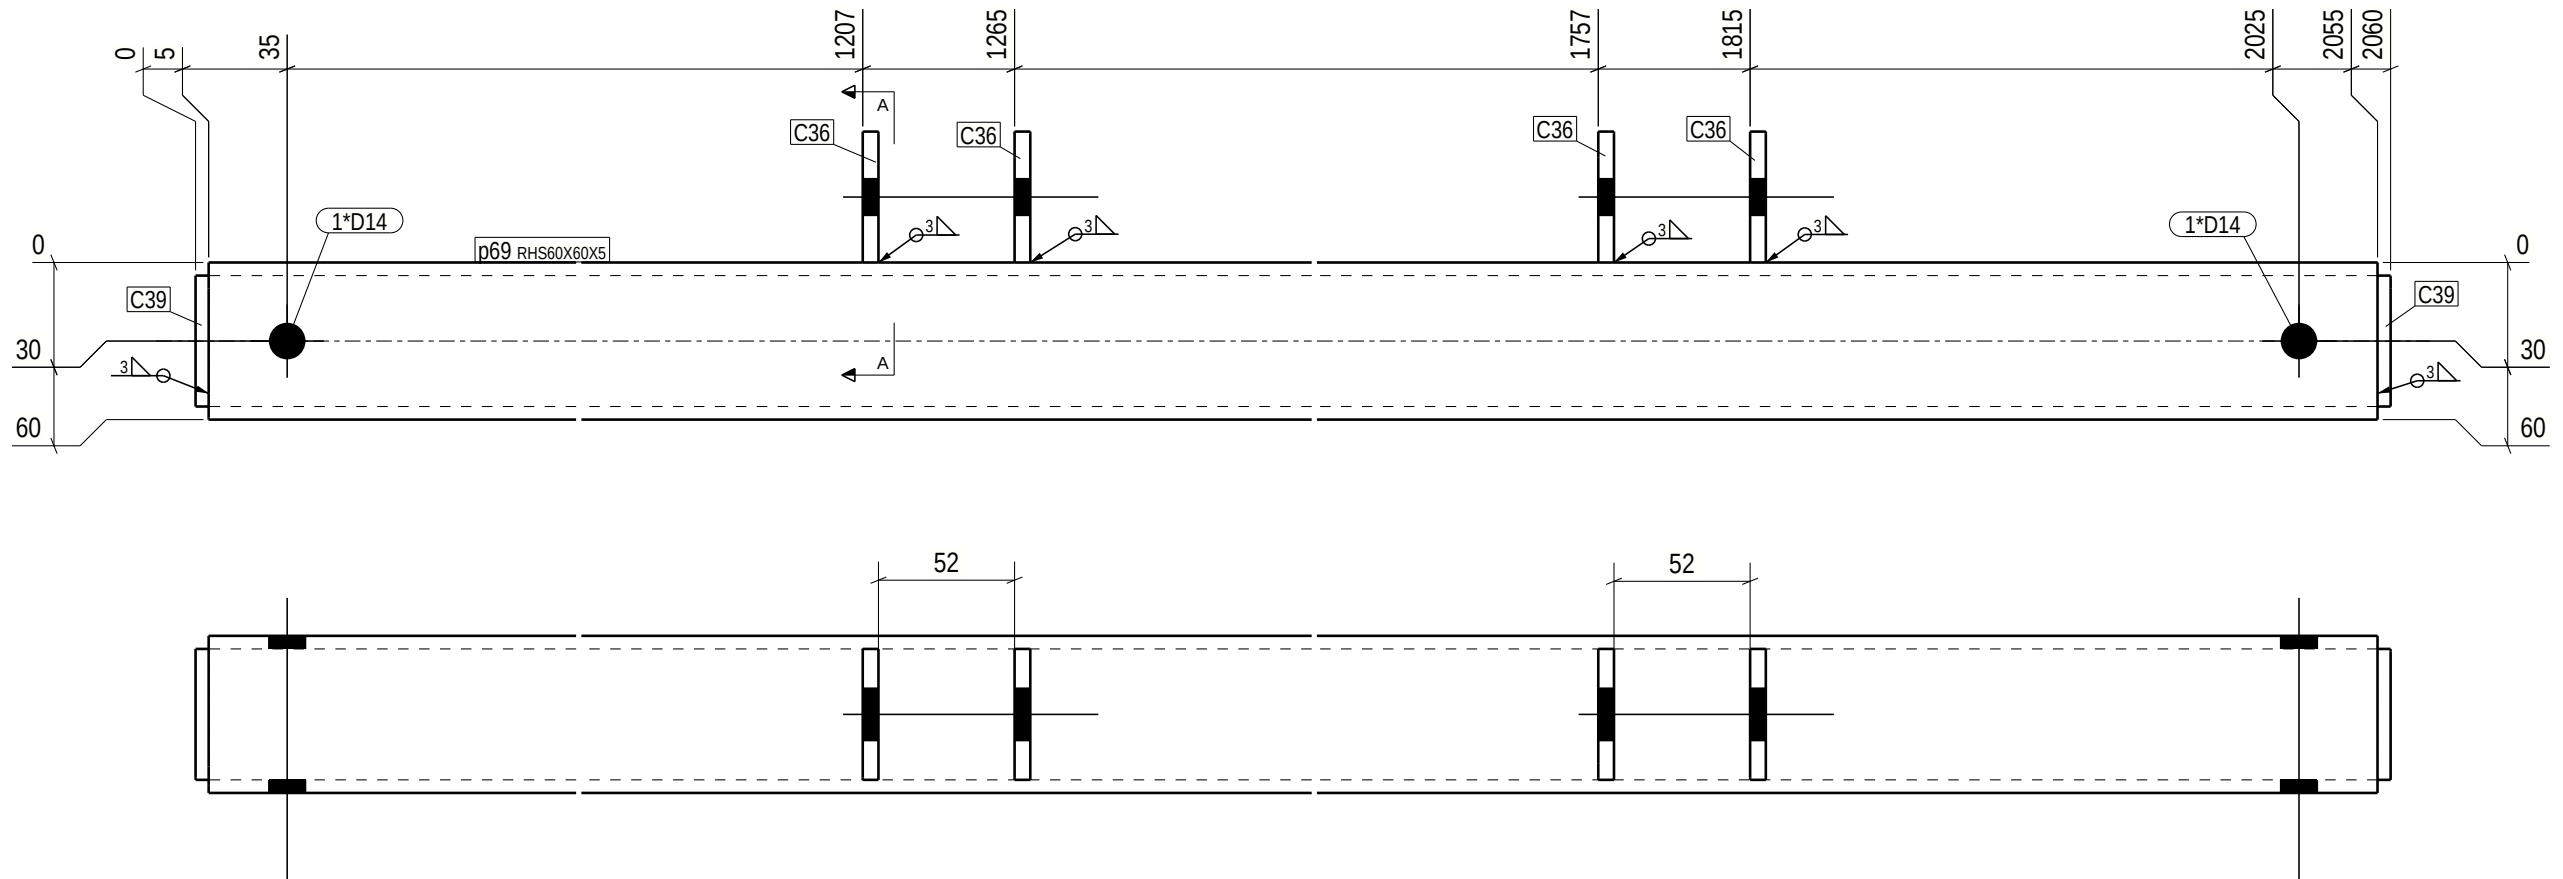

|                                                     |            |          |     |        |      |         |
|-----------------------------------------------------|------------|----------|-----|--------|------|---------|
| GENERAL NOTES:                                      |            |          |     |        |      |         |
| For your safety, check weight before handling:      |            |          |     |        |      |         |
| 0-5kg Light 5-15kg Normal 15+kg Heavy               |            |          |     |        |      |         |
| ALL WELDS ARE 4 UNLESS NOTED ON DRAWING             |            |          |     |        |      |         |
| MATERIAL LIST FOR ASSEMBLY MK'D p.69 4 No. Required |            |          |     |        |      |         |
| Mark                                                | Profile    | Material | No. | Length | Area | Weight  |
| p69                                                 | RHS60X60X5 | S355J2H  | 1   | 2050   | 0.5  | 16.6 !! |
| C36                                                 | PL6*50     | S355J2   | 4   | 50     | 0.0  | 0.1     |
| C39                                                 | FL5*50     | S355J2   | 2   | 50     | 0.0  | 0.1     |
| Total                                               |            |          |     |        | 0.5  | 17.2    |

Finish Class  
Standard

|                         |                                |     |
|-------------------------|--------------------------------|-----|
| Surface treatment info: | Thickness/start point-> length | No. |
|-------------------------|--------------------------------|-----|

weld a = 4

|       |          |
|-------|----------|
| PHASE | QUANTITY |
| 2     | 4        |

|                                                     |                                      |              |                  |             |         |
|-----------------------------------------------------|--------------------------------------|--------------|------------------|-------------|---------|
| * o 3 0 4 8 0 - 2 * DS Stalkonstruktion * A p 6 9 * |                                      |              |                  |             |         |
| PROJECT                                             | Akkasæter Lager- og vedlikeholdshall |              |                  | EXEC. CLASS | EXC 2   |
| MEMBER                                              | Portomfatning                        | QUANTITY:    | 4                | PROJECT No  | 30480-2 |
| REVISION                                            | ISSUED: 07.11.2025                   | DRAFTER: ZLL | BIM control: SST | DRAWING No. | p.69    |