
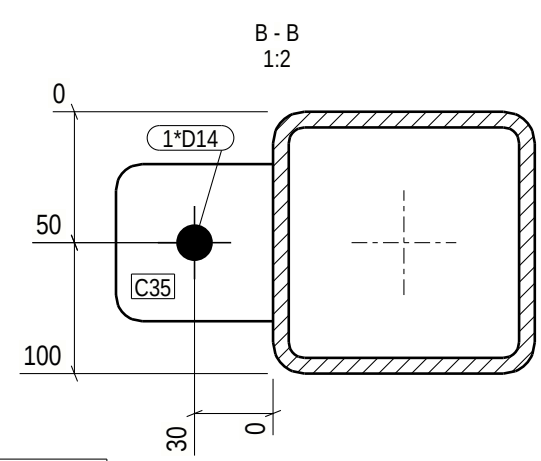
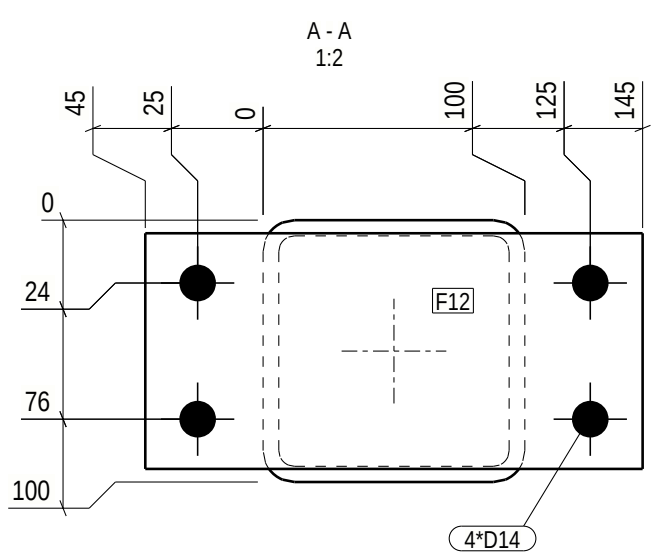
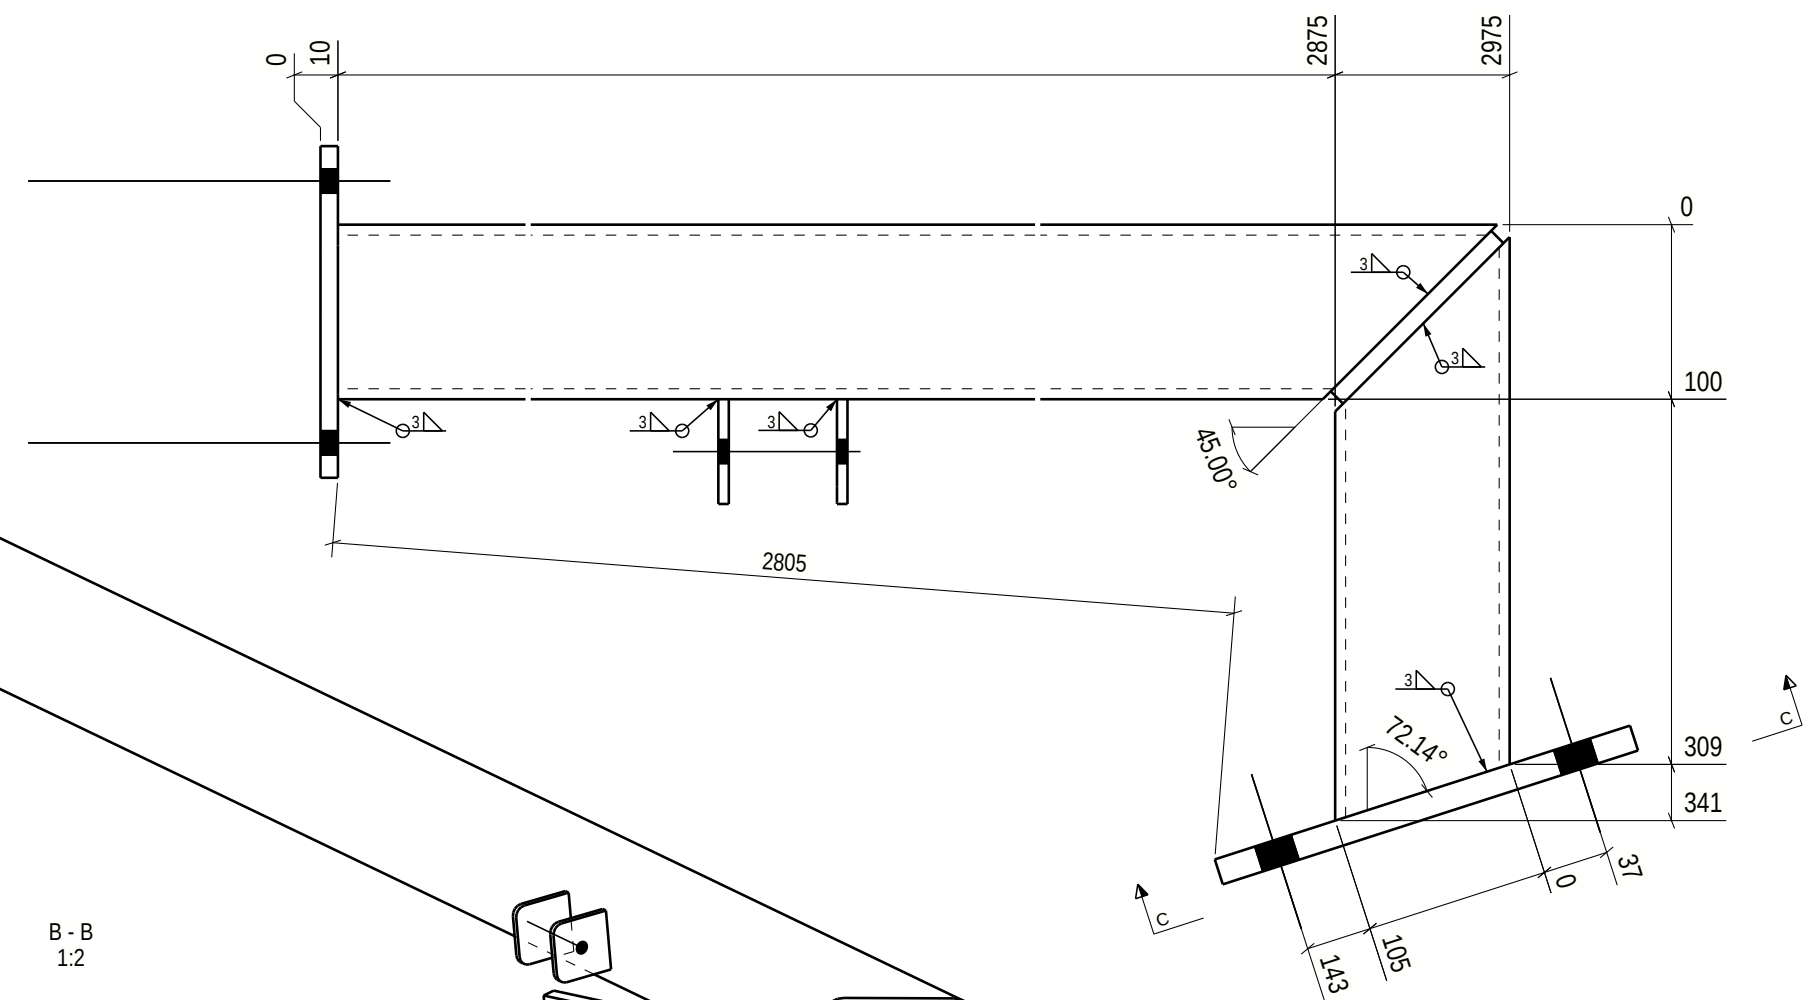
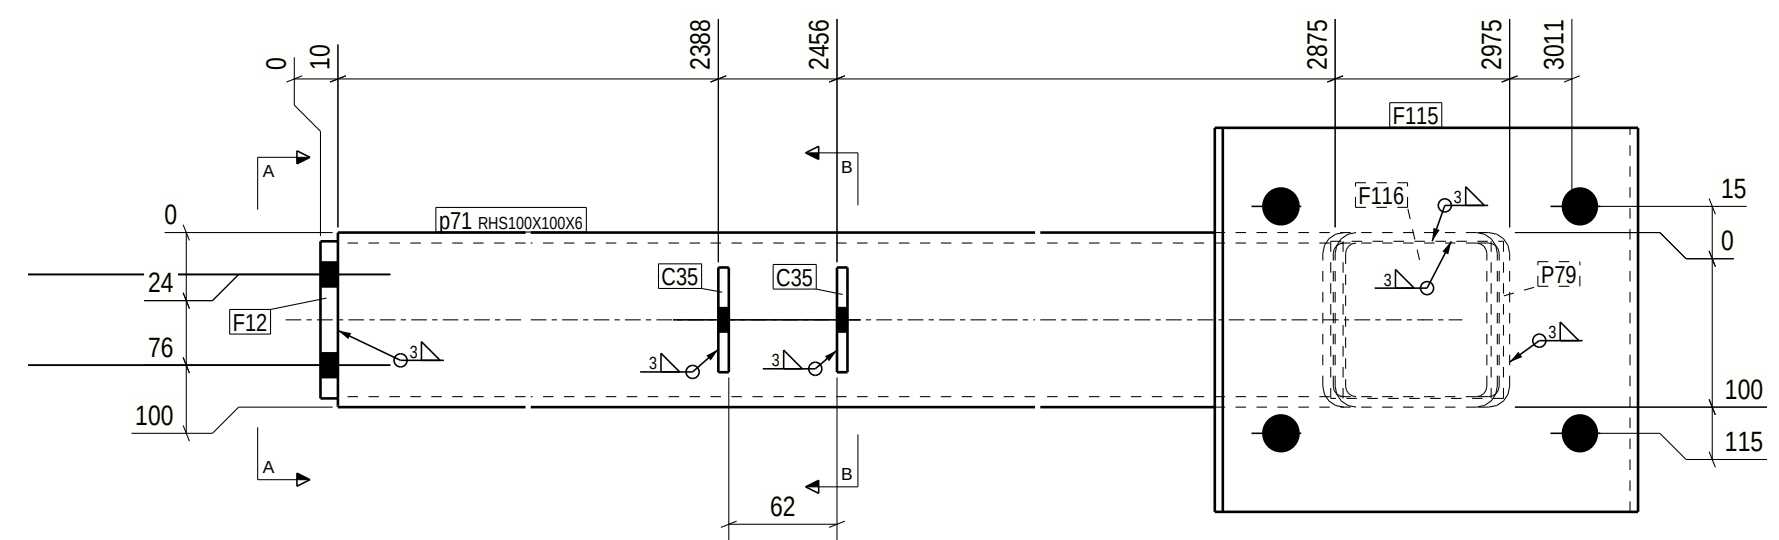


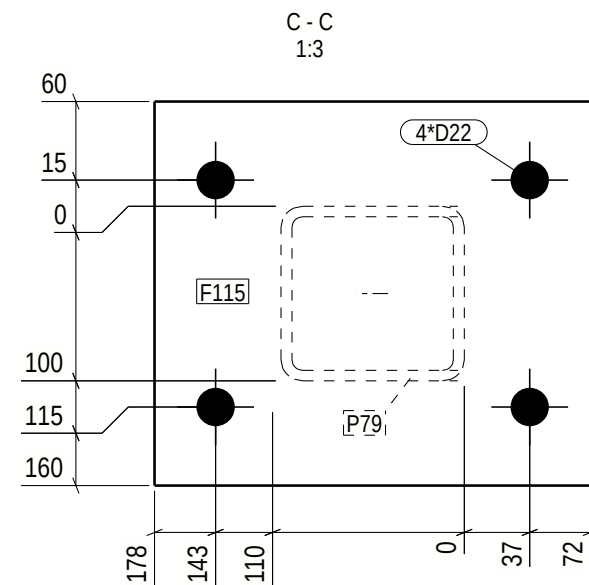

GENERAL NOTES: For your safety, check weight before handling:
0-5kg Light 5-15kg Normal 15+kg Heavy

ALL WELDS ARE 4 UNLESS NOTED ON DRAWING

MATERIAL LIST FOR ASSEMBLY MK'D p.71

Mark	Profile	Material	No.	Length	Area	Weight
p71	RHS100X100X6	S355J2H	1	2958	1.1	49.2 !!
C35	PL6*60	S355J2	2	60	0.0	0.2
F12	FL10*90	S355J2	1	190	0.0	1.3
F115	FL15*220	S355J2	1	250	0.1	6.5
F116	FL10*90	S355J2	1	130	0.0	0.9
P79	RHS100X100X6	S355J2H	1	334	0.1	4.5
Total					1.4	62.8

Finish Class Standard

Surface treatment info: Thickness/start point-> length No.

weld a = 4

PHASE	QUANTITY
2	2

* o 3 0 4 8 0 - 2 * DS Steelkonstruktion * A p 7 1 *			
PROJECT	Akkasæter Lager- og vedlikeholdshall	EXEC. CLASS	EXC 2
MEMBER	Portomfatning	QUANTITY:	2 PROJECT No 30480-2
REVISION	ISSUED: 07.11.2025	DRAFTER: ZLL SST	DRAWING No. p.71