
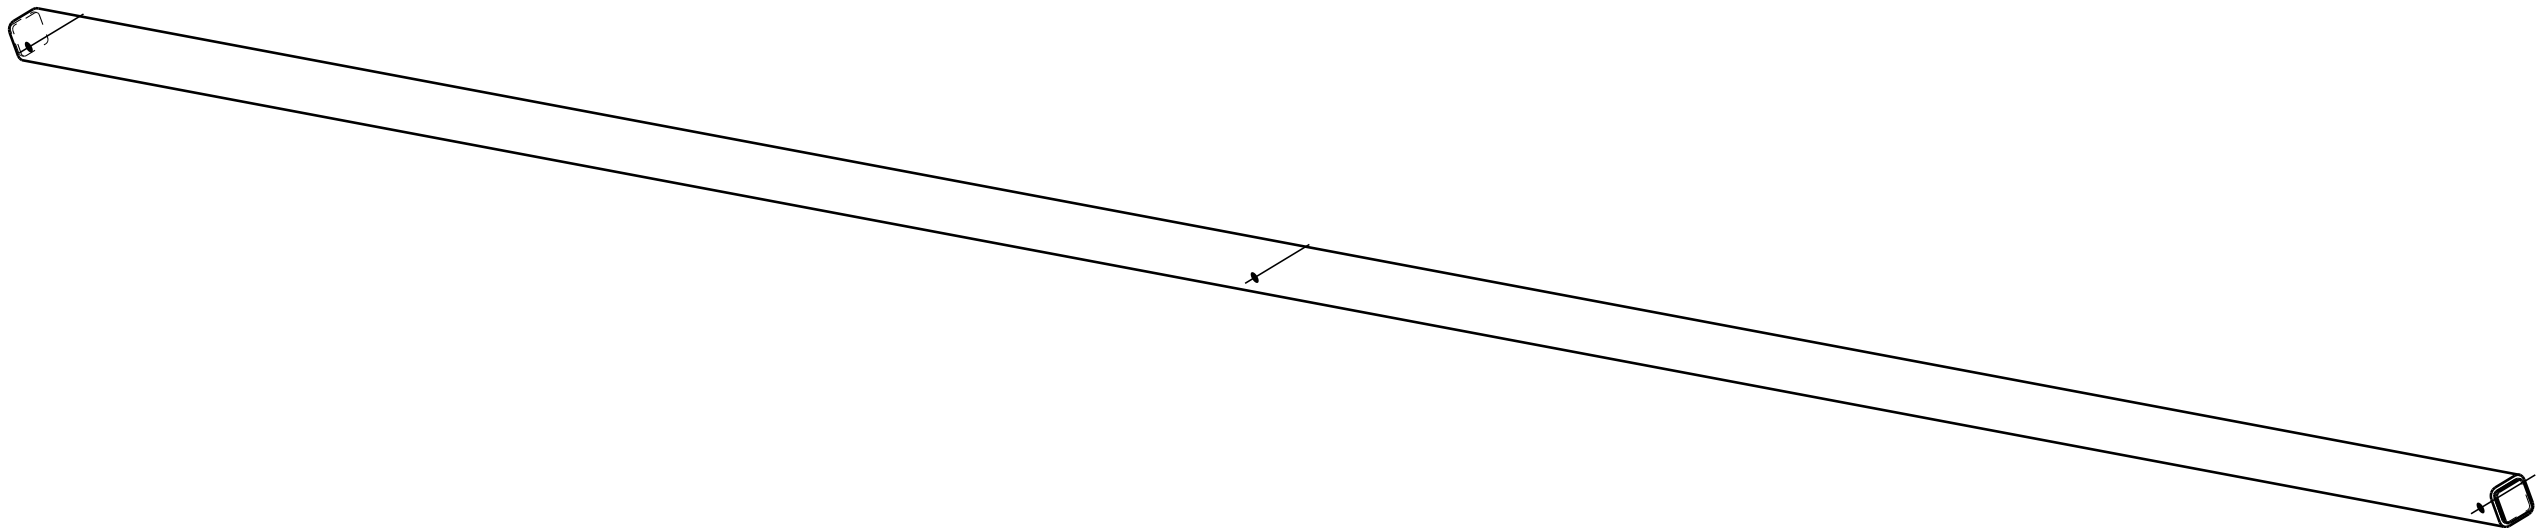
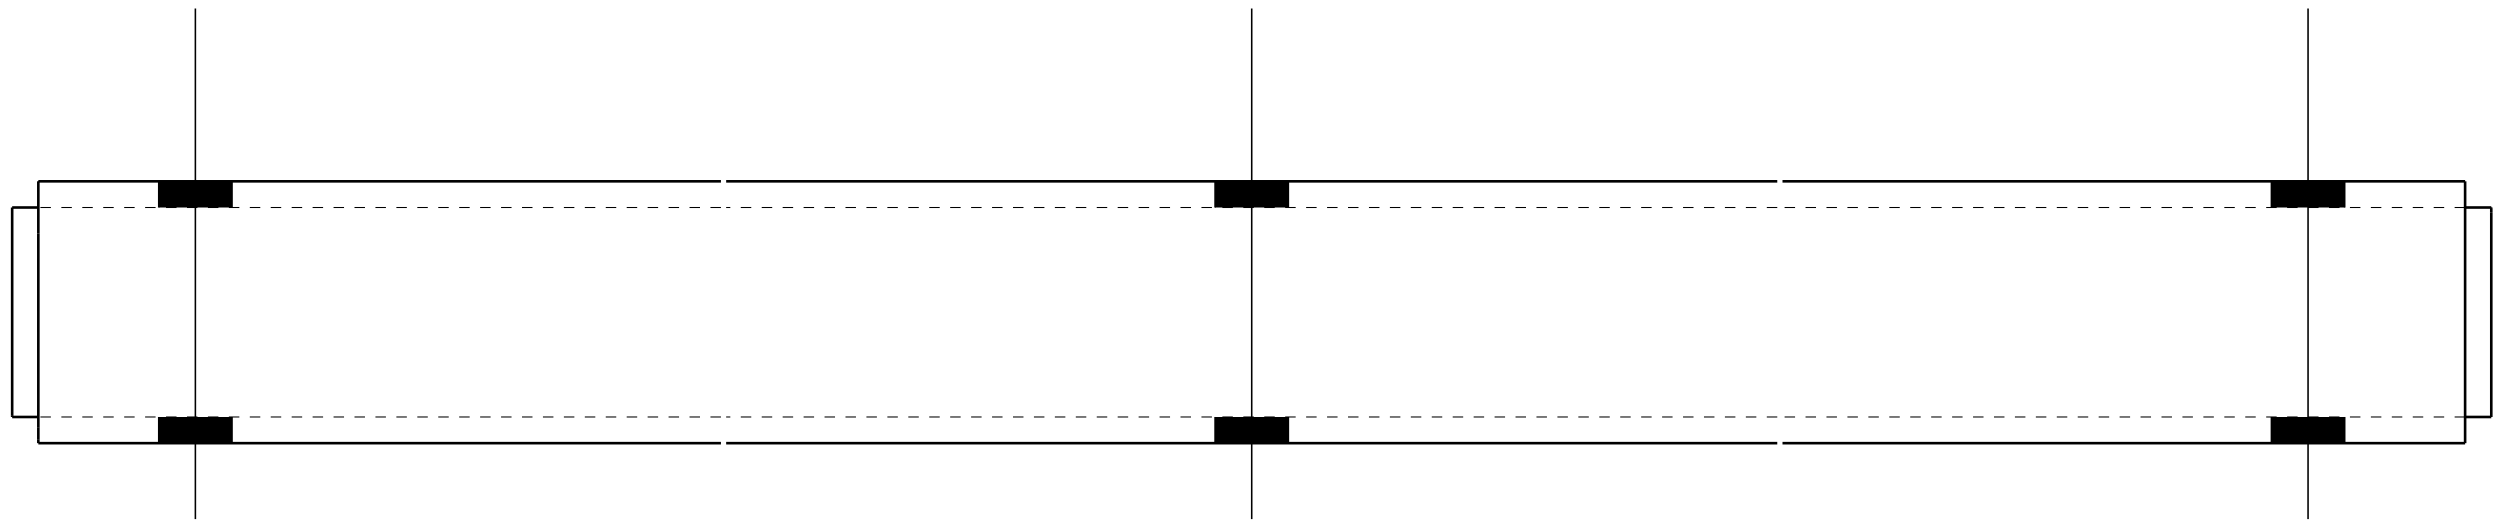


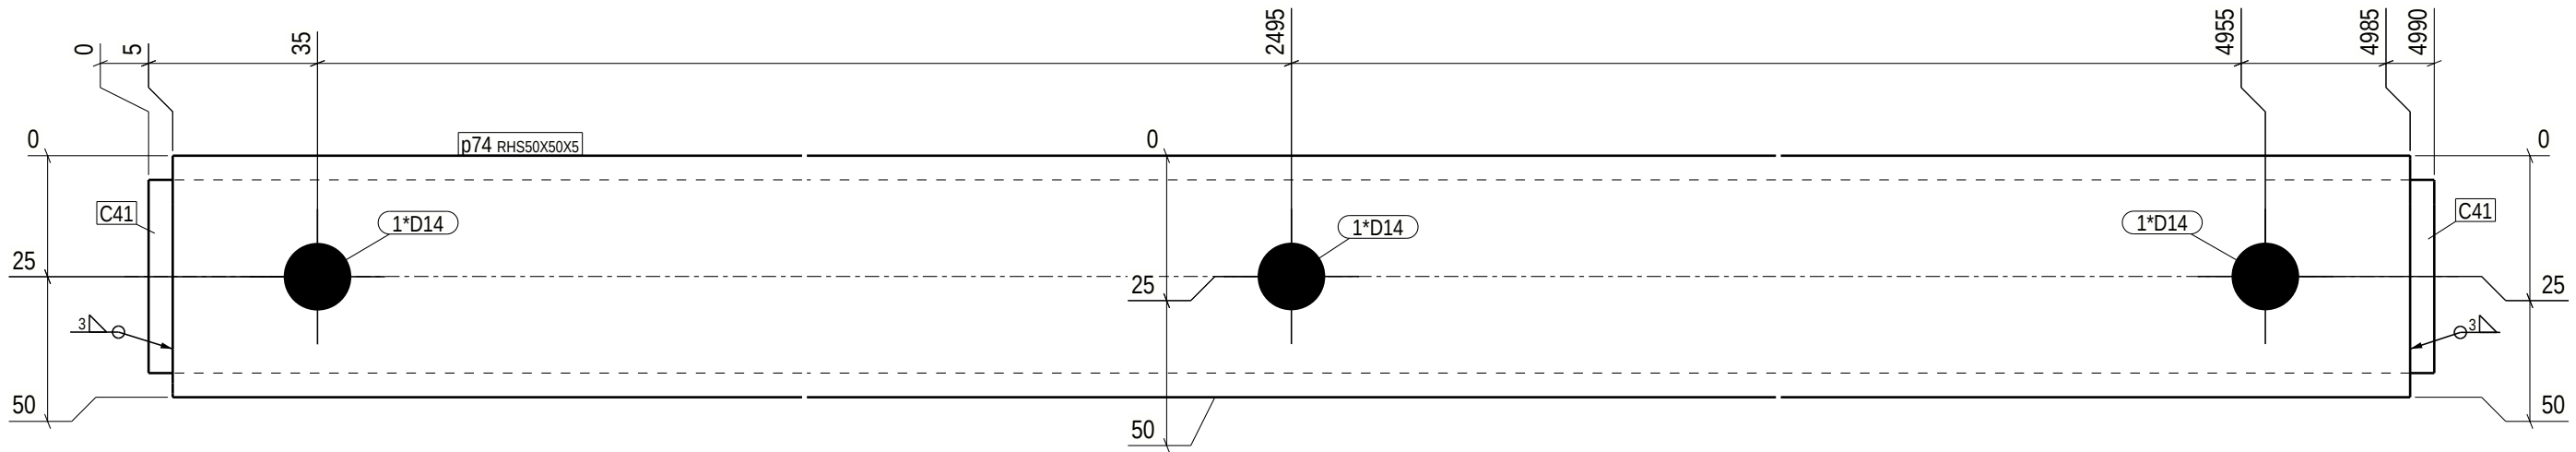

GENERAL NOTES:						
For your safety, check weight before handling:						
0-5kg Light 5-15kg Normal 15+kg Heavy						
ALL WELDS ARE 4 UNLESS NOTED ON DRAWING						
MATERIAL LIST FOR ASSEMBLY MK'D p.74						
Mark	Profile	Material	No.	Length	Area	Weight
p74	RHS50X50X5	S355J2H	1	4980	0.9	32.4 !!
C41	FL5*40	S355J2	2	40	0.0	0.1
Total				0.9	32.6	

Finish Class
Standard

Surface treatment info:	Thickness/start point--> length	No.
-------------------------	---------------------------------	-----

weld a = 4

PHASE	QUANTITY
2	4

* o 3 0 4 8 0 - 2 * DS Stahlkonstruktion * A p 7 4 *					
PROJECT	Akkasæter Lager- og vedlikeholdshall			EXEC. CLASS	EXC 2
MEMBER	Portomfatning		QUANTITY:	4	PROJECT No 30480-2
REVISION		ISSUED: 07.11.2025	DRAFTER: ZLL	BIM control: SST	DRAWING No. p.74