

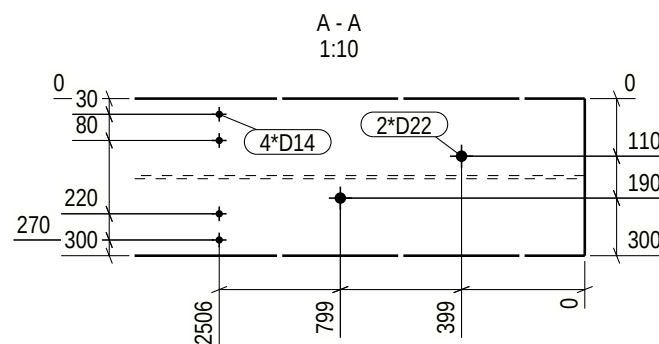
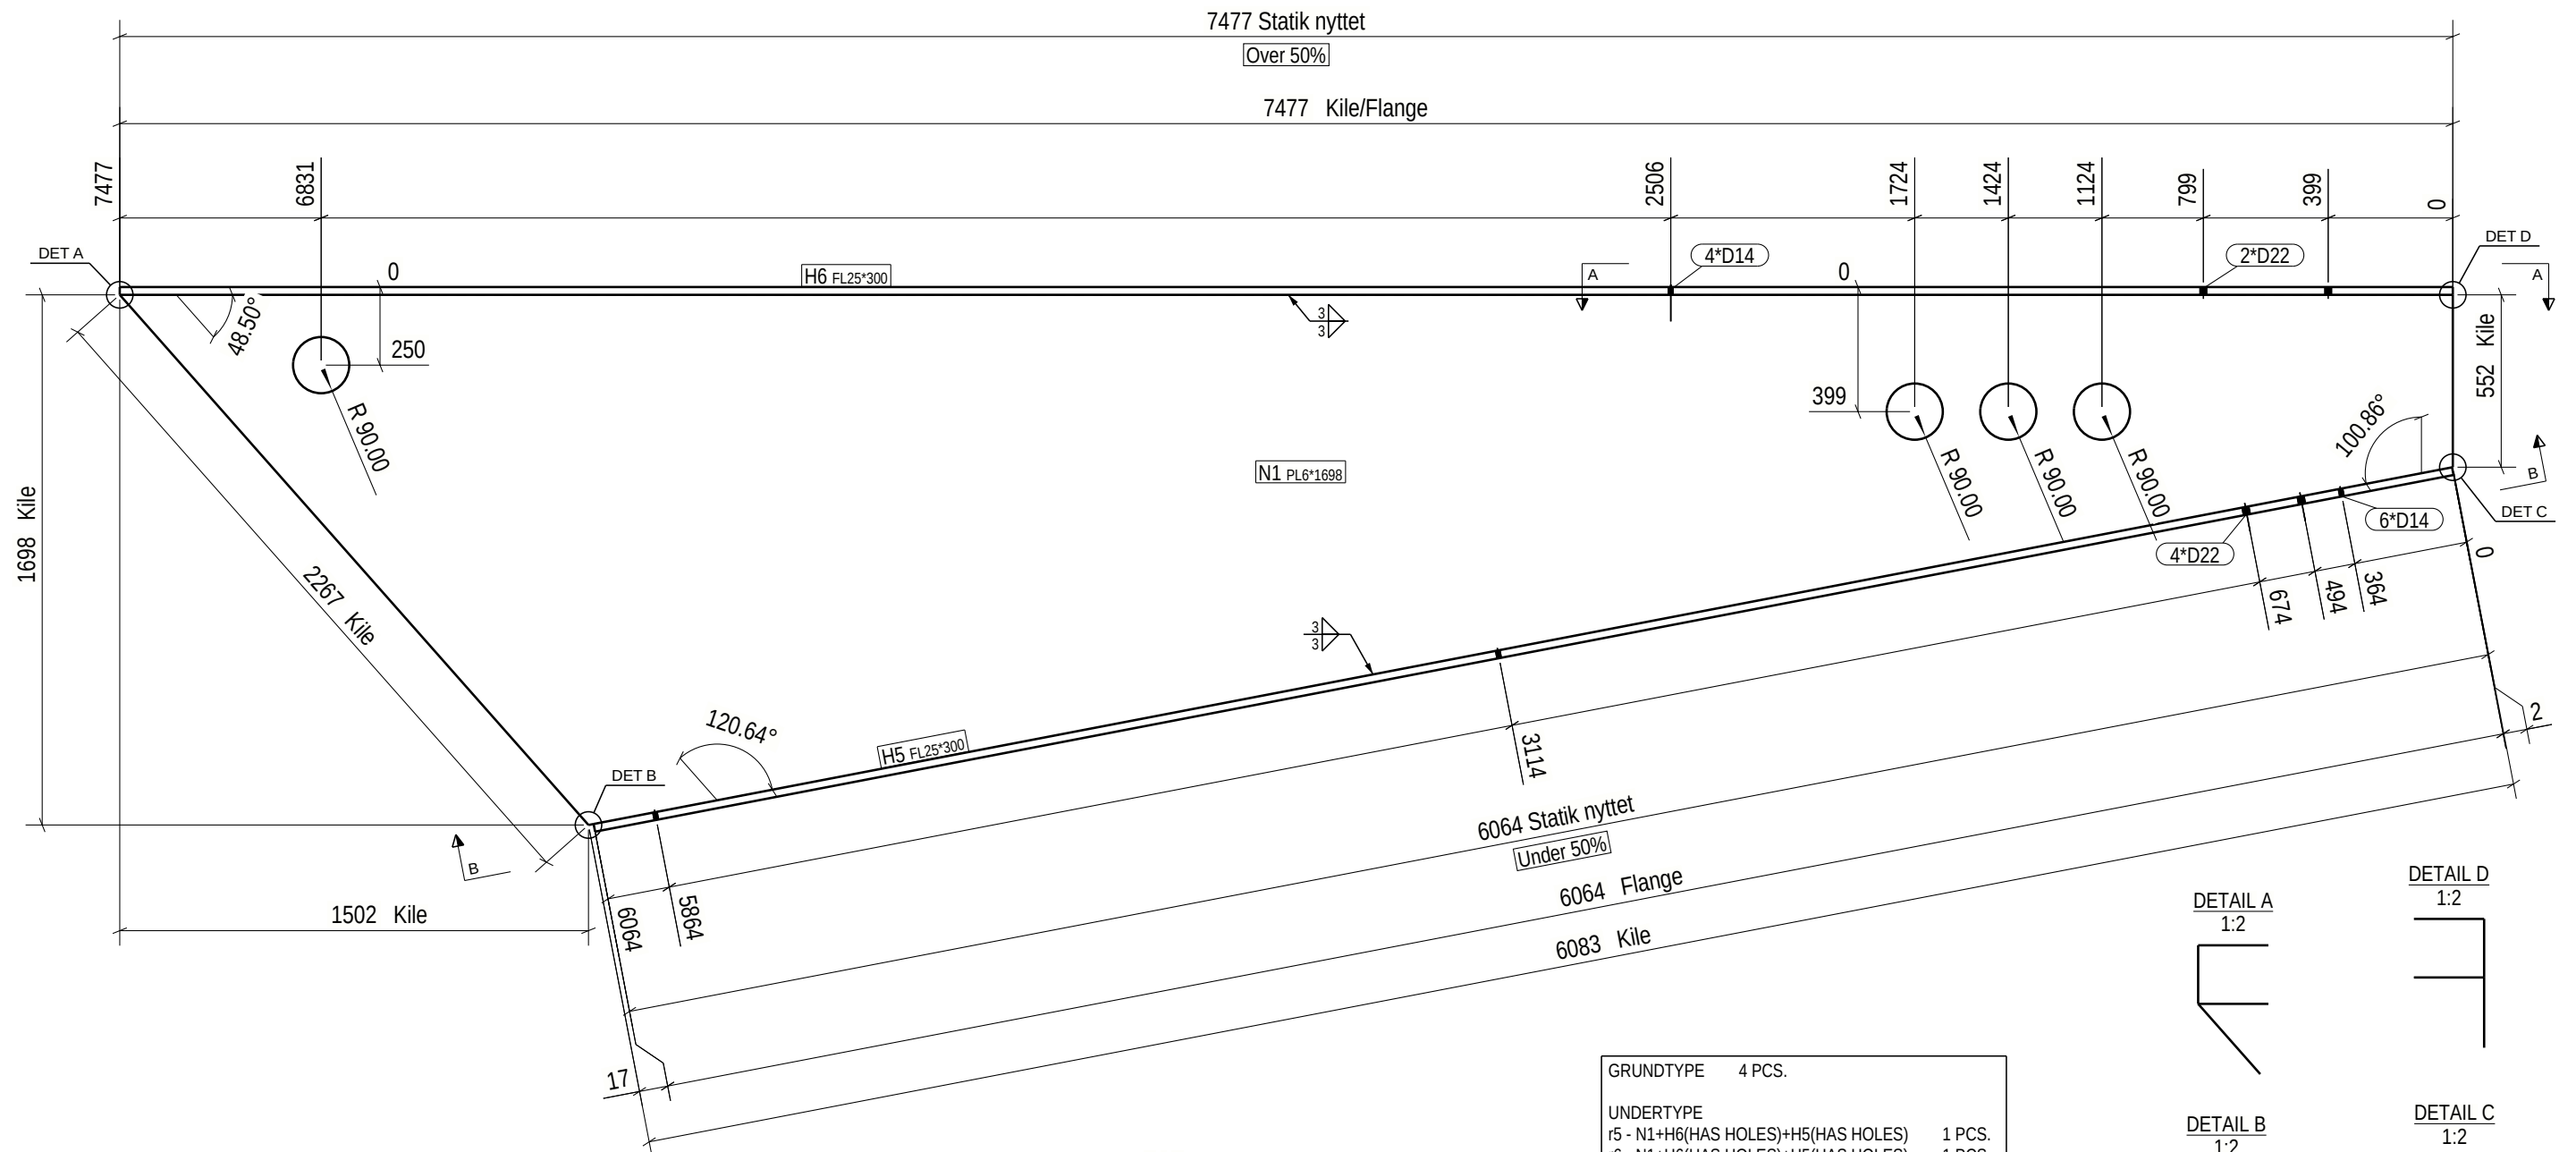


V-SEAM
Utilization under 50%
EXC 2=> Acc. to process control
EXC 3=> 20% UT
Utilization over 50%
EXC 2=> 10% UT
EXC 3=> 20% UT

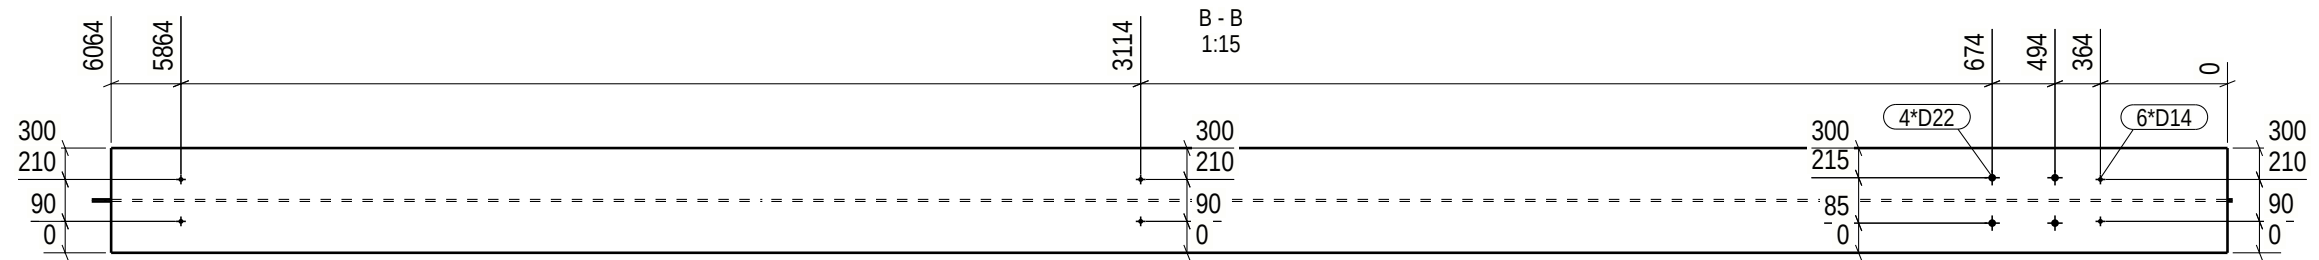

GRUNDTYPE	4 PCS.
UNDERTYPE	
r5 - N1+H6(HAS HOLES)+H5(HAS HOLES)	1 PCS.
r6 - N1+H6(HAS HOLES)+H5(HAS HOLES)	1 PCS.
r7 - N1+H6(HAS HOLES)+H5(HAS HOLES)	1 PCS.
r8 - N1+H6(HAS HOLES)+H5(HAS HOLES)	1 PCS.
SUM	4 PCS.

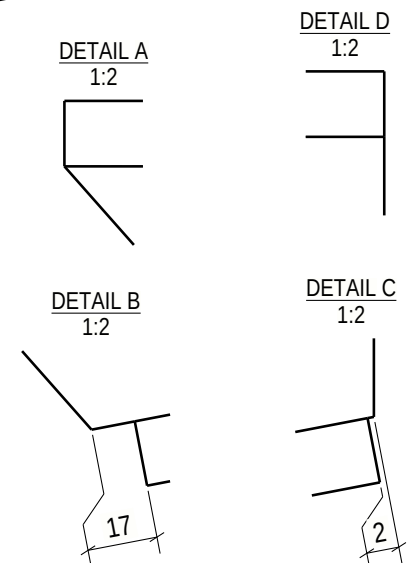


ALL WELDS ARE 4 UNLESS NOTED ON DRAWING

MATERIAL LIST FOR ASSEMBLY MK'D r.5 - 1 (See table) No. Required

Mark	Profile	Material	No.	Length	Area	Weight
H5	FL25*300	S355J2	1	6064	4.0	357.0 !!
H6	FL25*300	S355J2	1	7477	4.9	440.2 !!
N1	PL6*1698	S355J2	1	7477	15.9	371.8 !!
Total					24.7	1169.0

Finish Class
Standard

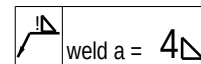

PHASE	QUANTITY
See Undertype drawings	

* o 3 0 4 8 0 - 2 *				 DS <i>Swilkonstruktion</i>		* A r 5 *	
PROJECT	Akkasæter Lager- og vedlikeholdshall				EXEC. CLASS		EXC 2
MEMBER	Kiletegning		QUANTITY: (See table)		PROJECT No		30480-2
REVISION	ISSUED: 07.11.2025		DRAFTER: ZLL BIM-control: ZLL		DRAWING No.		r.5 - 1