


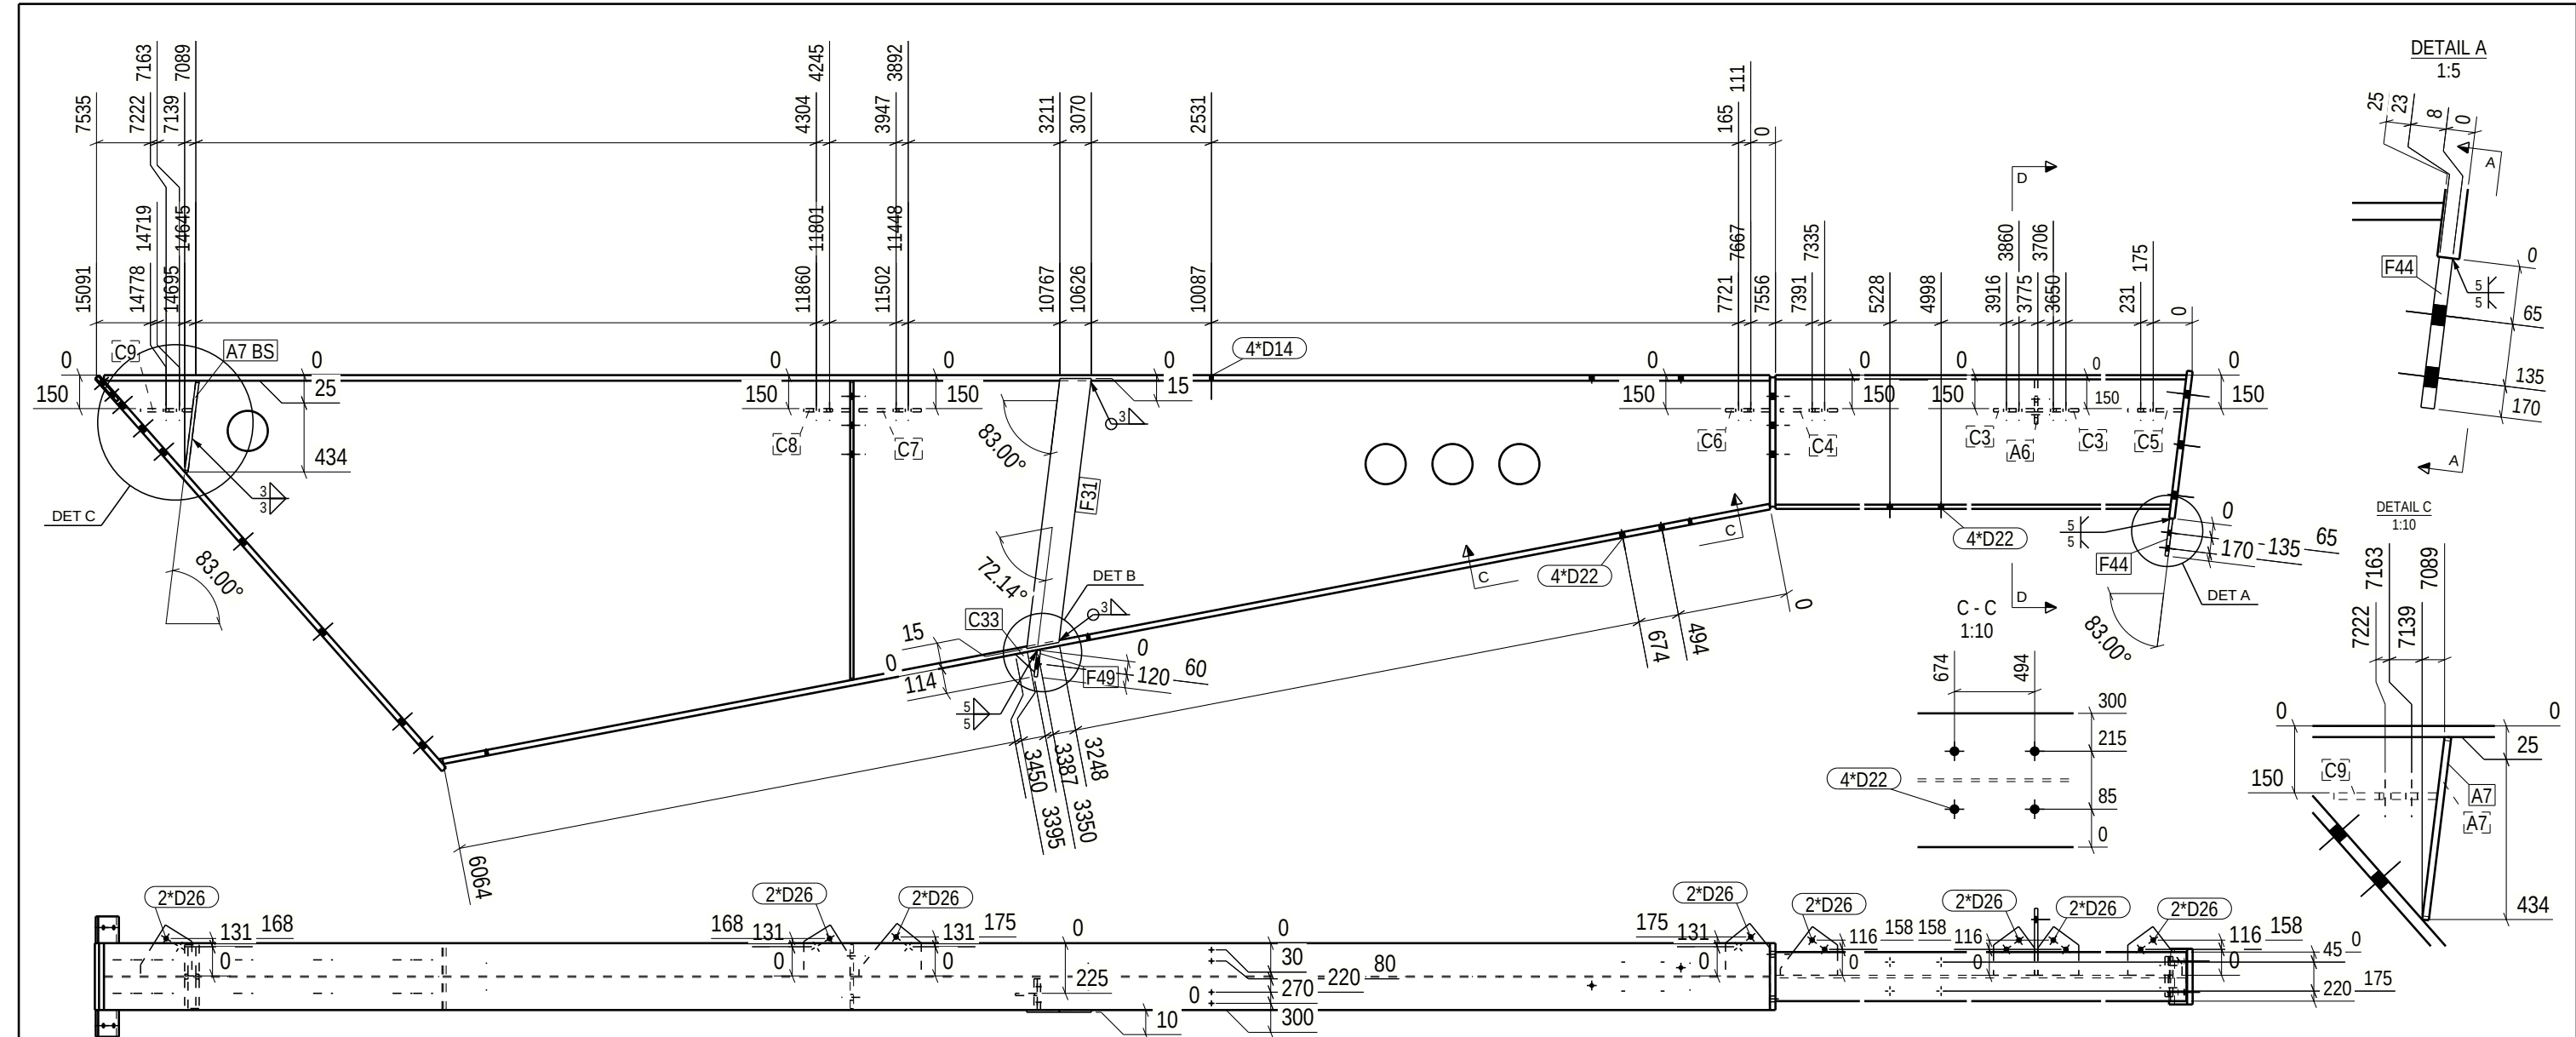

GENERAL NOTES: For your safety, check weight before handling:
0-5kg Light 5-15kg Normal 15+kg Heavy

ALL WELDS ARE 4 UNLESS NOTED ON DRAWING

MATERIAL LIST FOR ASSEMBLY MK'D r.5 1 No. Required

Mark	Profile	Material	No.	Length	Area	Weight
r5	IPE600	S355J2	1	7530	15.2	920.3 !!
A1	FL25*300	S355J2	1	580	0.4	34.1 !!
A2	FL15*140	S355J2	2	1341	0.4	22.1 !!
A6	FL15*200	S355J2	1	300	0.1	7.0
A7	FL15*140	S355J2	2	413	0.1	6.8
C3	PL15*184	S355J2	2	219	0.1	3.8
C4	PL15*219	S355J2	1	257	0.1	4.5
C5	PL15*219	S355J2	1	243	0.1	4.4
C6	PL15*199	S355J2	1	236	0.1	4.4
C7	PL15*236	S355J2	1	280	0.1	5.1
C8	PL15*207	S355J2	1	229	0.1	4.3
C9	PL15*229	S355J2	1	230	0.1	4.5
C33	PL10*81	S355J2	1	118	0.0	0.4
F3	FL25*300	S355J2	1	2351	1.5	138.4 !!
F6	FL25*250	S355J2 Z15	1	666	0.4	32.7 !!
F10	FL15*120	S355J2	2	140	0.0	2.0
F31	FL10*140	S355J2	1	1238	0.4	13.3
F44	FL15*170	S355J2	1	180	0.1	3.6
F49	FL15*120	S355J2	1	140	0.0	2.0
H5	FL25*300	S355J2	1	6064	4.0	357.0 !!
H6	FL25*300	S355J2	1	7477	4.9	440.2 !!
N1	PL6*1698	S355J2	1	7477	15.9	371.8 !!
Total				44.7	2417.4	

Finish Class
Standard

Surface treatment info: Thickness/start point-> length No.

weld a = 4

PHASE	QUANTITY
2	1

* o 3 0 4 8 0 - 2 *								DS		Steelkonstruktion		* A r 5 *	
PROJECT		Akkasæter Lager- og vedlikeholdshall						EXEC. CLASS		EXC 2			
MEMBER		Rigle - UT af r4-2				QUANTITY:		1		PROJECT No		30480-2	
REVISION				ISSUED: 07.11.2025		DRAFTER:		ZLL		DRAWING No.		r.5	
						BIM control:		SST					

Undertype of
r4 - 2