
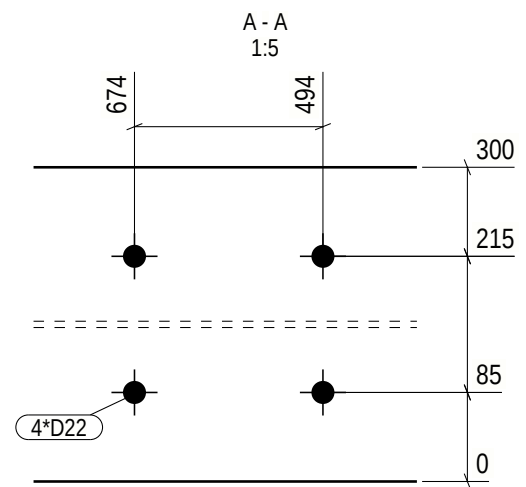
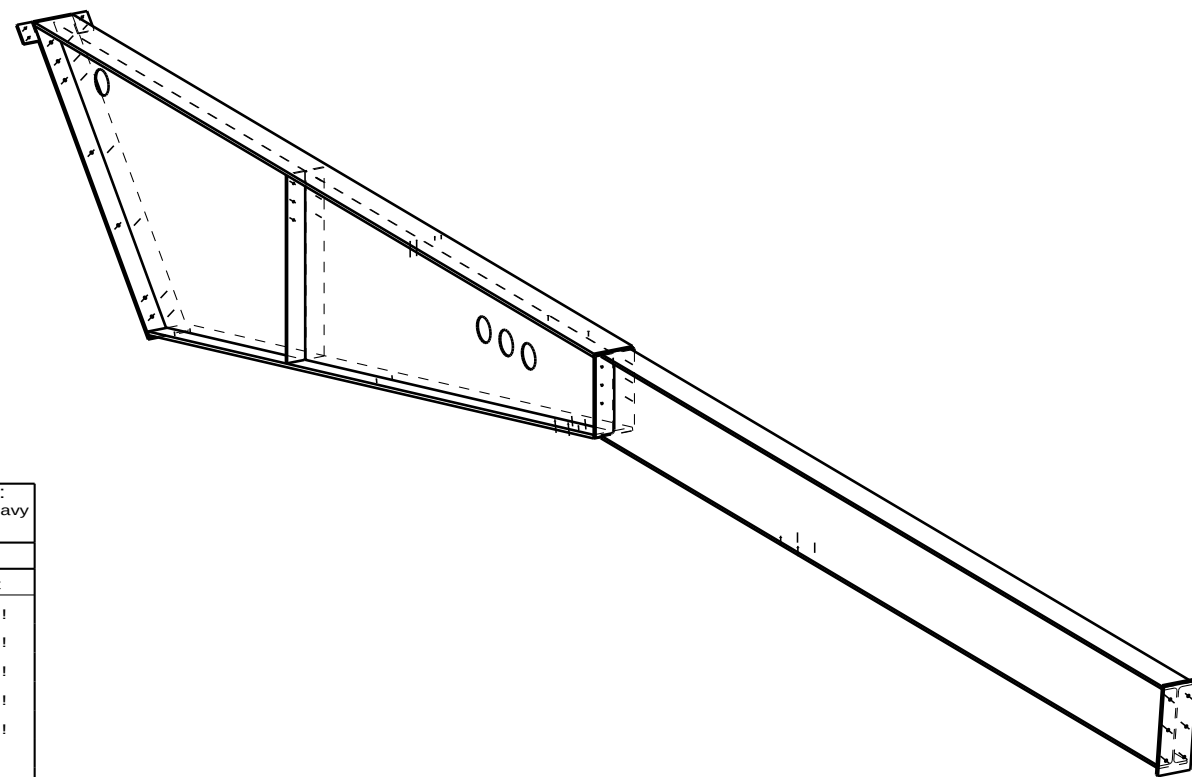
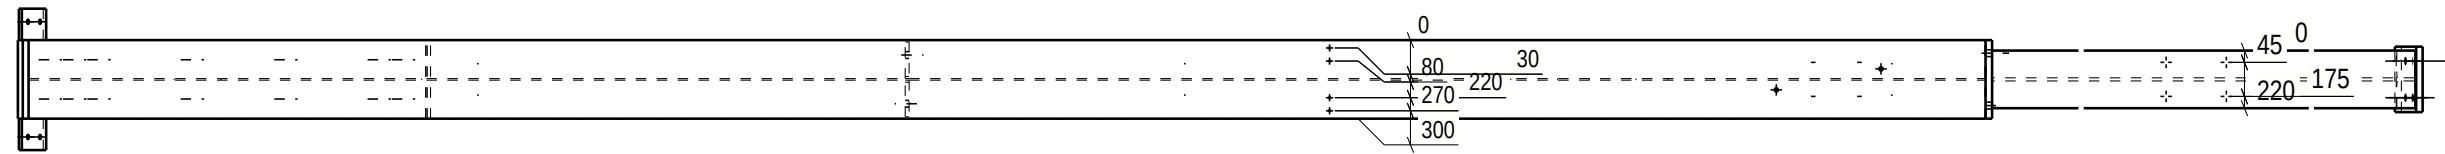


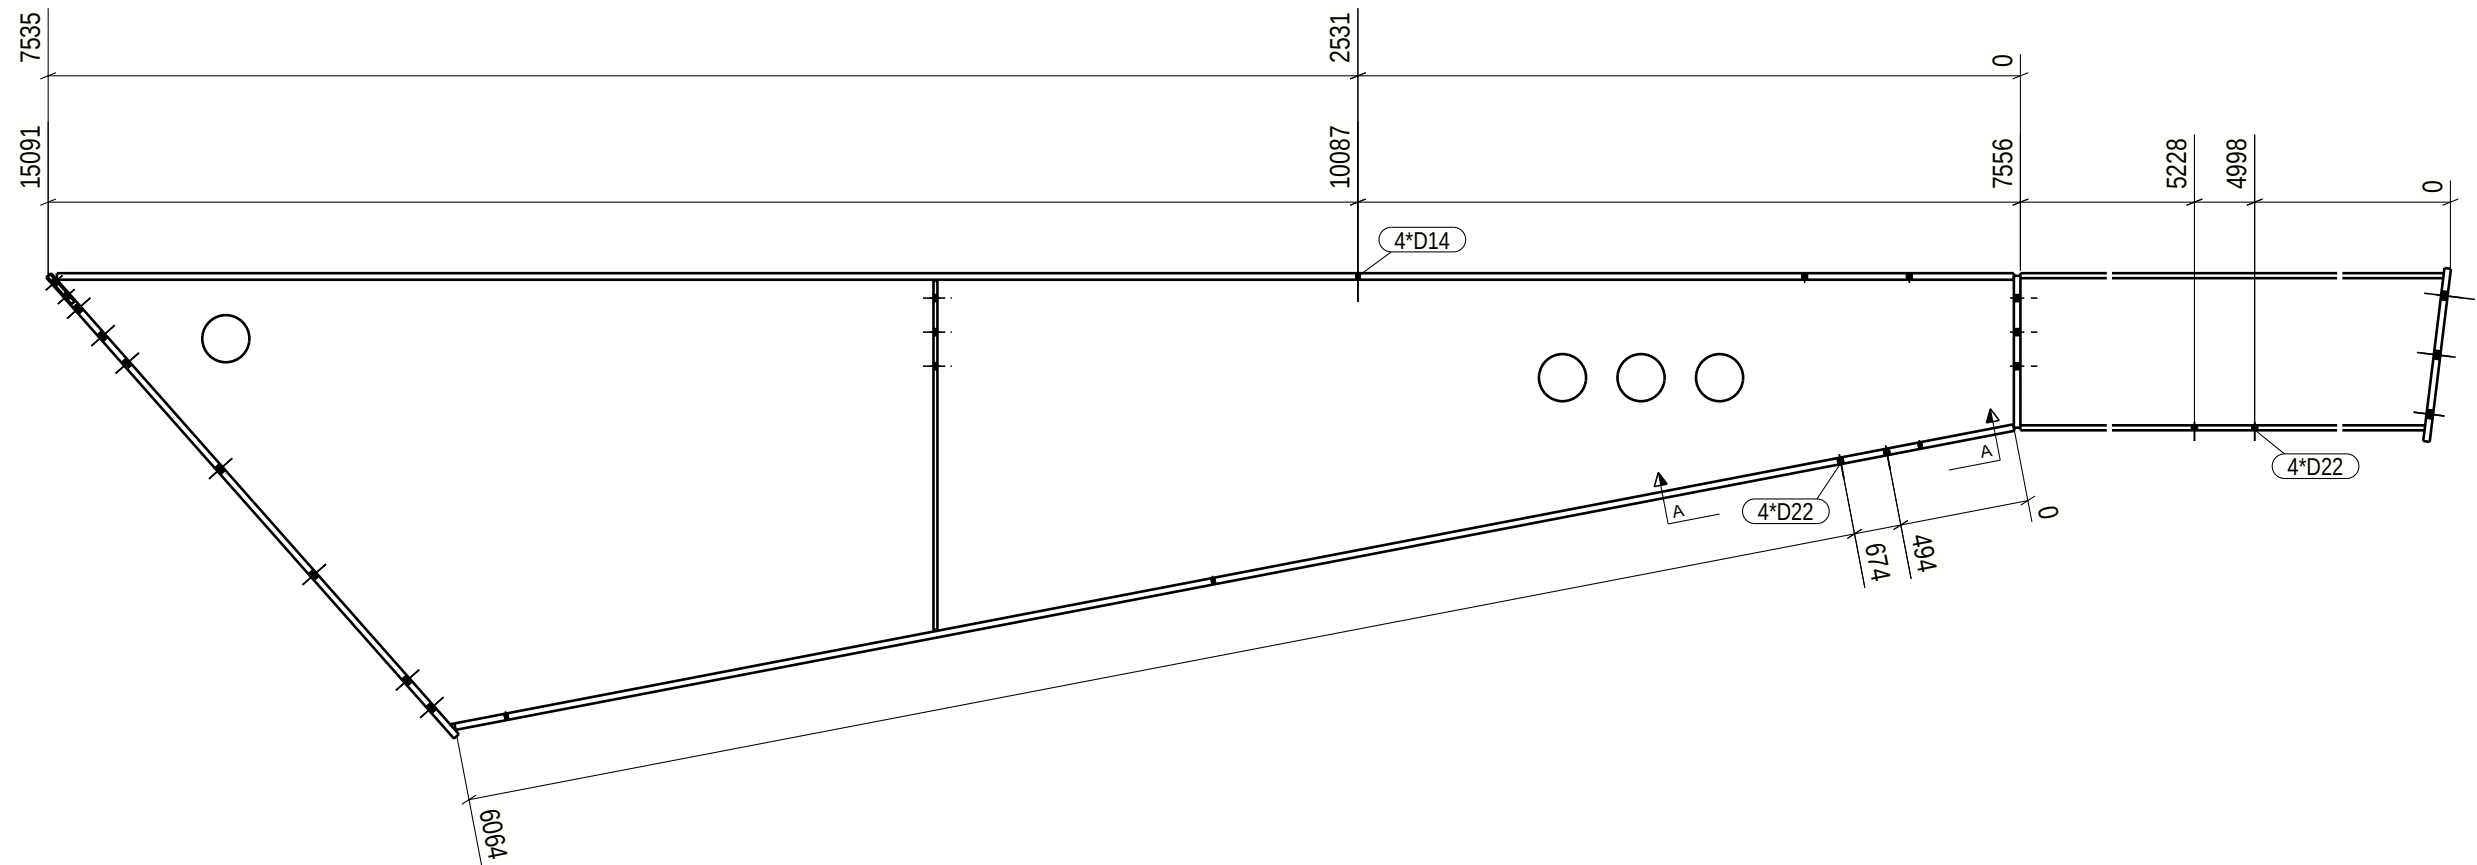

GENERAL NOTES: For your safety, check weight before handling:
0-5kg Light 5-15kg Normal 15+kg Heavy

ALL WELDS ARE 4 UNLESS NOTED ON DRAWING

MATERIAL LIST FOR ASSEMBLY MK'D r. 7 1 No. Required

Mark	Profile	Material	No.	Length	Area	Weight
r7	IPE600	S355J2	1	7530	15.2	920.3 !!
A1	FL25*300	S355J2	1	580	0.4	34.1 !!
A2	FL15*140	S355J2	2	1341	0.4	22.1 !!
F3	FL25*300	S355J2	1	2351	1.5	138.4 !!
F6	FL25*250	S355J2 Z15	1	666	0.4	32.7 !!
F10	FL15*120	S355J2	2	140	0.0	2.0
H5	FL25*300	S355J2	1	6064	4.0	357.0 !!
H6	FL25*300	S355J2	1	7477	4.9	440.2 !!
N1	PL6*1698	S355J2	1	7477	15.9	371.8 !!
Total				43.1	2342.7	

Finish Class
Standard

Surface treatment info: Thickness/start point-> length No.

weld a = 4

PHASE	QUANTITY
2	1

* o 3 0 4 8 0 - 2 * DS Stalkonstruktion * A r 7 *			
PROJECT	Akkasæter Lager- og vedlikeholdshall	EXEC. CLASS	EXC 2
MEMBER	Rigle - UT af r4-2	QUANTITY:	1 PROJECT No 30480-2
REVISION	ISSUED: 07.11.2025	DRAFTER: ZLL SST	DRAWING No. r.7

Undertype of
r4 - 2