


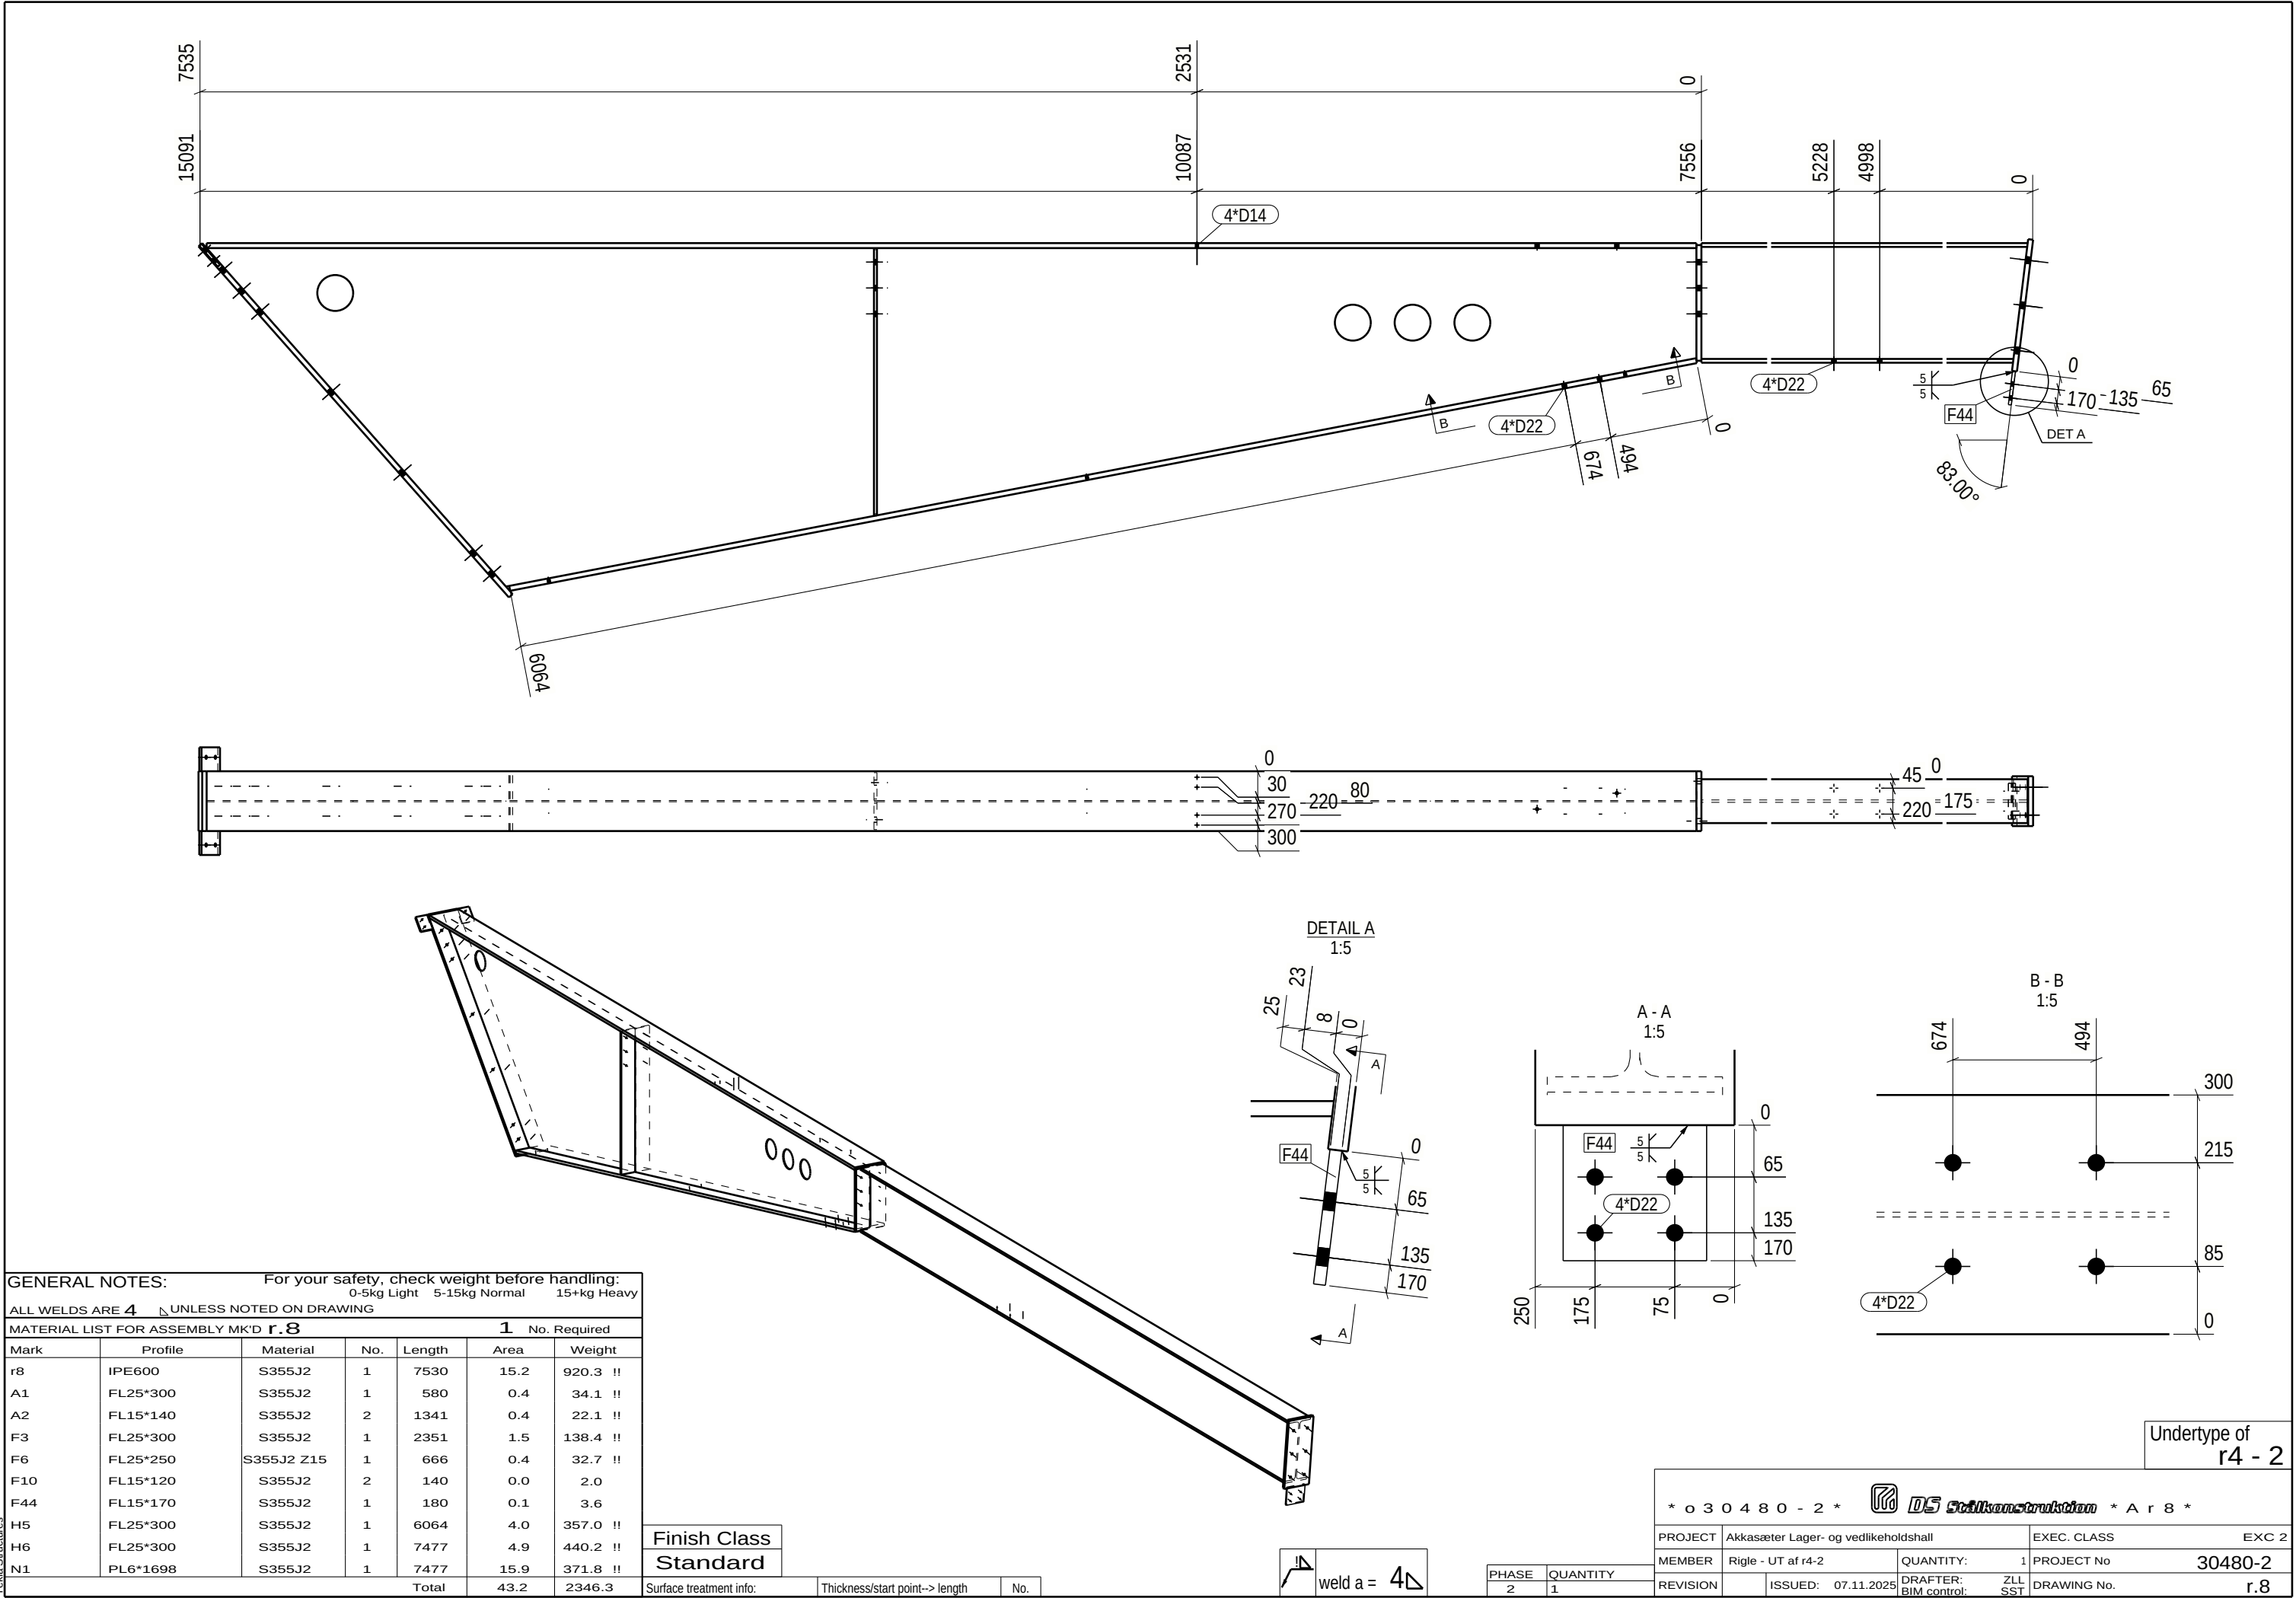

GENERAL NOTES: For your safety, check weight before handling:						
ALL WELDS ARE 4 UNLESS NOTED ON DRAWING						
MATERIAL LIST FOR ASSEMBLY MK'D r.8						
Mark	Profile	Material	No.	Length	Area	Weight
r8	IPE600	S355J2	1	7530	15.2	920.3 !!
A1	FL25*300	S355J2	1	580	0.4	34.1 !!
A2	FL15*140	S355J2	2	1341	0.4	22.1 !!
F3	FL25*300	S355J2	1	2351	1.5	138.4 !!
F6	FL25*250	S355J2 Z15	1	666	0.4	32.7 !!
F10	FL15*120	S355J2	2	140	0.0	2.0
F44	FL15*170	S355J2	1	180	0.1	3.6
H5	FL25*300	S355J2	1	6064	4.0	357.0 !!
H6	FL25*300	S355J2	1	7477	4.9	440.2 !!
N1	PL6*1698	S355J2	1	7477	15.9	371.8 !!
Total				43.2	2346.3	

Finish Class
Standard

Surface treatment info:	Thickness/start point-> length	No.
-------------------------	--------------------------------	-----

weld a = 4

PHASE	QUANTITY
2	1

* o 3 0 4 8 0 - 2 * DS Skalkonstruktion * A r 8 *			
PROJECT	Akkasæter Lager- og vedlikeholdshall	EXEC. CLASS	EXC 2
MEMBER	Rigle - UT af r4-2	QUANTITY:	1
REVISION	ISSUED: 07.11.2025	DRAFTER:	ZLL
		BIM control:	SST
PROJECT No		30480-2	
DRAWING No.		r.8	

Undertype of
r4 - 2