
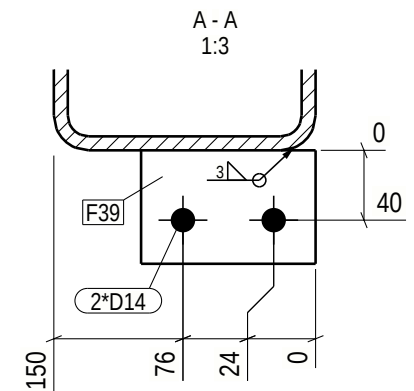
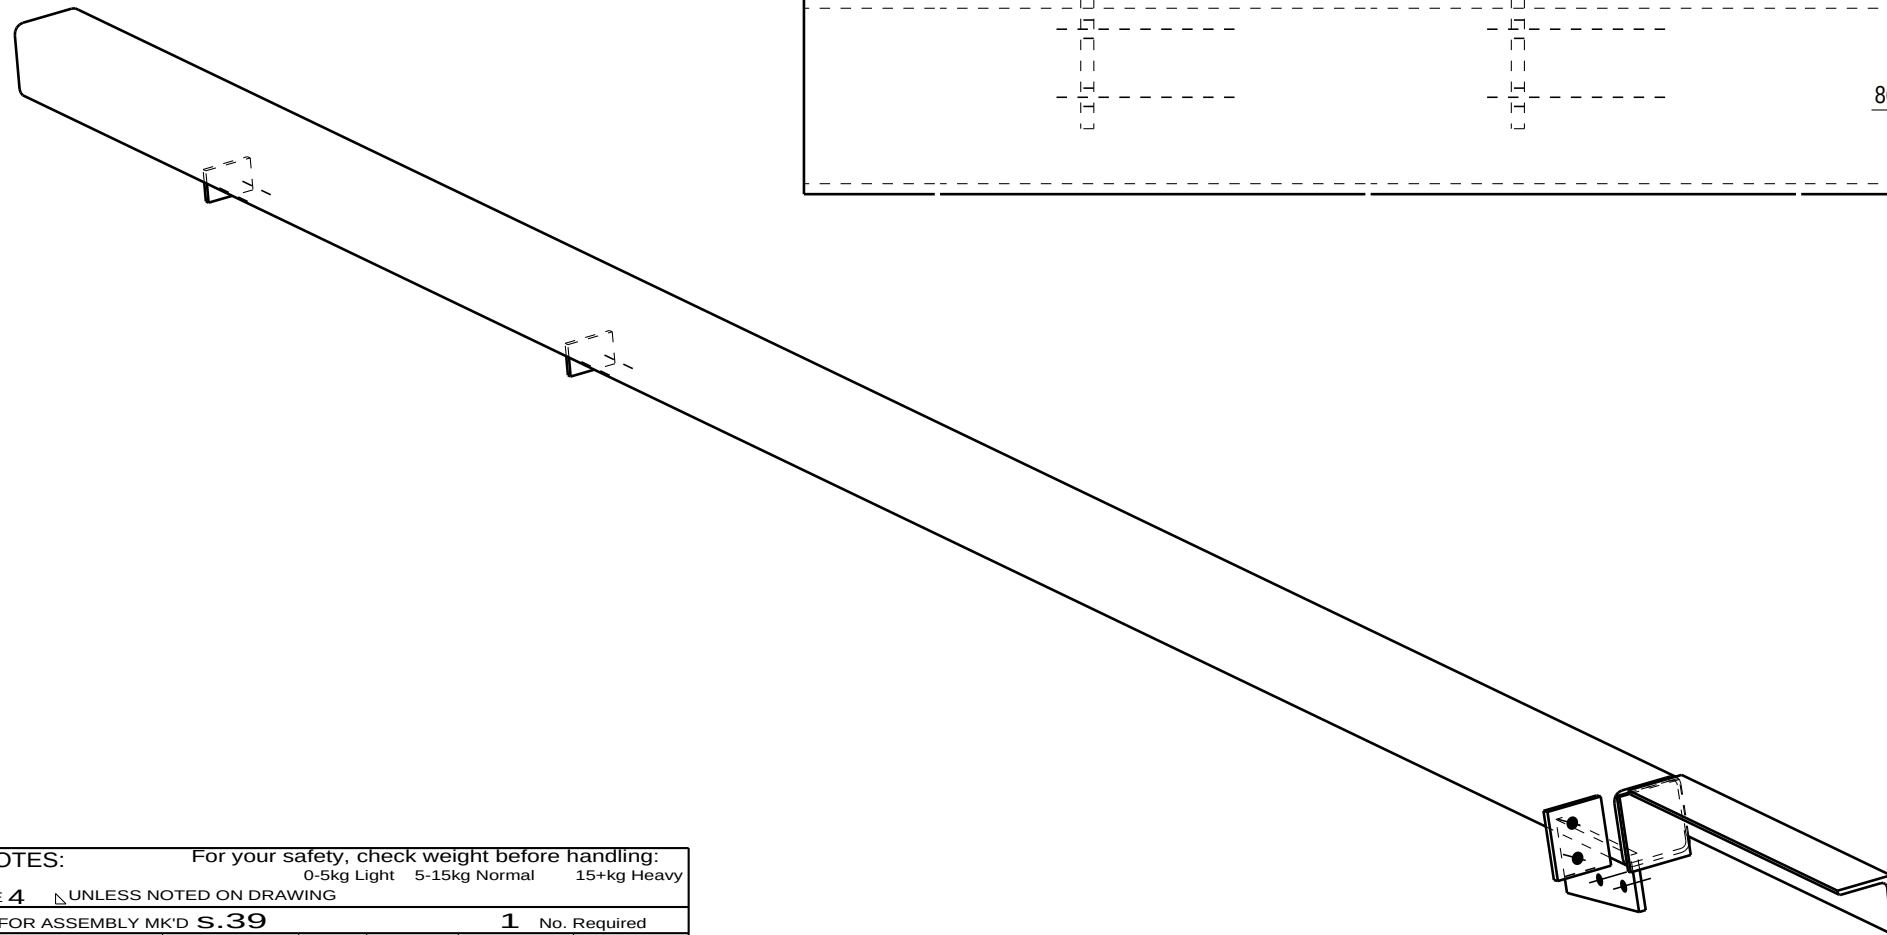
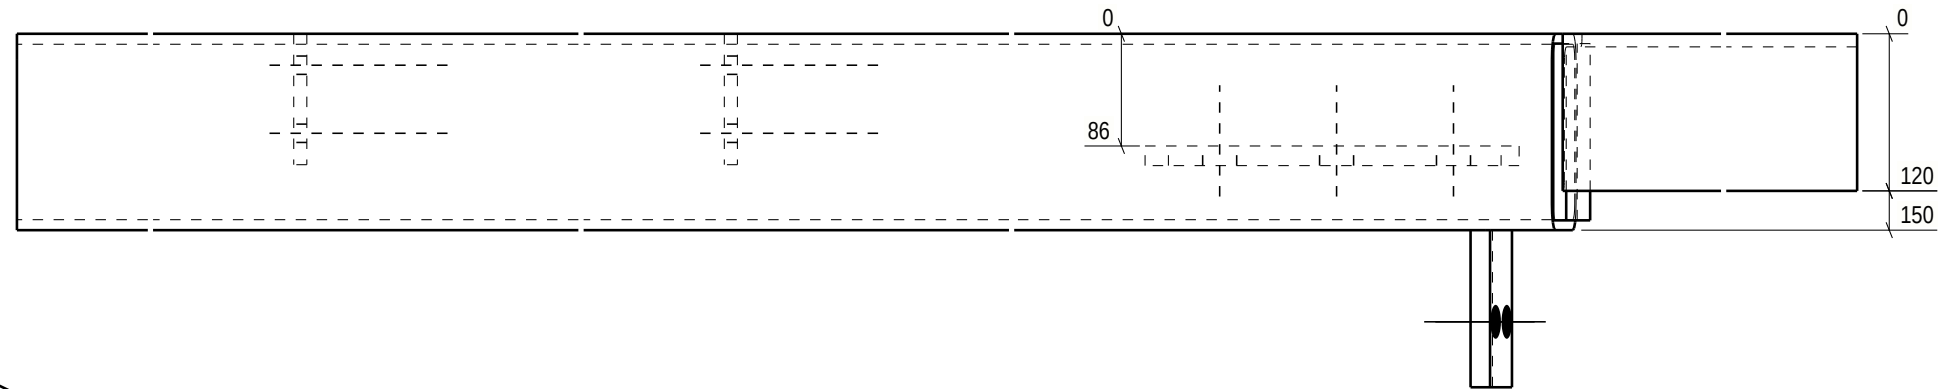
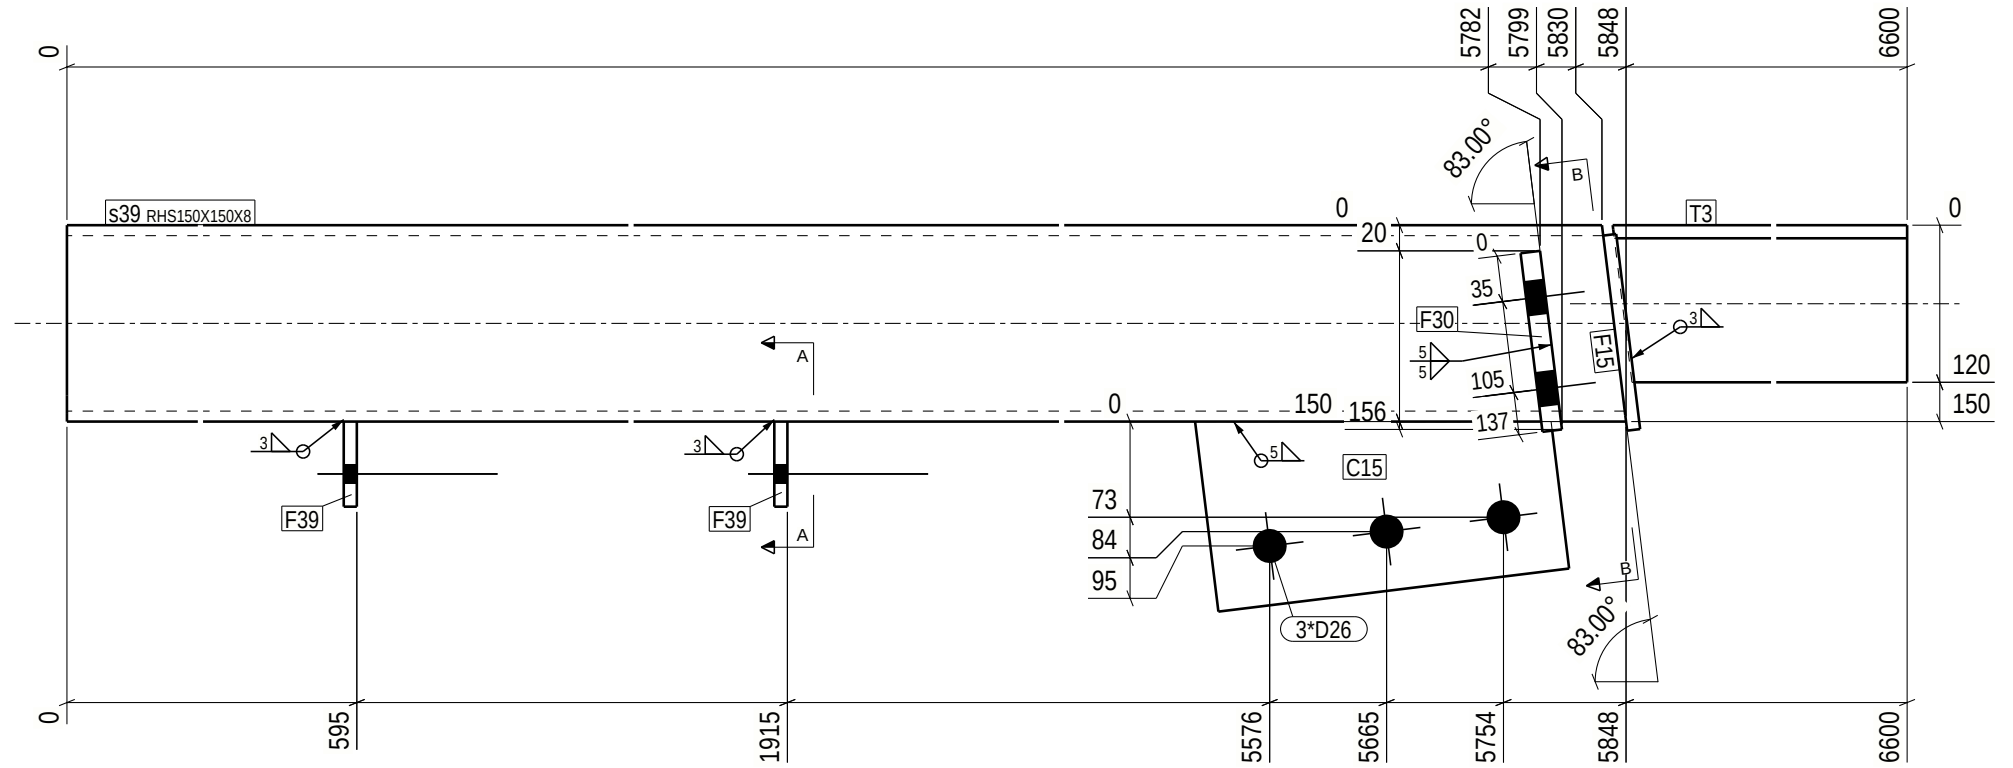


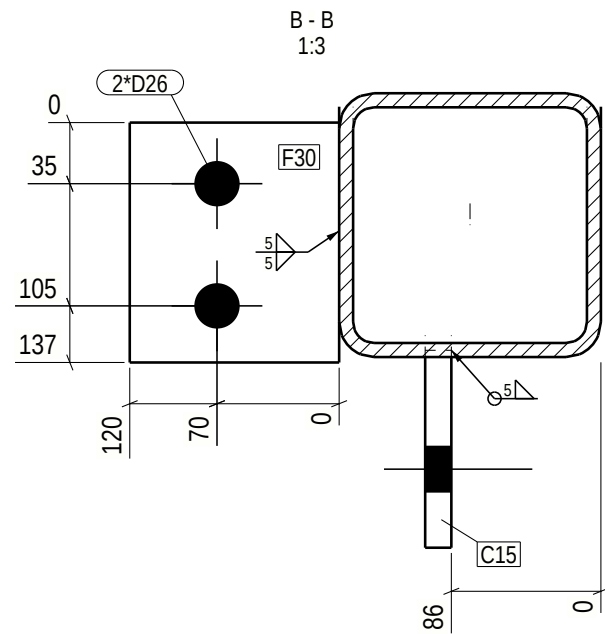

GENERAL NOTES: For your safety, check weight before handling:
0-5kg Light 5-15kg Normal 15+kg Heavy

ALL WELDS ARE 4 UNLESS NOTED ON DRAWING

MATERIAL LIST FOR ASSEMBLY MK'D **s.39** **1** No. Required

Mark	Profile	Material	No.	Length	Area	Weight
s39	RHS150X150X8	S355J2H	1	5848	3.3	197.3 !!
C15	PL15*146	S355J2	1	270	0.1	4.1
F15	FL10*135	S355J2	1	150	0.0	1.6
F30	FL15*120	S355J2	1	137	0.0	1.9
F39	FL10*65	S355J2	2	100	0.0	0.5
T3	L120*10	S355J2	1	762	0.4	13.8
Total					3.9	219.7

Finish Class
Standard

Surface treatment info: Thickness/start point-> length No.

weld a = 4

PHASE	QUANTITY
2	1

* o 3 0 4 8 0 - 2 *  DS <i>Stalkonstruktion</i> * A s 3 9 *			
PROJECT	Akkasæter Lager- og vedlikeholdshall	EXEC. CLASS	EXC 2
MEMBER	Søyle	QUANTITY:	1
REVISION	ISSUED: 07.11.2025	DRAFTER:	ZLL
		BIM control:	SST
PROJECT No		30480-2	
DRAWING No.		s.39	