


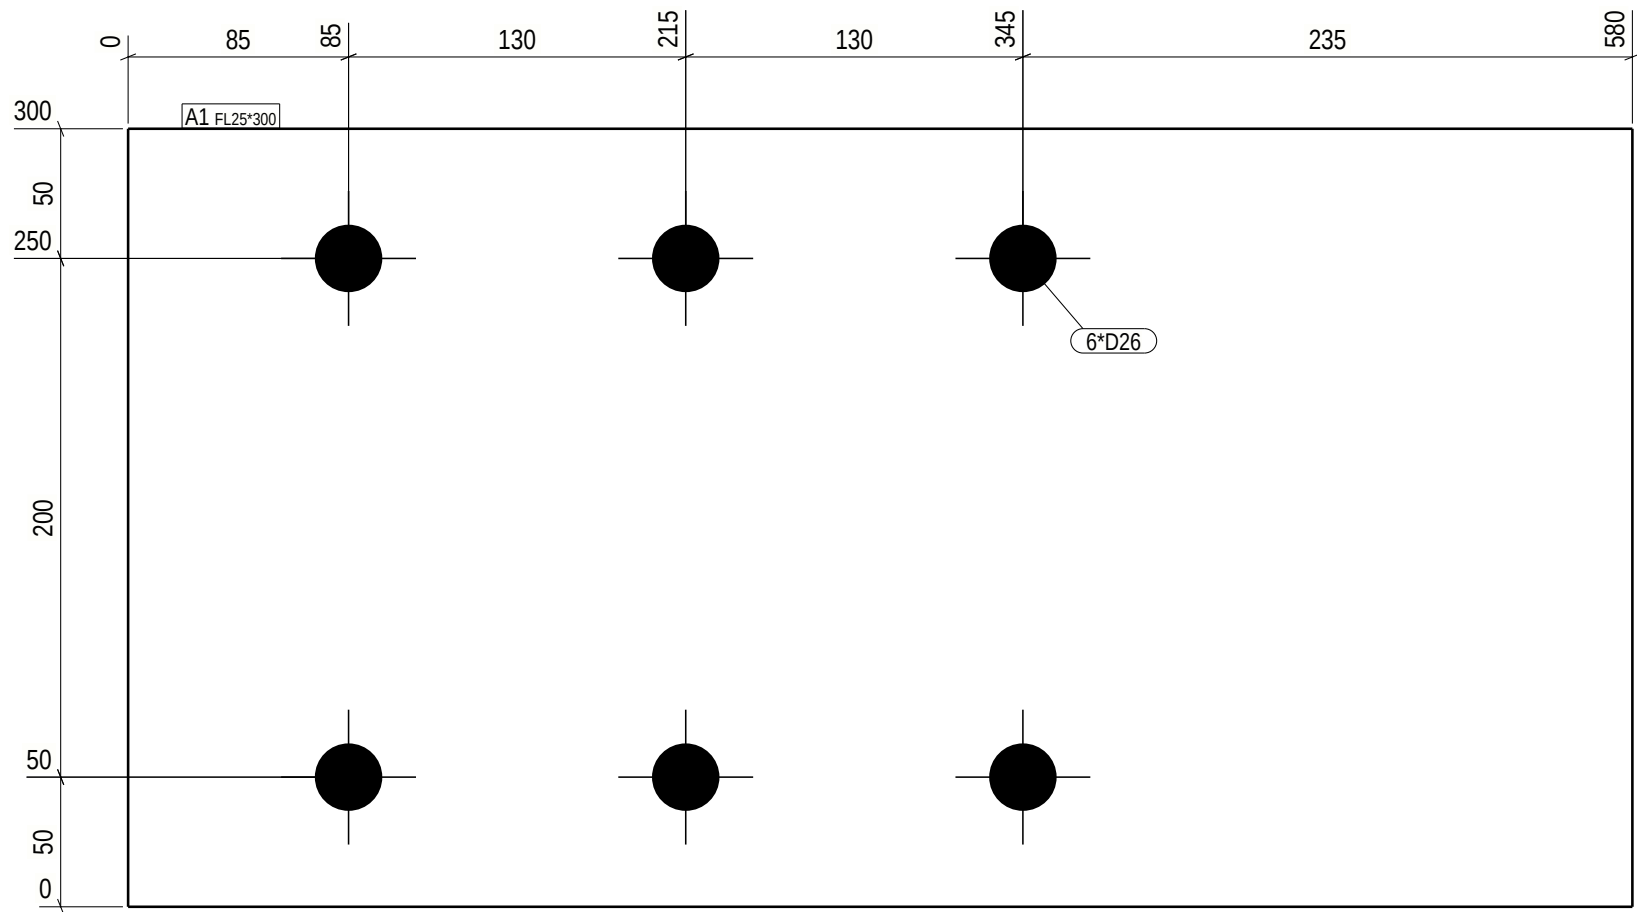

GENERAL NOTES:						
For your safety, check weight before handling:						
0-5kg Light 5-15kg Normal 15+kg Heavy						
MATERIAL LIST FOR PART - A1						
16 PARTS REQUIRED						
POS. No.	PROFILE	No.	GRADE	L (mm)	AREA (m ²)	WEIGHT (kg)
A1	FL25*300	1	S355J2	580	0.4	34.1 !!
TOTAL WEIGHT FOR				16	PARTS	546.4

Part list	Qty.
FT	16

Execution class: EXC 2		* o 3 0 4 8 0 - 2 *  DS <i>Skalkonstruktion</i> * W A 1 *			
No utilization on drawings = over 50%					
V-SEAM Utilization under 50% EXC 2=> Acc. to process control EXC 3=> 20% UT Utilization over 50% EXC 2=> 10% UT EXC 3=> 20% UT		PROJECT	Akkasæter Lager- og vedlikeholdshall	PHASE	2 / Phase 2
		MEMBER	Afstivning	QUANTITY:	16
		REVISION		ISSUED:	07.11.2025
				DRAFTER:	ZLL
				BIM control:	SST
				PROJECT No	30480-2
				DRAWING No.	A.1