


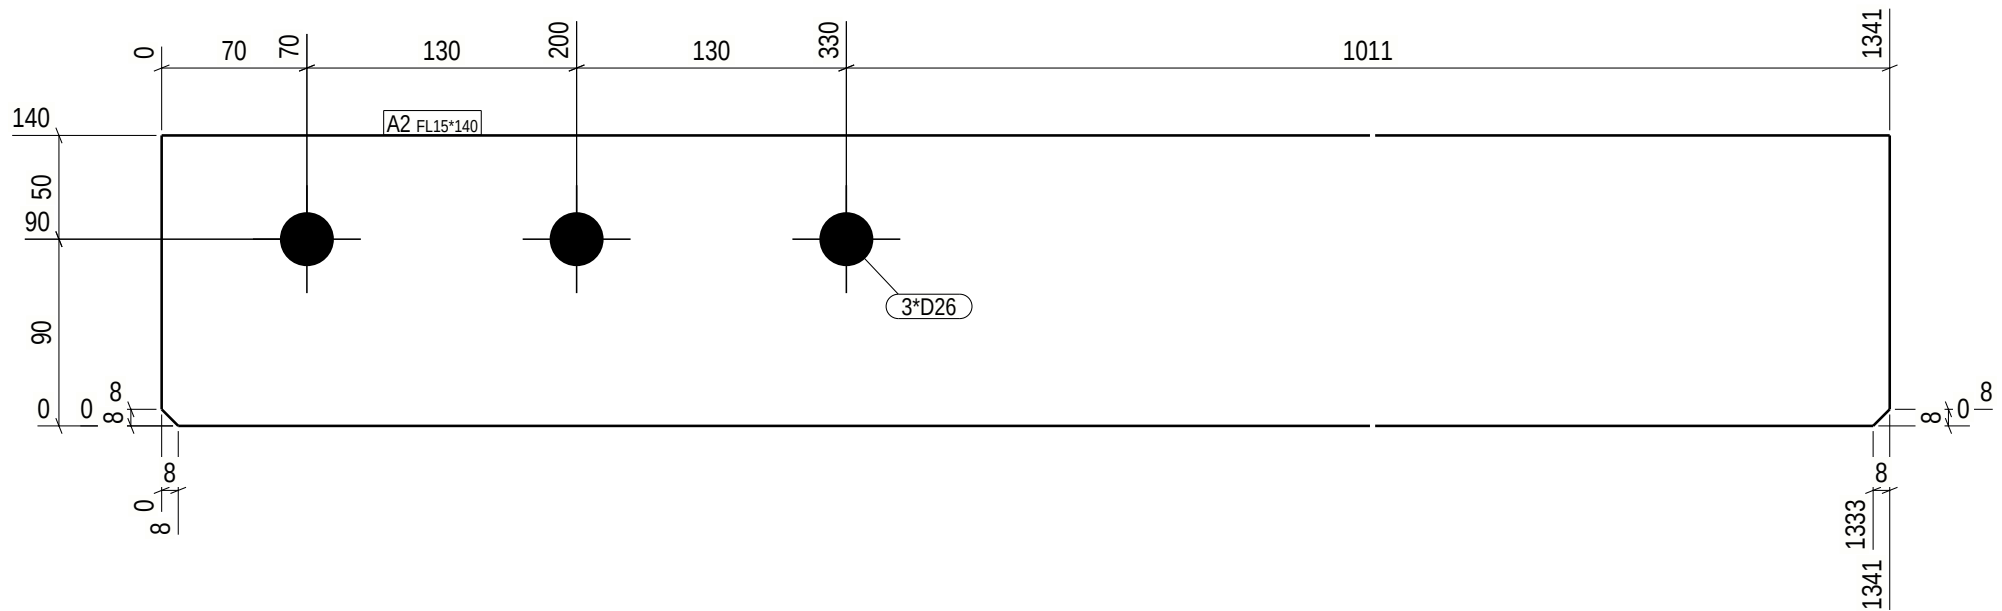

GENERAL NOTES:

For your safety, check weight before handling:
0-5kg Light 5-15kg Normal 15+kg Heavy

MATERIAL LIST FOR PART - A2

32 PARTS REQUIRED

POS. No.	PROFILE	No.	GRADE	L (mm)	AREA (m ²)	WEIGHT (kg)
A2	FL15*140	1	S355J2	1341	0.4	22.1 !!

TOTAL WEIGHT FOR 32 PARTS 707.0

Part list	Qty.
FT	32

Execution class: EXC 2

No utilization on drawings = over 50%

V-SEAM
Utilization under 50%
EXC 2=> Acc. to process control
EXC 3=> 20% UT
Utilization over 50%
EXC 2=> 10% UT
EXC 3=> 20% UT

* o 3 0 4 8 0 - 2 *



DS Skalkonstruktion

* W A 2 *

PROJECT	Akkasæter Lager- og vedlikeholdshall		PHASE	2 / Phase 2	
MEMBER	Afstivning		QUANTITY:	32	PROJECT No 30480-2
REVISION		ISSUED: 07.11.2025	DRAFTER: ZLL BIM control: SST		DRAWING No. A.2