


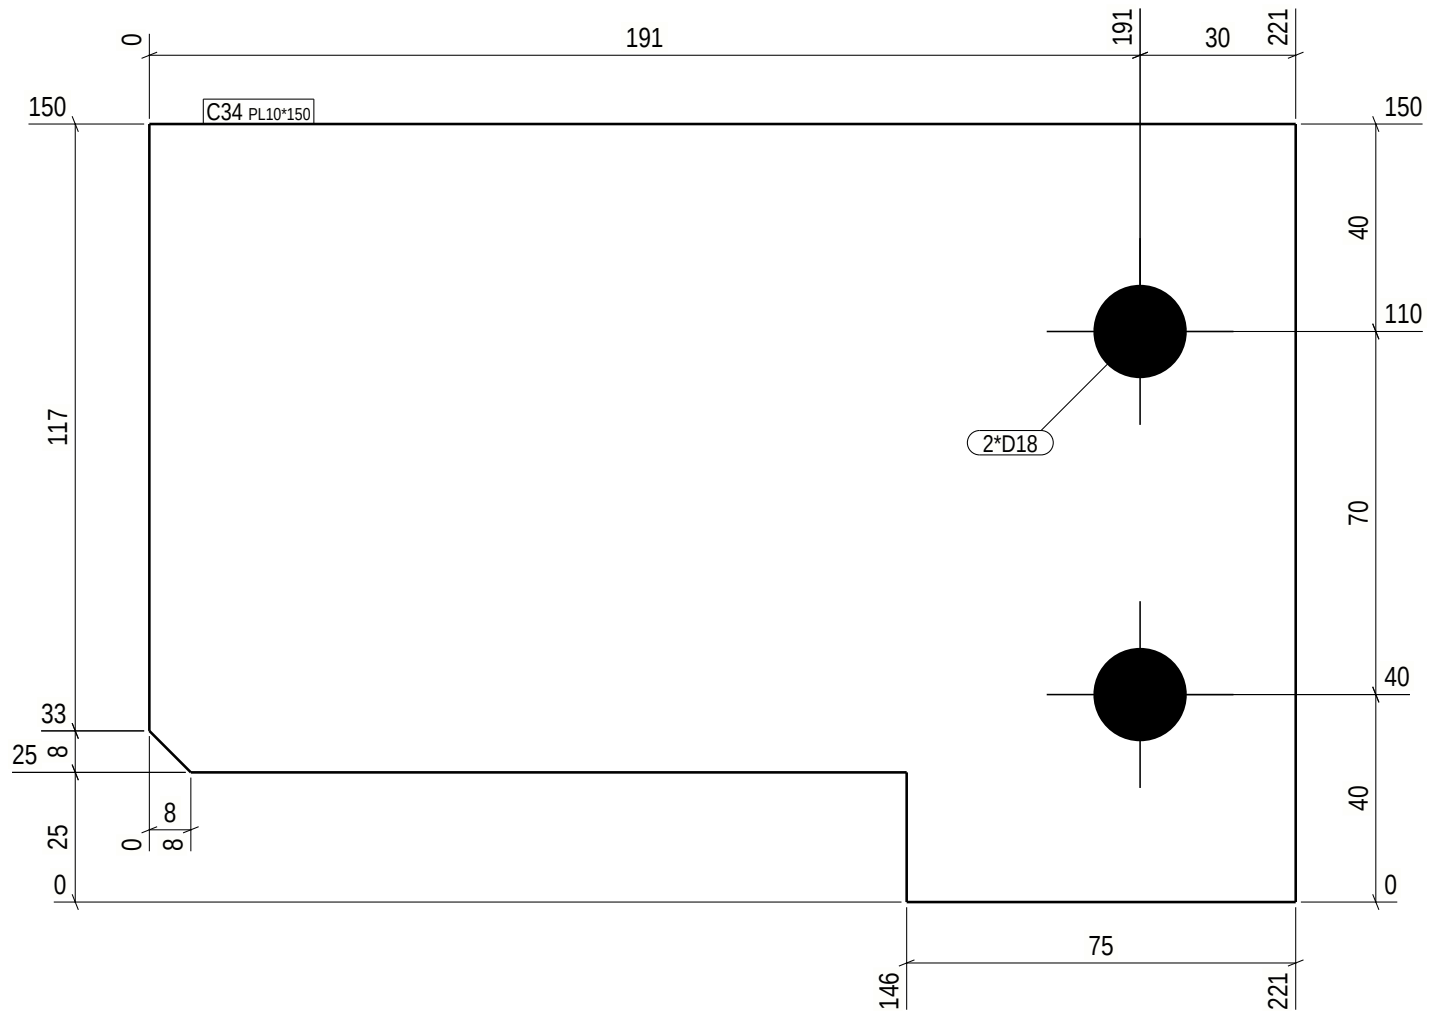

GENERAL NOTES:

For your safety, check weight before handling:
0-5kg Light 5-15kg Normal 15+kg Heavy

MATERIAL LIST FOR PART - C34

32 PARTS REQUIRED

POS. No.	PROFILE	No.	GRADE	L (mm)	AREA (m ²)	WEIGHT (kg)
C34	PL10*150	1	S355J2	221	0.1	2.3

TOTAL WEIGHT FOR 32 PARTS 74.0

Part list	Qty.
BN	32

Execution class: EXC 2

No utilization on drawings = over 50%

V-SEAM
Utilization under 50%
EXC 2=> Acc. to process control
EXC 3=> 20% UT
Utilization over 50%
EXC 2=> 10% UT
EXC 3=> 20% UT

* o 3 0 4 8 0 - 2 *



DS Steelkonstruktion

* WC 3 4 *

PROJECT	Akkasæter Lager- og vedlikeholdshall		PHASE	2 / Phase 2	
MEMBER	Plade		QUANTITY:	32	PROJECT No 30480-2
REVISION	ISSUED: 07.11.2025		DRAFTER:	ZLL	DRAWING No. C.34
			BIM control:	SST	