


Tekla Structures

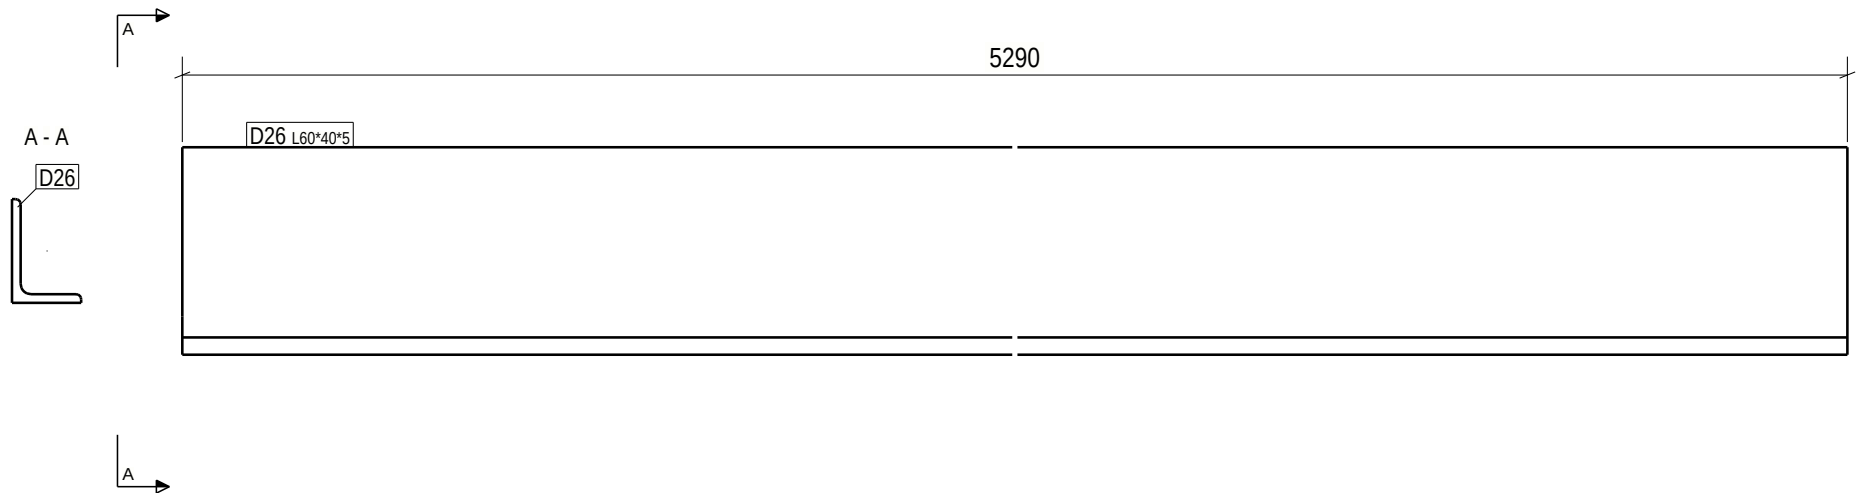

GENERAL NOTES:						
For your safety, check weight before handling:						
0-5kg Light 5-15kg Normal 15+kg Heavy						
MATERIAL LIST FOR PART - D26						
2 PARTS REQUIRED						
POS. No.	PROFILE	No.	GRADE	L (mm)	AREA (m ²)	WEIGHT (kg)
D26	L60*40*5	1	S355J2	5290	1.0	19.9 !!
TOTAL WEIGHT FOR				2	PARTS	39.8

Part list	Qty.
BN	2

Execution class: EXC 2		* o 3 0 4 8 0 - 2 *  DS <i>Skalkonstruktion</i> * WD 2 6 *			
No utilization on drawings = over 50%					
V-SEAM Utilization under 50% EXC 2=> Acc. to process control EXC 3=> 20% UT Utilization over 50% EXC 2=> 10% UT EXC 3=> 20% UT		PROJECT	Akkasæter Lager- og vedlikeholdshall		PHASE 2 / Phase 2
		MEMBER	Drager		QUANTITY: 2 PROJECT No 30480-2
		REVISION	ISSUED: 07.11.2025		DRAFTER: ZLL BIM control: SST DRAWING No. D.26