


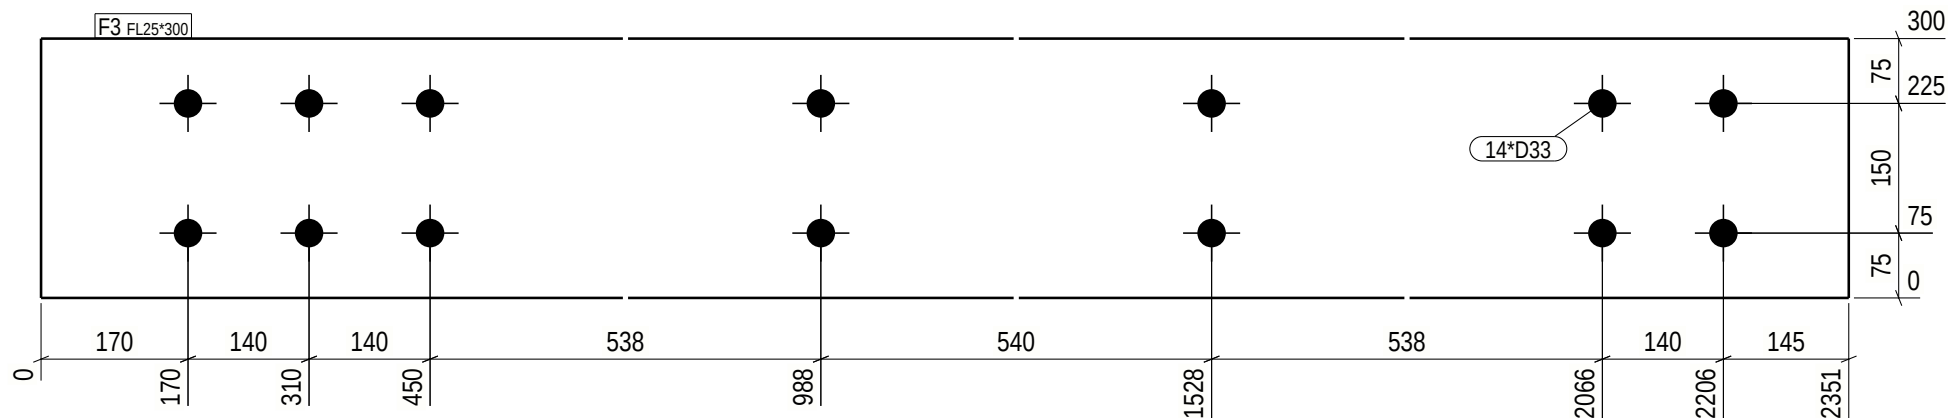

GENERAL NOTES:						
For your safety, check weight before handling:						
0-5kg Light 5-15kg Normal 15+kg Heavy						
MATERIAL LIST FOR PART - F3				32 PARTS REQUIRED		
POS. No.	PROFILE	No.	GRADE	L (mm)	AREA (m ²)	WEIGHT (kg)
F3	FL25*300	1	S355J2	2351	1.5	138.4 !!
TOTAL WEIGHT FOR				32	PARTS	4429.3

Part list	Qty.
BN	16
FT	16

Execution class: EXC 2		* o 3 0 4 8 0 - 2 *  DS <i>Stålkonstruktion</i> * W F 3 *			
No utilization on drawings = over 50%					
V-SEAM Utilization under 50% EXC 2=> Acc. to process control EXC 3=> 20% UT Utilization over 50% EXC 2=> 10% UT EXC 3=> 20% UT		PROJECT	Akkasæter Lager- og vedlikeholdshall		PHASE 2 / Phase 2
		MEMBER	Fladstål		QUANTITY: 32
		REVISION	ISSUED: 07.11.2025		PROJECT No 30480-2
			DRAFTER: ZLL BIM control: SST		DRAWING No. F.3